



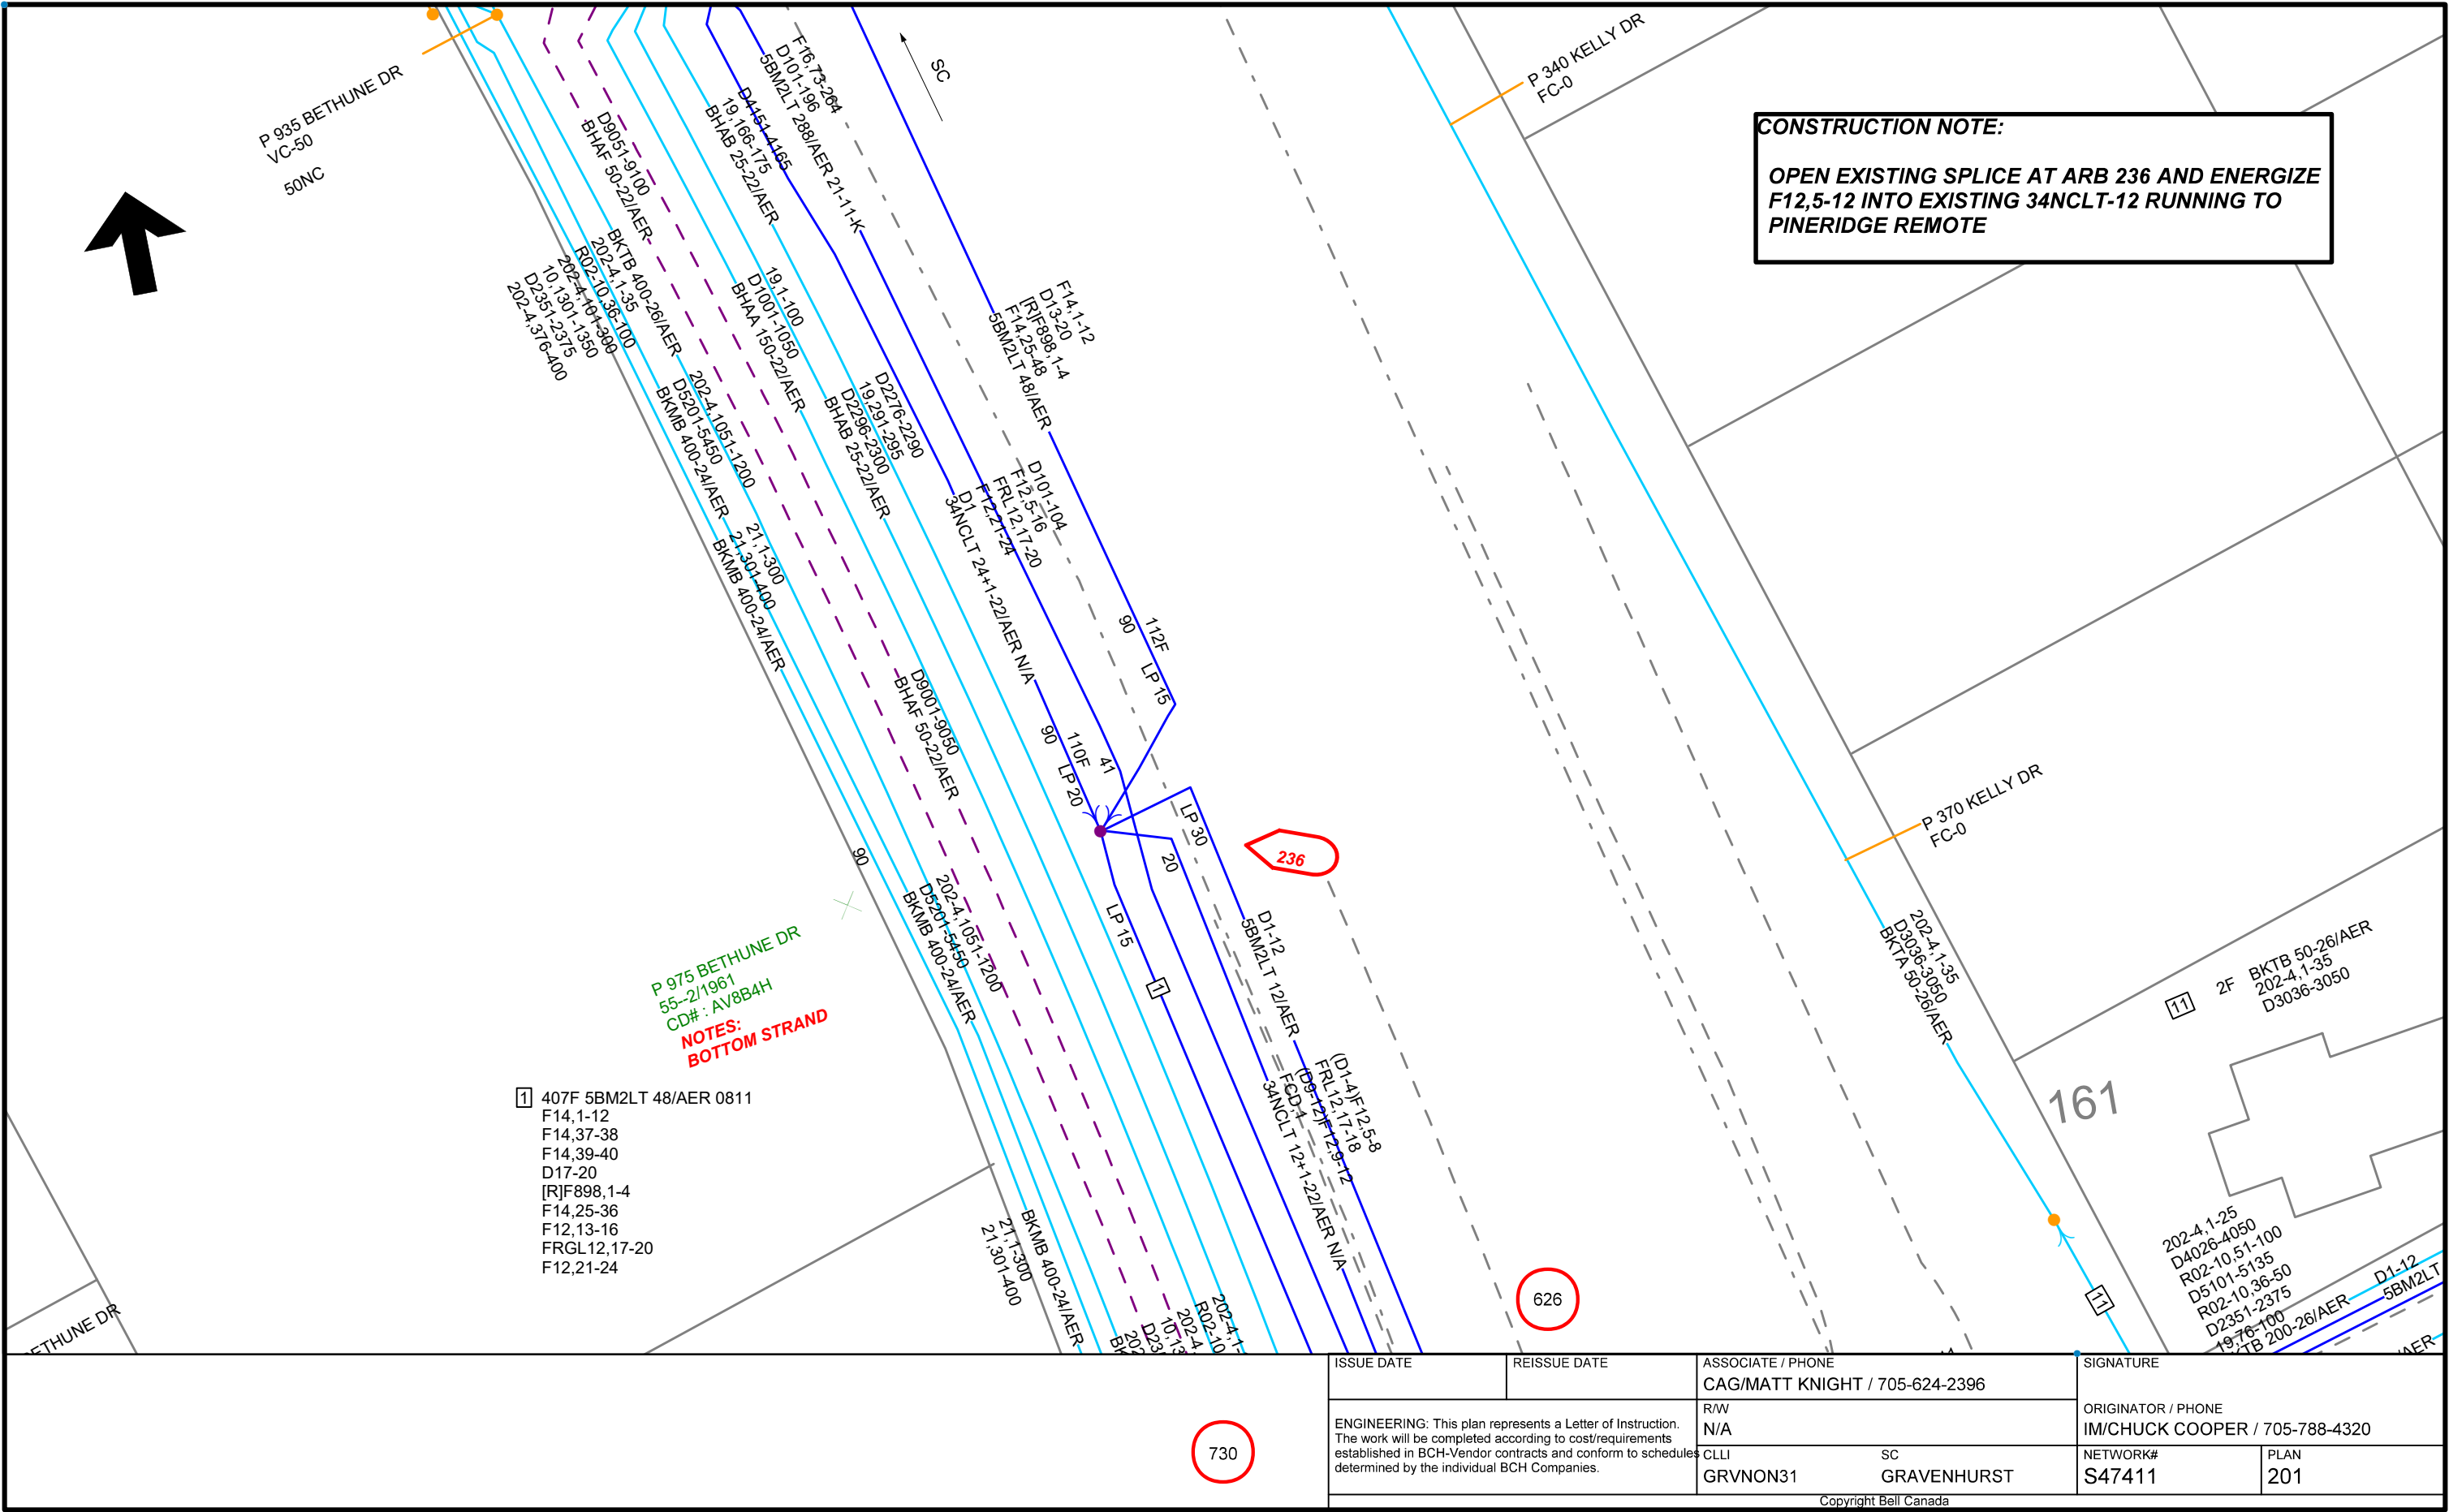


ISSUE DATE	REISSUE DATE	ASSOCIATE / PHONE CAG/MATT KNIGHT / 705-624-2396		SIGNATURE	
ENGINEERING: This plan represents a Letter of Instruction. The work will be completed according to cost/requirements established in BCH-Vendor contracts and conform to schedules determined by the individual BCH Companies.		R/W N/A		ORIGINATOR / PHONE IM/CHUCK COOPER / 705-788-4320	
		CLLI GRVNON31	SC GRAVENHURST	NETWORK# S47411	PLAN 201
		Copyright Bell Canada			

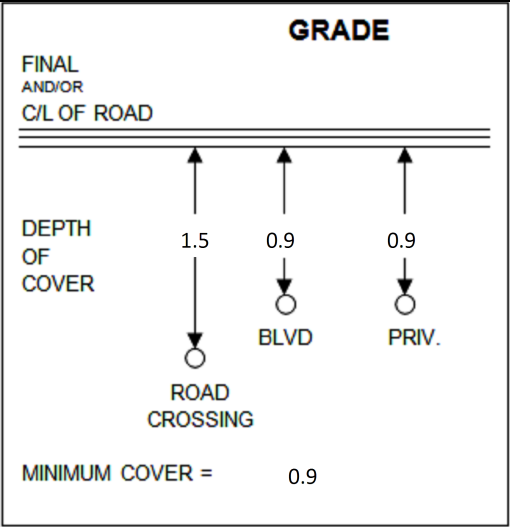


WARNING - RESIDENTS WARNED OF IMPROPER GAS LINE PLACEMENT IN AND DAMAGE IN THE PAST - PLEASE TAKE EXTRA CARE

CONSTRUCTION NOTES:


- 1) NEW CONDUIT ALONG ROADWAYS TO BE DRILLED
- 2) CONDUIT BEING PLACED TO SIDES OF HOMES TO BE PLOWED TO D MARK & COILED AT SIDE OF HOME. JET DROPS TO BE PLACED IN DUCTS
- 3) ALL PITS TO BE VACCED
- 4) WHEN REPLACING PEDESTALS ENSURE PED IS BELL OWNED AS CABLE TV PEDESTALS ARE ALSO BROWN
- 5) REPLACE EXISTING COIL DROPS IN PEDESTALS
- 6) AT ANY LOCATION WHERE A DROP WIRE GOES DIRECTLY TO A HOUSE THE CUSTOMER MUST BE ASKED IF THEY WOULD LIKE THE FIBRE RUN TO THEIR HOME AT NO COST REGARDLESS IF THEY GET THE SERVICE OR NOT. IF THE CUSTOMER DOES NOT WANT THE DROP RUN TO THEIR HOME A FLOWER POT WILL BE PLACED ON THE PROPERTY LINE AND THE DROP WIRE WILL BE COILED INSIDE FOR FUTURE
- 7) SEE PLAN 724 FOR DUCT CONNECTION DETAILS

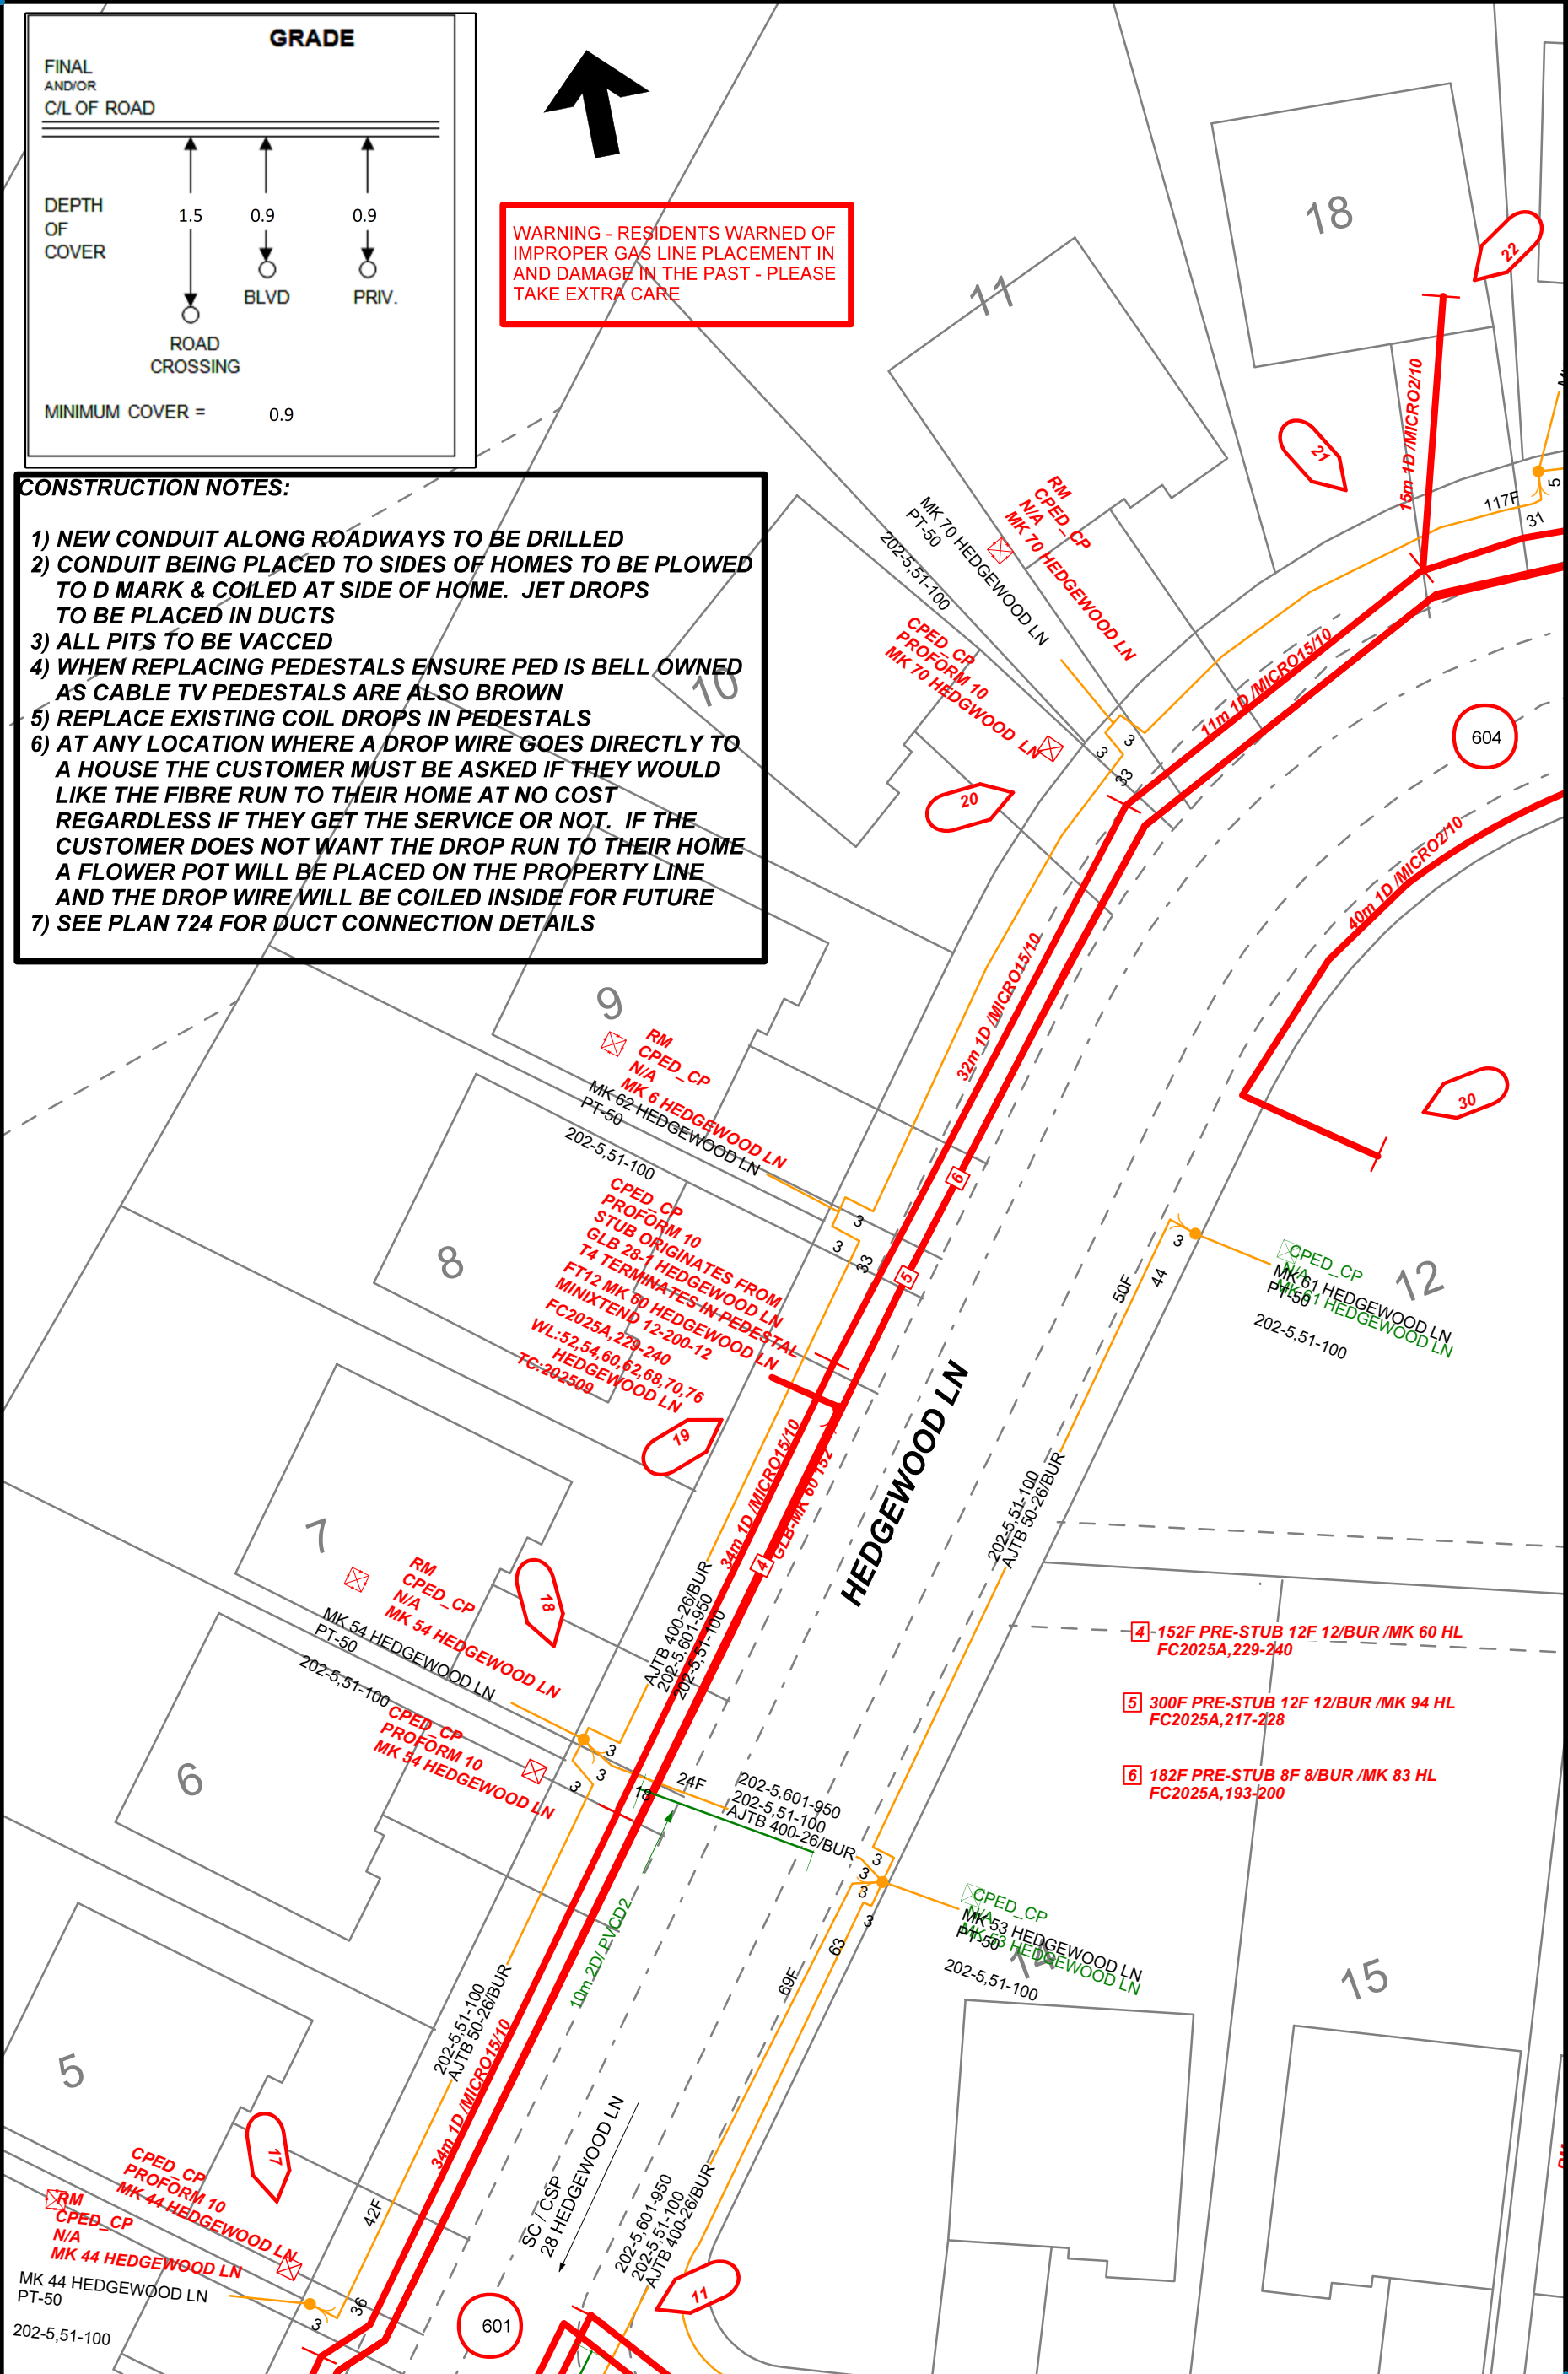

730	ISSUE DATE	REISSUE DATE	ASSOCIATE / PHONE CAG/MATT KNIGHT / 705-624-2396	SIGNATURE	
	ENGINEERING: This plan represents a Letter of Instruction. The work will be completed according to cost/requirements established in BCH-Vendor contracts and conform to schedules determined by the individual BCH Companies.		R/W N/A	ORIGINATOR / PHONE IM/CHUCK COOPER / 705-788-4320	
			CLLI GRVNON31	SC GRAVENHURST	NETWORK# S47411
					PLAN 603

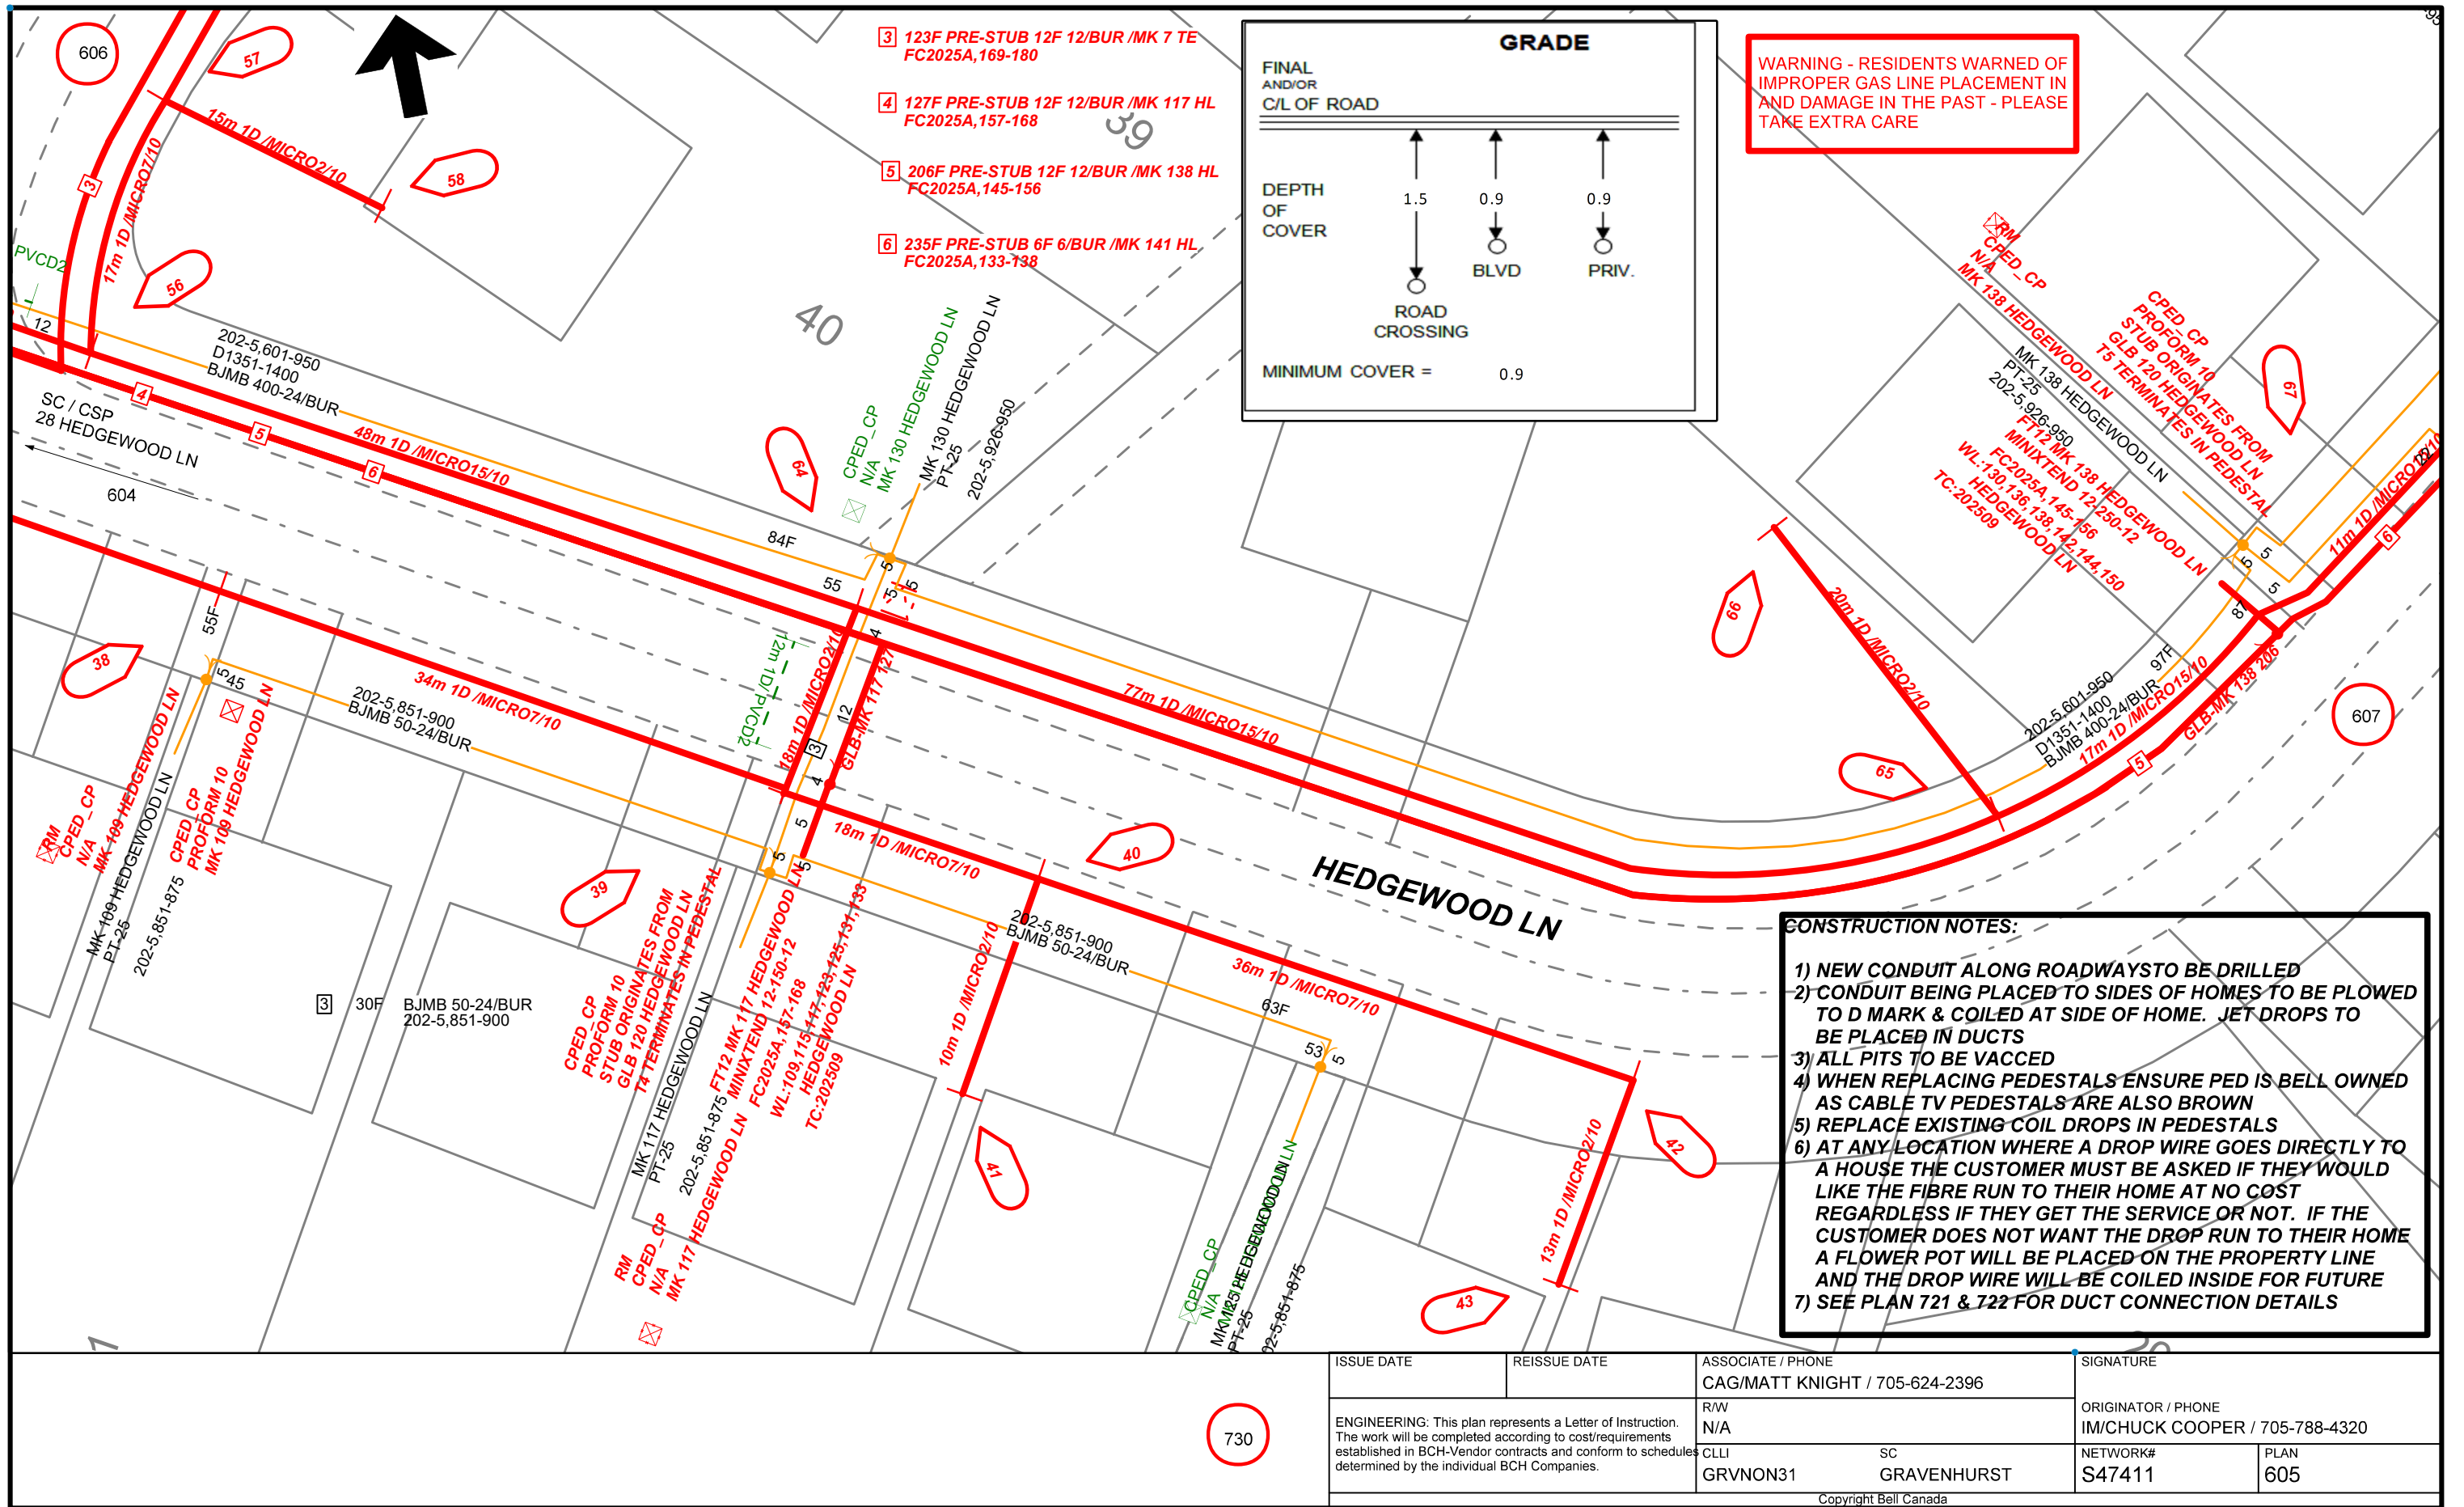


- 3 123F PRE-STUB 12F 12/BUR /MK 7 TE
FC2025A,169-180
- 4 127F PRE-STUB 12F 12/BUR /MK 117 HL
FC2025A,157-168
- 5 206F PRE-STUB 12F 12/BUR /MK 138 HL
FC2025A,145-156
- 6 235F PRE-STUB 6F 6/BUR /MK 141 HL
FC2025A,133-138

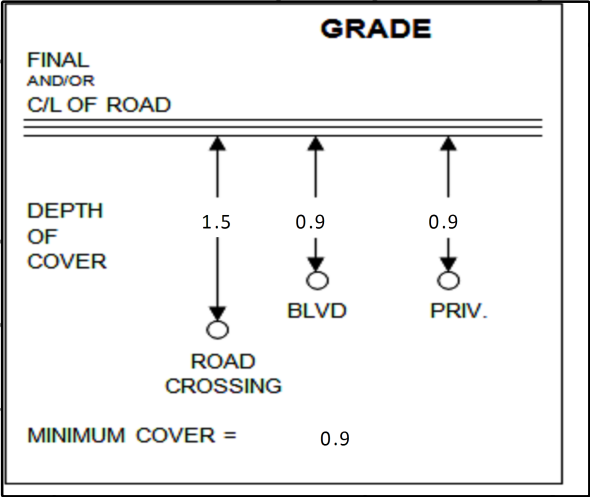

WARNING - RESIDENTS WARNED OF IMPROPER GAS LINE PLACEMENT IN AND DAMAGE IN THE PAST - PLEASE TAKE EXTRA CARE

- CONSTRUCTION NOTES:**
- 1) NEW CONDUIT ALONG ROADWAYS TO BE DRILLED
 - 2) CONDUIT BEING PLACED TO SIDES OF HOMES TO BE PLOWED TO D MARK & COILED AT SIDE OF HOME. JET DROPS TO BE PLACED IN DUCTS
 - 3) ALL PITS TO BE VACCED
 - 4) WHEN REPLACING PEDESTALS ENSURE PED IS BELL OWNED AS CABLE TV PEDESTALS ARE ALSO BROWN
 - 5) REPLACE EXISTING COIL DROPS IN PEDESTALS
 - 6) AT ANY LOCATION WHERE A DROP WIRE GOES DIRECTLY TO A HOUSE THE CUSTOMER MUST BE ASKED IF THEY WOULD LIKE THE FIBRE RUN TO THEIR HOME AT NO COST REGARDLESS IF THEY GET THE SERVICE OR NOT. IF THE CUSTOMER DOES NOT WANT THE DROP RUN TO THEIR HOME A FLOWER POT WILL BE PLACED ON THE PROPERTY LINE AND THE DROP WIRE WILL BE COILED INSIDE FOR FUTURE
 - 7) SEE PLAN 721 & 722 FOR DUCT CONNECTION DETAILS

ISSUE DATE	REISSUE DATE	ASSOCIATE / PHONE CAG/MATT KNIGHT / 705-624-2396	SIGNATURE
ENGINEERING: This plan represents a Letter of Instruction. The work will be completed according to cost/requirements established in BCH-Vendor contracts and conform to schedules determined by the individual BCH Companies.		R/W N/A	ORIGINATOR / PHONE IM/CHUCK COOPER / 705-788-4320
CLLI GRVNON31		SC GRAVENHURST	NETWORK# S47411
			PLAN 605

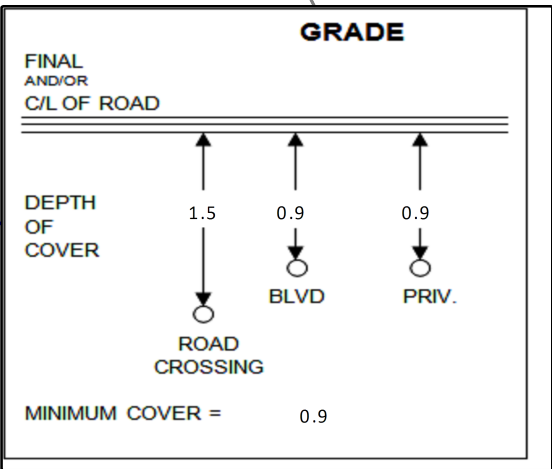

WARNING - RESIDENTS WARNED OF IMPROPER GAS LINE PLACEMENT IN AND DAMAGE IN THE PAST - PLEASE TAKE EXTRA CARE

A 206F 5BDXLT 72/BUR 22-06-M D1-72

P 18 PINEDALE INN RD
40-G-4/1987
CD# : AAB454

PINEDALE INN RD

17PI

77

82

81

A COIL 26

IN DUCT 180

95m 1D MICRO7/10

HEDGEWOOD LN

CPED_CP
PROFORM 10
MK 166 HEDGEWOOD LN

MKT 166 HEDGEWOOD LN
PT-25
202-5,926-950
RM CPED_CP
N/A
MK 166 HEDGEWOOD LN

1 50F PRE-STUB 8F 8/BUR /MK 160 HL FC2025A,89-96

CPED_CP
PROFORM 10
STUB TERMINATES IN
GLB 189 PINERIDGE GATE
T1 TERMINATES IN PEDESTAL
F18 MK 160 HEDGEWOOD LN
MINIXTEND 8-100-8
FC2025A,89-96
WL:152 158,160,168
HEDGEWOOD LN
TC:205209

MK 160 HEDGEWOOD LN
PT-25
202-5,926-950
RM CPED_CP
N/A
MK 160 HEDGEWOOD LN

SC / CSP
28 HEDGEWOOD LN

MK 160 HEDGEWOOD LN
PT-25
202-5,926-950
MB 400-24/BUR
77/40

18m 1D MICRO7/10

GLB-MK 160 90

CONSTRUCTION NOTES:

- 1) NEW CONDUIT ALONG ROADWAYS TO BE DRILLED
- 2) CONDUIT BEING PLACED TO SIDES OF HOMES TO BE PLOWED TO D MARK AND COILED AT SIDE OF HOME. JET DROPS TO BE PLACED IN DUCTS
- 3) ALL PITS TO BE VACCED
- 4) WHEN REPLACING PEDESTALS ENSURE PED IS BELL OWNED AS CABLE PEDESTALS ARE ALSO BROWN
- 5) REPLACE EXISTING COIL DROP IN PEDESTALS
- 6) AT ANY LOCATION WHERE A DROP WIRE GOES DIRECTLY TO TO A HOUSE THE CUSTOMER MUST BE ASKED IF THEY WOULD LIKE THE FIBRE RUN TO THEIR HOME AT NO COST, REGARDLESS IF THEY GET THE SERVICE OR NOT. IF THE CUSTOMER DOES NOT WANT THE DROP RUN TO THEIR HOME A FLOWER POT WILL BE PLACED ON THE PROPERTY LINE AND THE DROP WILL BE COILED INSIDE FOR FUTURE
- 7) SEE PLAN 719 FOR DUCT CONNECTION DETAILS
- 8) PLACE NEW 5BDLXT-72 CABLE IN MICRODUCT FROM GLB TO P 18 PINEDALE INN RD AND LEAVE 26m OF CABLE COILED AT BASE OF POLE FOR FUTURE

FINAL LENGTH 5BDXLT-72 = 226m BUR

ISSUE DATE

REISSUE DATE

ASSOCIATE / PHONE

CAG/MATT KNIGHT / 705-624-2396

SIGNATURE

ENGINEERING: This plan represents a Letter of Instruction. The work will be completed according to cost/requirements established in BCH-Vendor contracts and conform to schedules determined by the individual BCH Companies.

R/W
N/A

CLLI

GRVNON31

SC

GRAVENHURST

ORIGINATOR / PHONE


IM/CHUCK COOPER / 705-788-4320


NETWORK#

S47411

PLAN


608

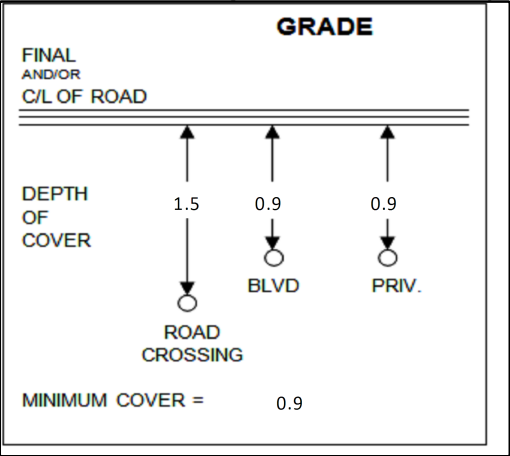

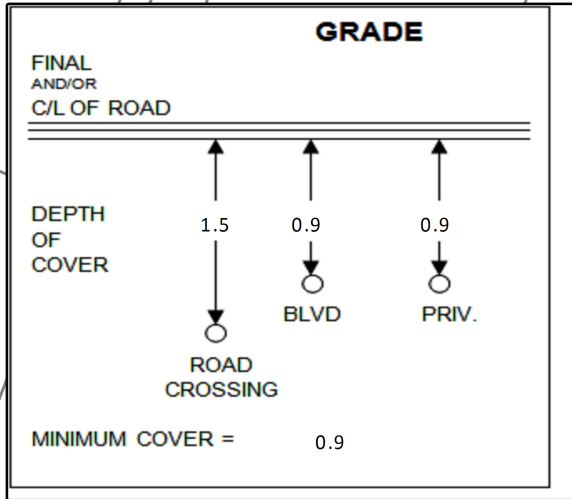


WARNING - RESIDENTS WARNED OF IMPROPER GAS LINE PLACEMENT IN AND DAMAGE IN THE PAST - PLEASE TAKE EXTRA CARE


- CONSTRUCTION NOTES:**
- 1) NEW CONDUIT ALONG ROADWAYS TO BE DRILLED
 - 2) CONDUIT BEING PLACED TO SIDES OF HOMES TO BE PLOWED TO D MARK AND COILED AT SIDE OF HOME. JET DROPS TO BE PLACED IN DUCTS
 - 3) ALL PITS TO BE VACCED
 - 4) WHEN REPLACING PEDESTALS ENSURE PED IS BELLOWED AS CABLE TV PEDESTALS ARE ALSO BROWN
 - 5) REPLACE EXISTING COIL DROPS IN PEDESTALS
 - 6) AT ANY LOCATION WHERE A DROP WIRE GOES DIRECTLY TO A HOUSE THE CUSTOMER MUST BE ASKED IF THEY WOULD LIKE THE FIBRE RUN TO THEIR HOME AT NO COST REGARDLESS IF THEY GET THE SERVICE OR NOT. IF THE CUSTOMER DOES NOT WANT THE DROP RUN TO THEIR HOME A FLOWER POT WILL BE PLACED ON THE PROPERTY LINE
 - 7) SEE PLAN 716 & 717 FOR DUCT CONNECTION DETAILS

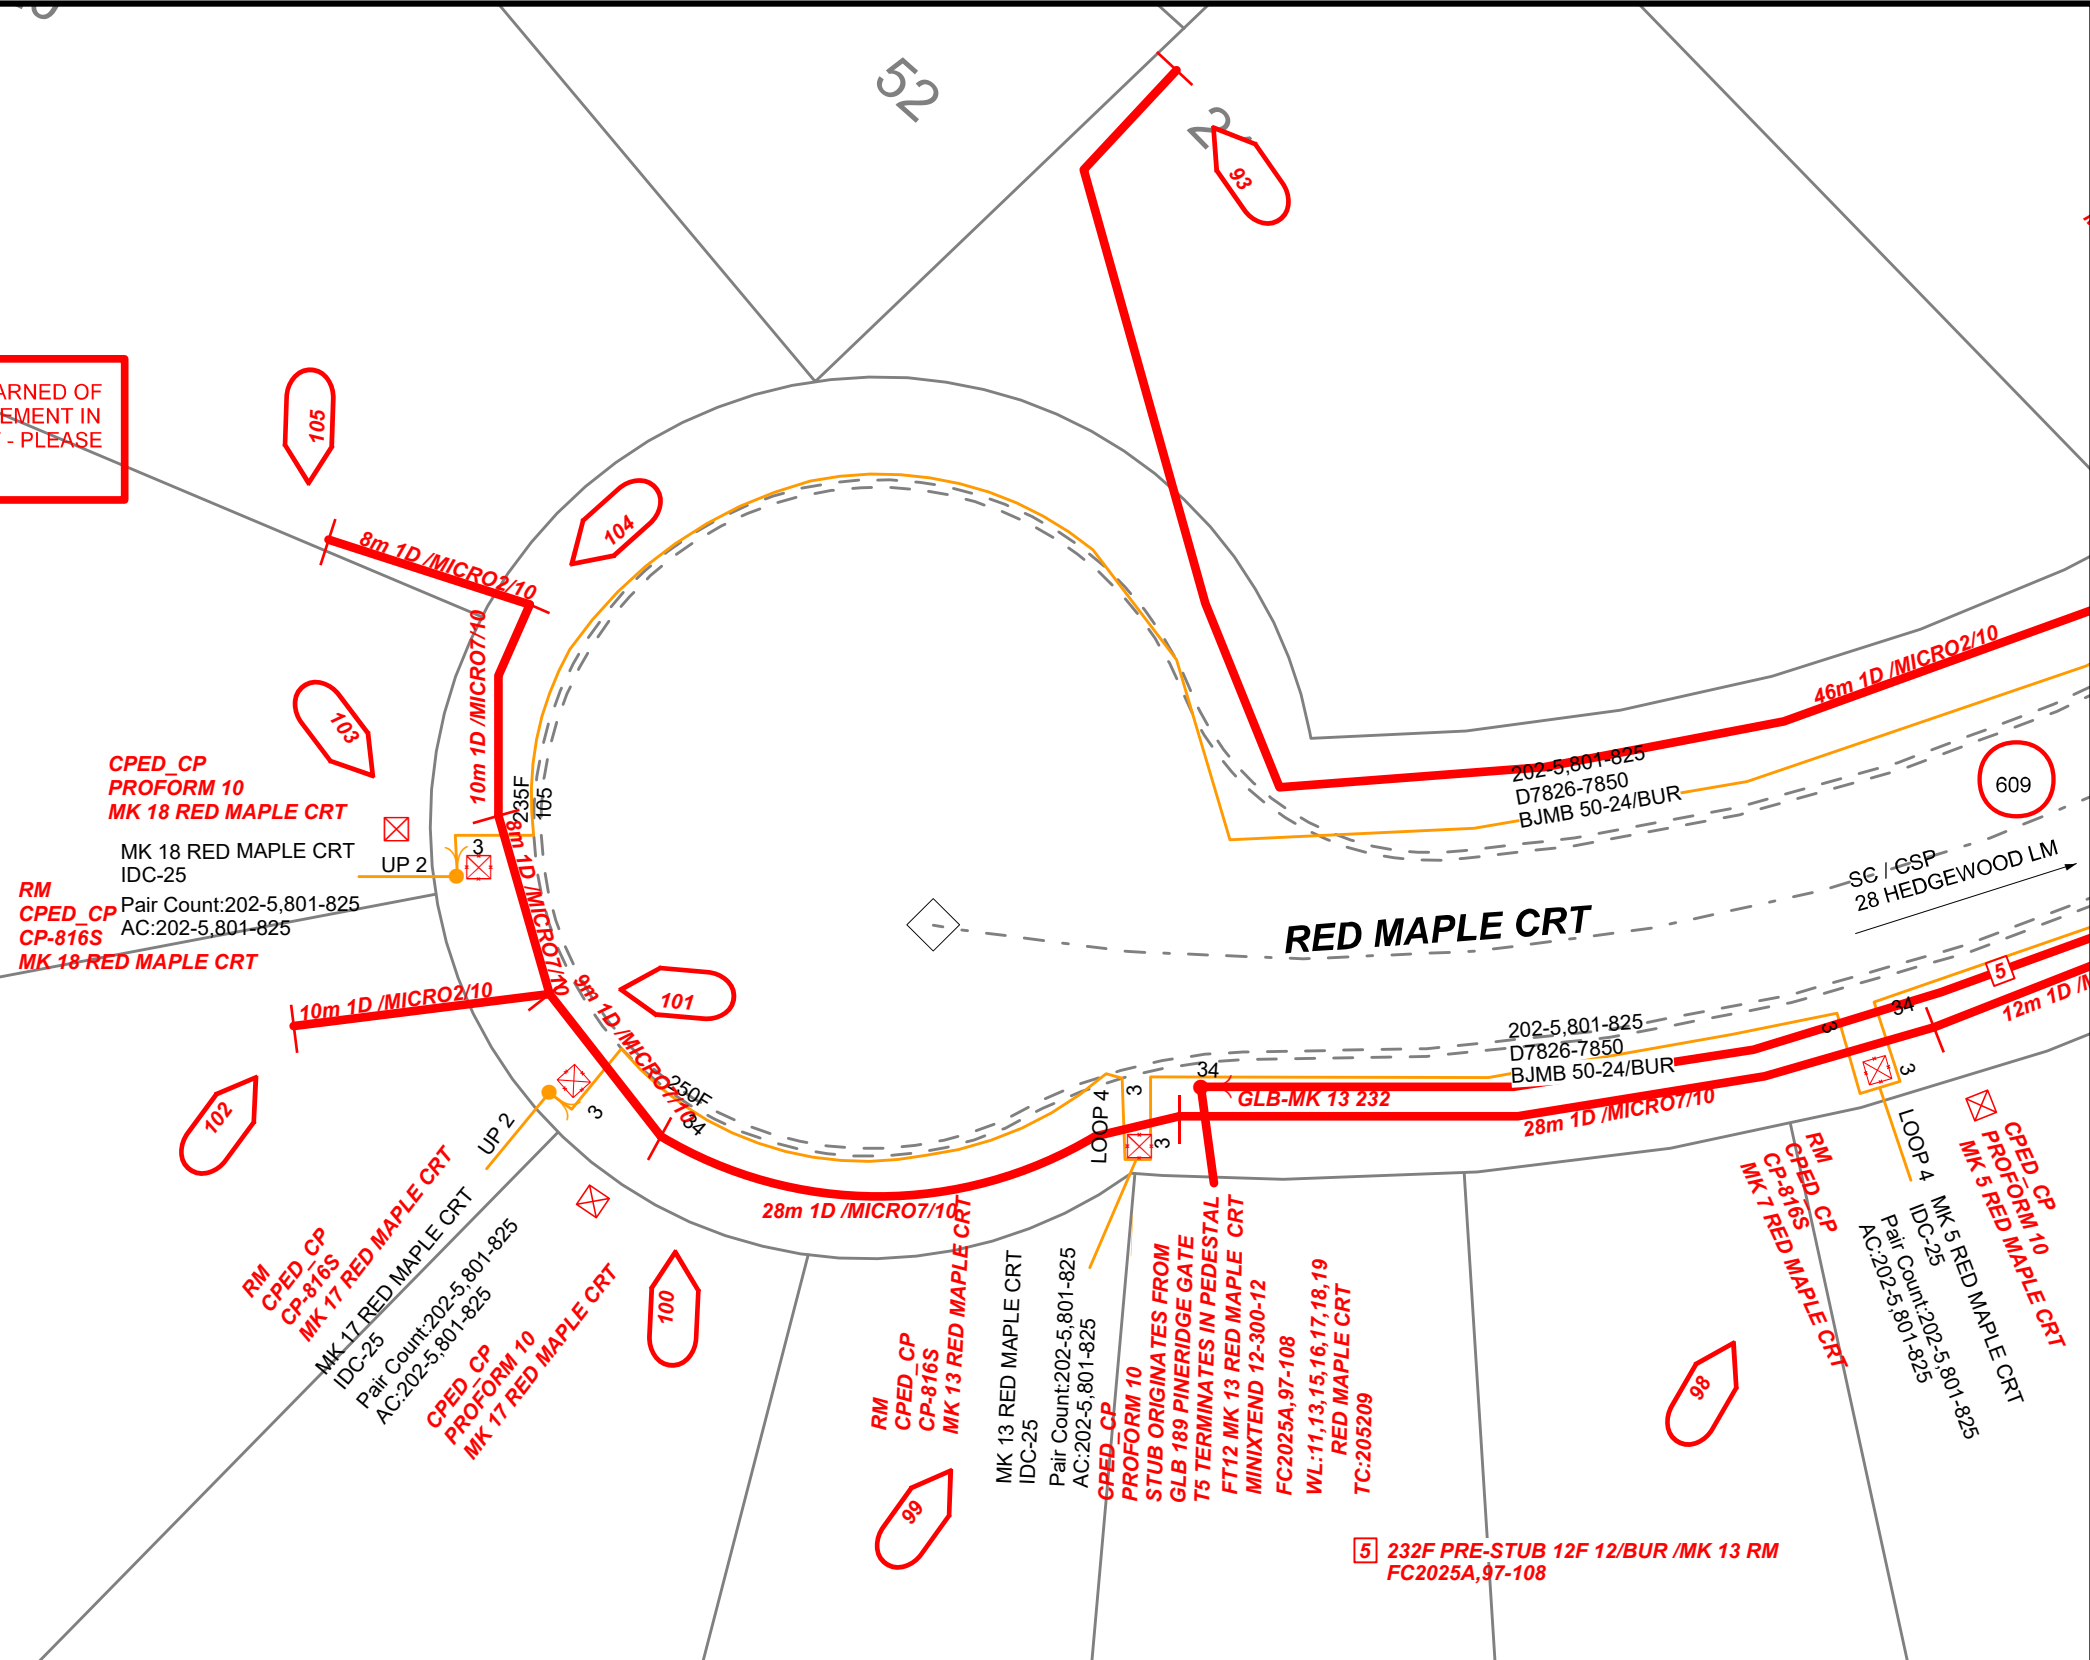

ISSUE DATE	REISSUE DATE	ASSOCIATE / PHONE CAG/MATT KNIGHT / 705-624-2396	SIGNATURE
ENGINEERING: This plan represents a Letter of Instruction. The work will be completed according to cost/requirements established in BCH-Vendor contracts and conform to schedules determined by the individual BCH Companies.		R/W N/A	ORIGINATOR / PHONE IM/CHUCK COOPER / 705-788-4320
CLLI GRVNON31	SC GRAVENHURST	NETWORK# S47411	PLAN 610

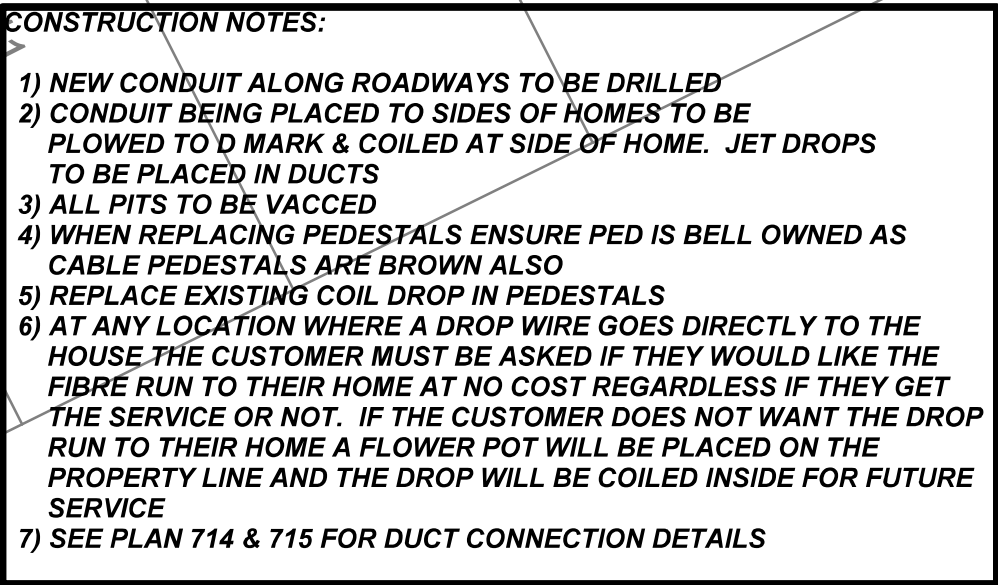

ISSUE DATE	REISSUE DATE	ASSOCIATE / PHONE CAG/MATT KNIGHT / 705-624-2396		SIGNATURE	
ENGINEERING: This plan represents a Letter of Instruction. The work will be completed according to cost/requirements established in BCH-Vendor contracts and conform to schedules determined by the individual BCH Companies.		R/W N/A		ORIGINATOR / PHONE IM/CHUCK COOPER / 705-788-4320	
		CLLI GRVNON31	SC GRAVENHURST	NETWORK# S47411	PLAN 611

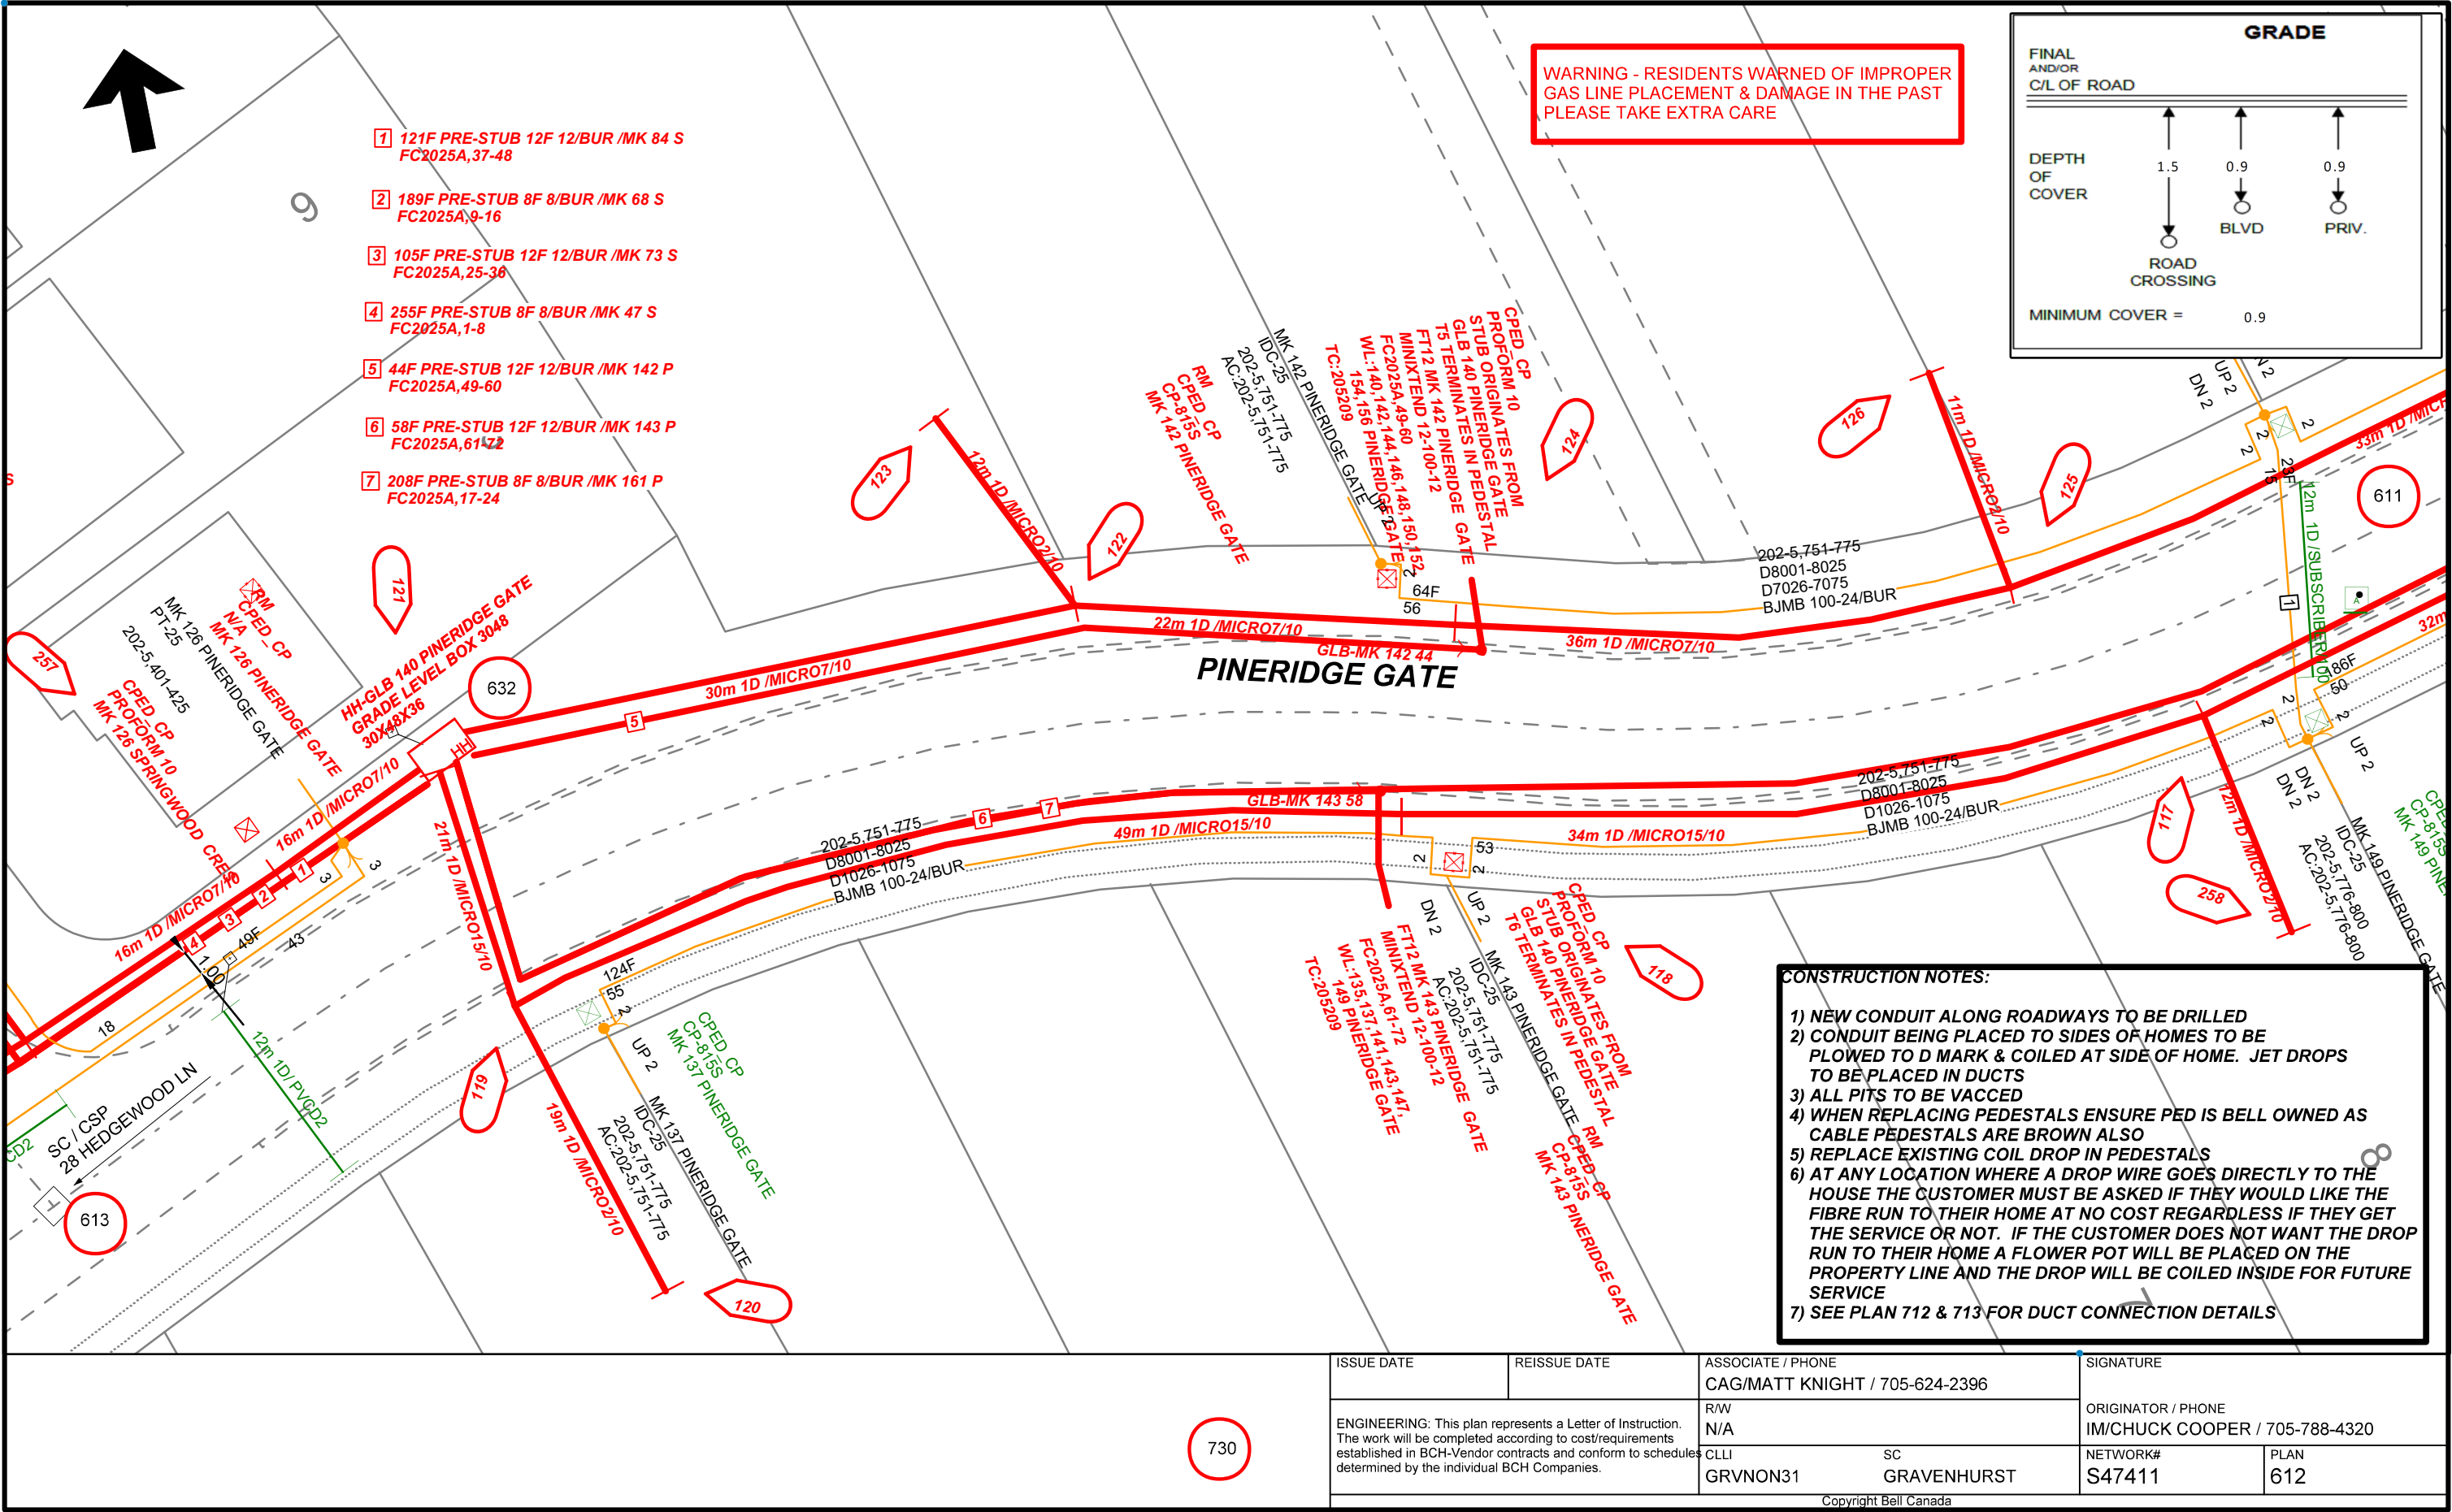




- 1) NEW CONDUIT ALONG ROADWAYS TO BE DRILLED
- 2) CONDUIT BEING PLACED TO SIDES OF HOMES TO BE PLOWED TO D MARK & COILED AT SIDE OF HOME. JET DROPS TO BE PLACED IN DUCTS
- 3) ALL PITS TO BE VACCED
- 4) WHEN REPLACING PEDESTALS ENSURE PED IS BELL OWNED AS CABLE PEDESTALS ARE BROWN ALSO
- 5) REPLACE EXISTING COIL DROP IN PEDESTALS
- 6) AT ANY LOCATION WHERE A DROP WIRE GOES DIRECTLY TO THE HOUSE THE CUSTOMER MUST BE ASKED IF THEY WOULD LIKE THE FIBRE RUN TO THEIR HOME AT NO COST REGARDLESS IF THEY GET THE SERVICE OR NOT. IF THE CUSTOMER DOES NOT WANT THE DROP RUN TO THEIR HOME A FLOWER POT WILL BE PLACED ON THE PROPERTY LINE AND THE DROP WILL BE COILED INSIDE FOR FUTURE SERVICE
- 7) SEE PLAN 711 & 712 FOR DUCT CONNECTION DETAILS




ISSUE DATE	REISSUE DATE	ASSOCIATE / PHONE CAG/MATT KNIGHT / 705-624-2396	SIGNATURE	
ENGINEERING: This plan represents a Letter of Instruction. The work will be completed according to cost/requirements established in BCH-Vendor contracts and conform to schedules determined by the individual BCH Companies.		R/W N/A	ORIGINATOR / PHONE IM/CHUCK COOPER / 705-788-4320	
		CLLI GRVNON31	SC GRAVENHURST	NETWORK# S47411
Copyright Bell Canada				

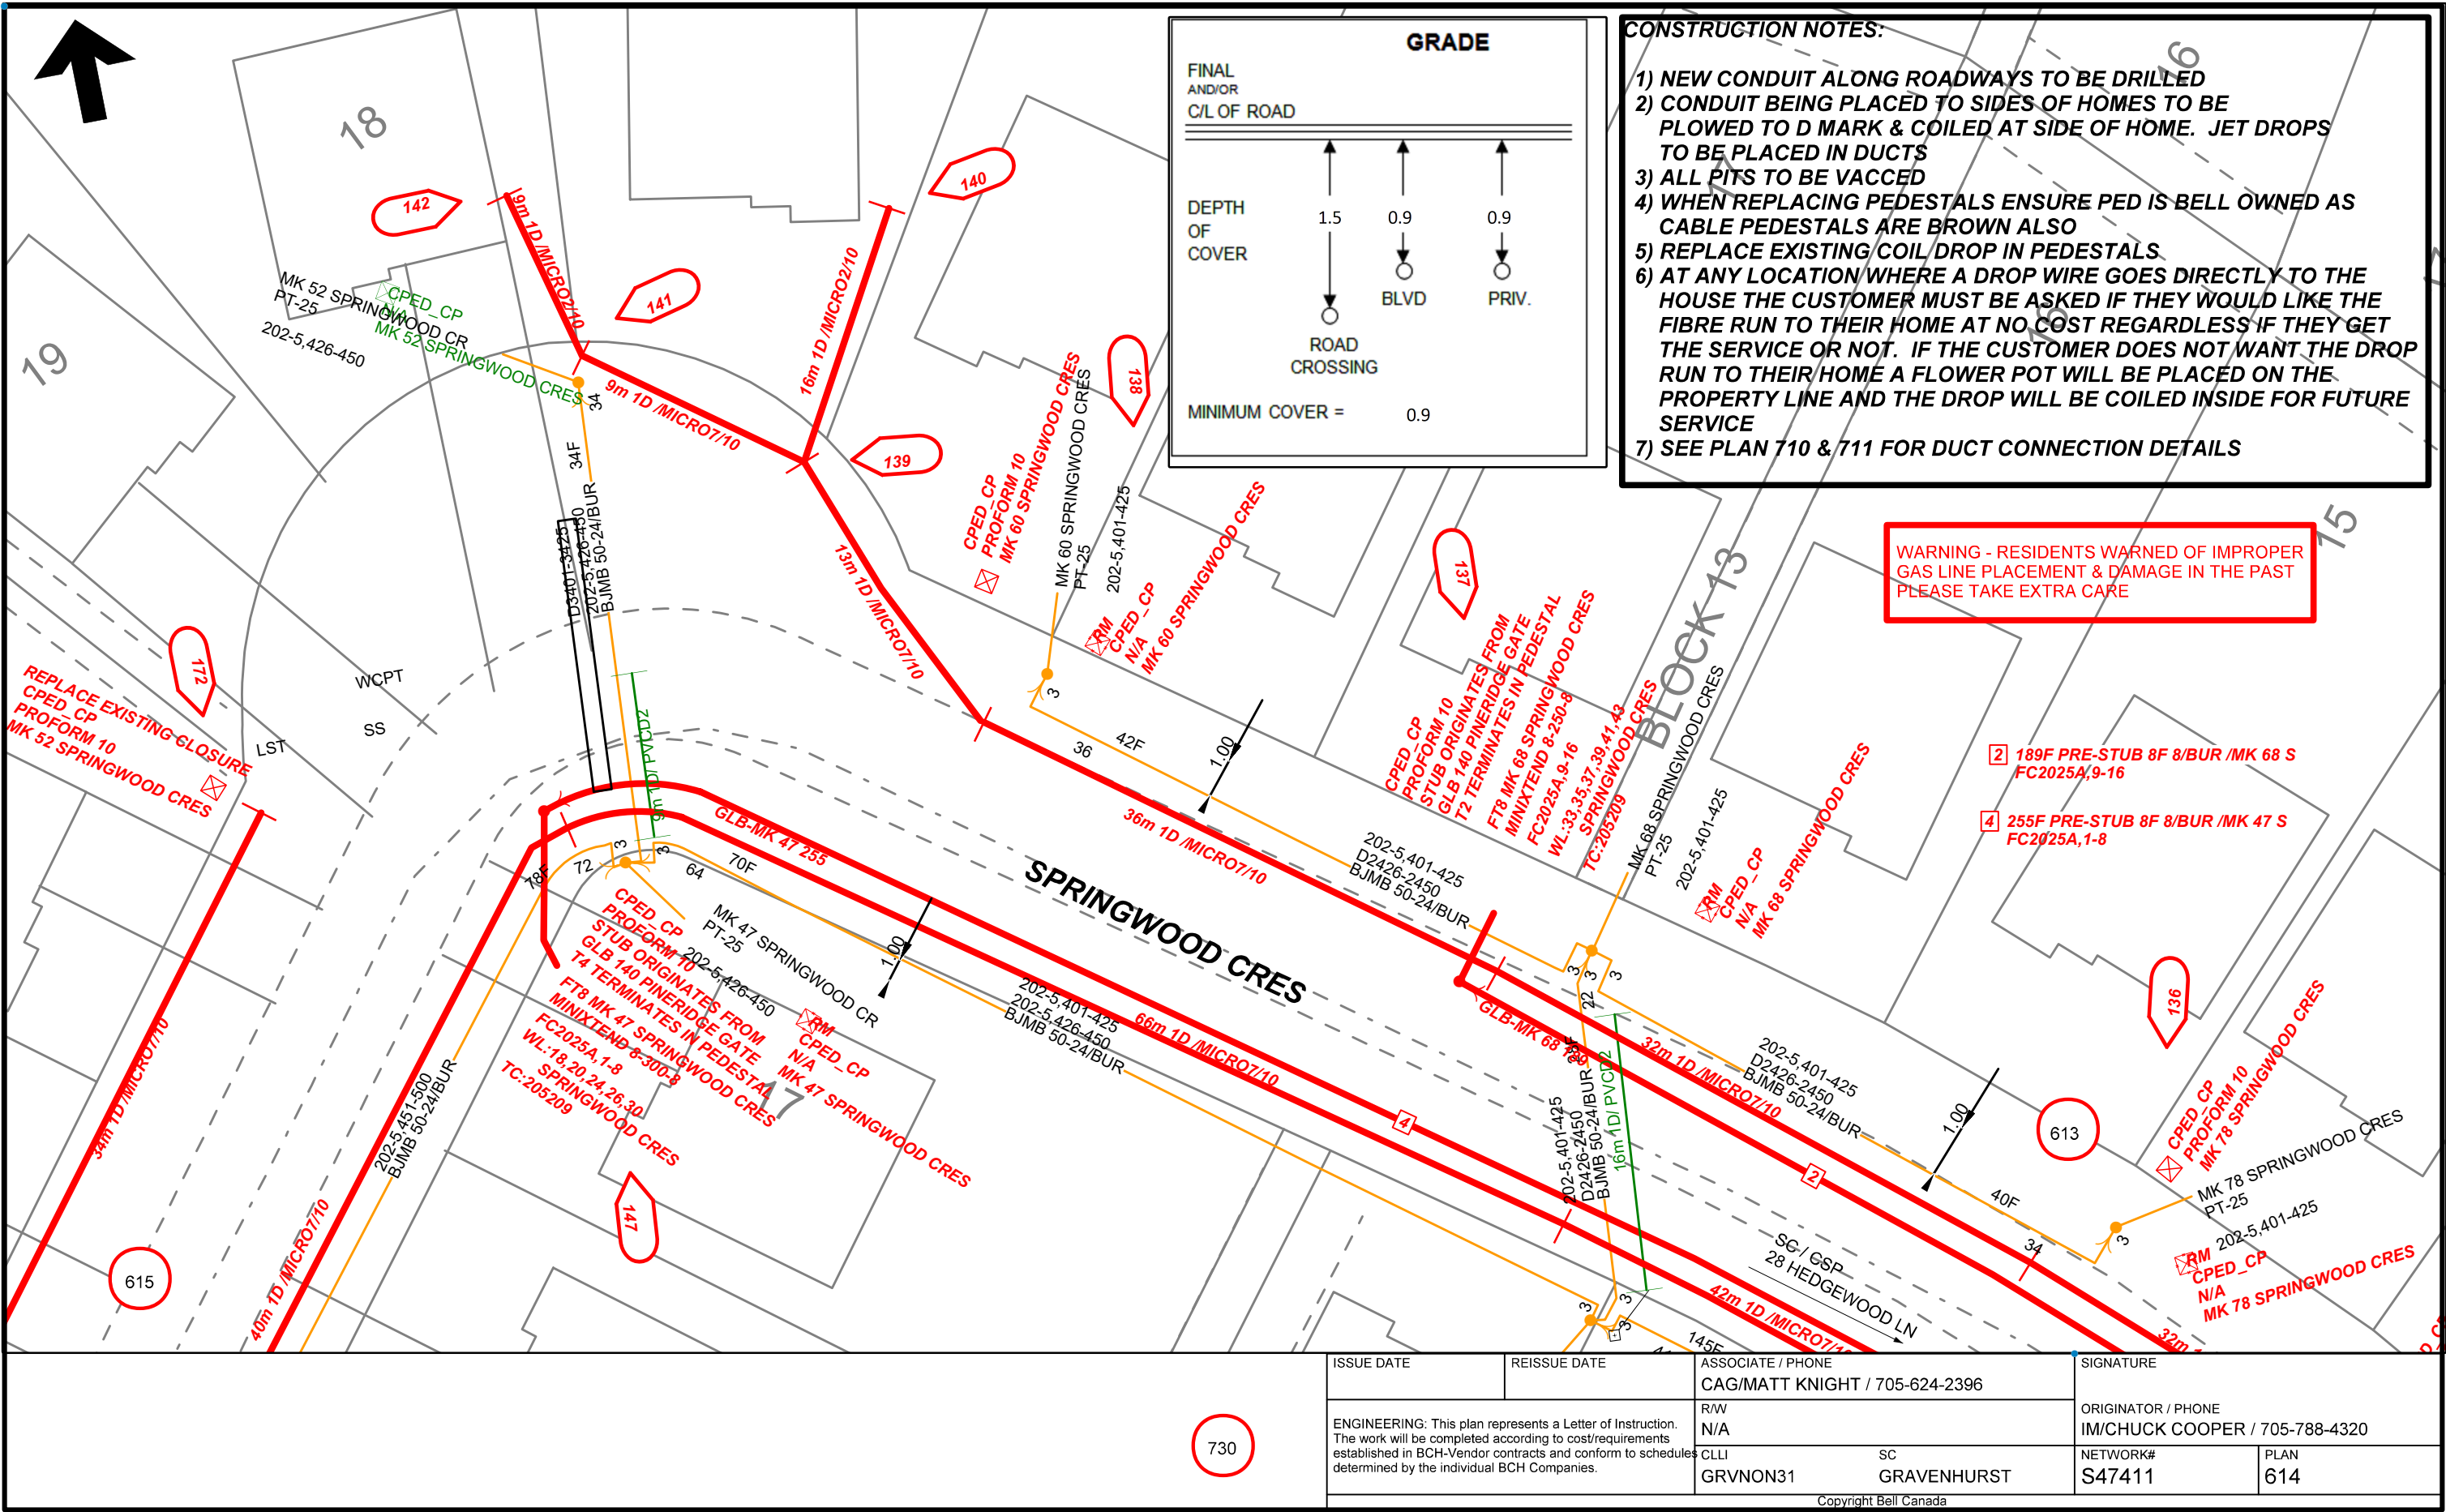

- CONSTRUCTION NOTES:**
- 1) NEW CONDUIT ALONG ROADWAYS TO BE DRILLED
 - 2) CONDUIT BEING PLACED TO SIDES OF HOMES TO BE PLOWED TO D MARK & COILED AT SIDE OF HOME. JET DROPS TO BE PLACED IN DUCTS
 - 3) ALL PITS TO BE VACCED
 - 4) WHEN REPLACING PEDESTALS ENSURE PED IS BELL OWNED AS CABLE PEDESTALS ARE BROWN ALSO
 - 5) REPLACE EXISTING COIL/DROP IN PEDESTALS
 - 6) AT ANY LOCATION WHERE A DROP WIRE GOES DIRECTLY TO THE HOUSE THE CUSTOMER MUST BE ASKED IF THEY WOULD LIKE THE FIBRE RUN TO THEIR HOME AT NO COST REGARDLESS IF THEY GET THE SERVICE OR NOT. IF THE CUSTOMER DOES NOT WANT THE DROP RUN TO THEIR HOME A FLOWER POT WILL BE PLACED ON THE PROPERTY LINE AND THE DROP WILL BE COILED INSIDE FOR FUTURE SERVICE
 - 7) SEE PLAN 710 & 711 FOR DUCT CONNECTION DETAILS

WARNING - RESIDENTS WARNED OF IMPROPER GAS LINE PLACEMENT & DAMAGE IN THE PAST PLEASE TAKE EXTRA CARE

ISSUE DATE	REISSUE DATE	ASSOCIATE / PHONE CAG/MATT KNIGHT / 705-624-2396	SIGNATURE
ENGINEERING: This plan represents a Letter of Instruction. The work will be completed according to cost/requirements established in BCH-Vendor contracts and conform to schedules determined by the individual BCH Companies.	R/W N/A	ORIGINATOR / PHONE IM/CHUCK COOPER / 705-788-4320	
CLLI GRVNON31	SC GRAVENHURST	NETWORK# S47411	PLAN 614

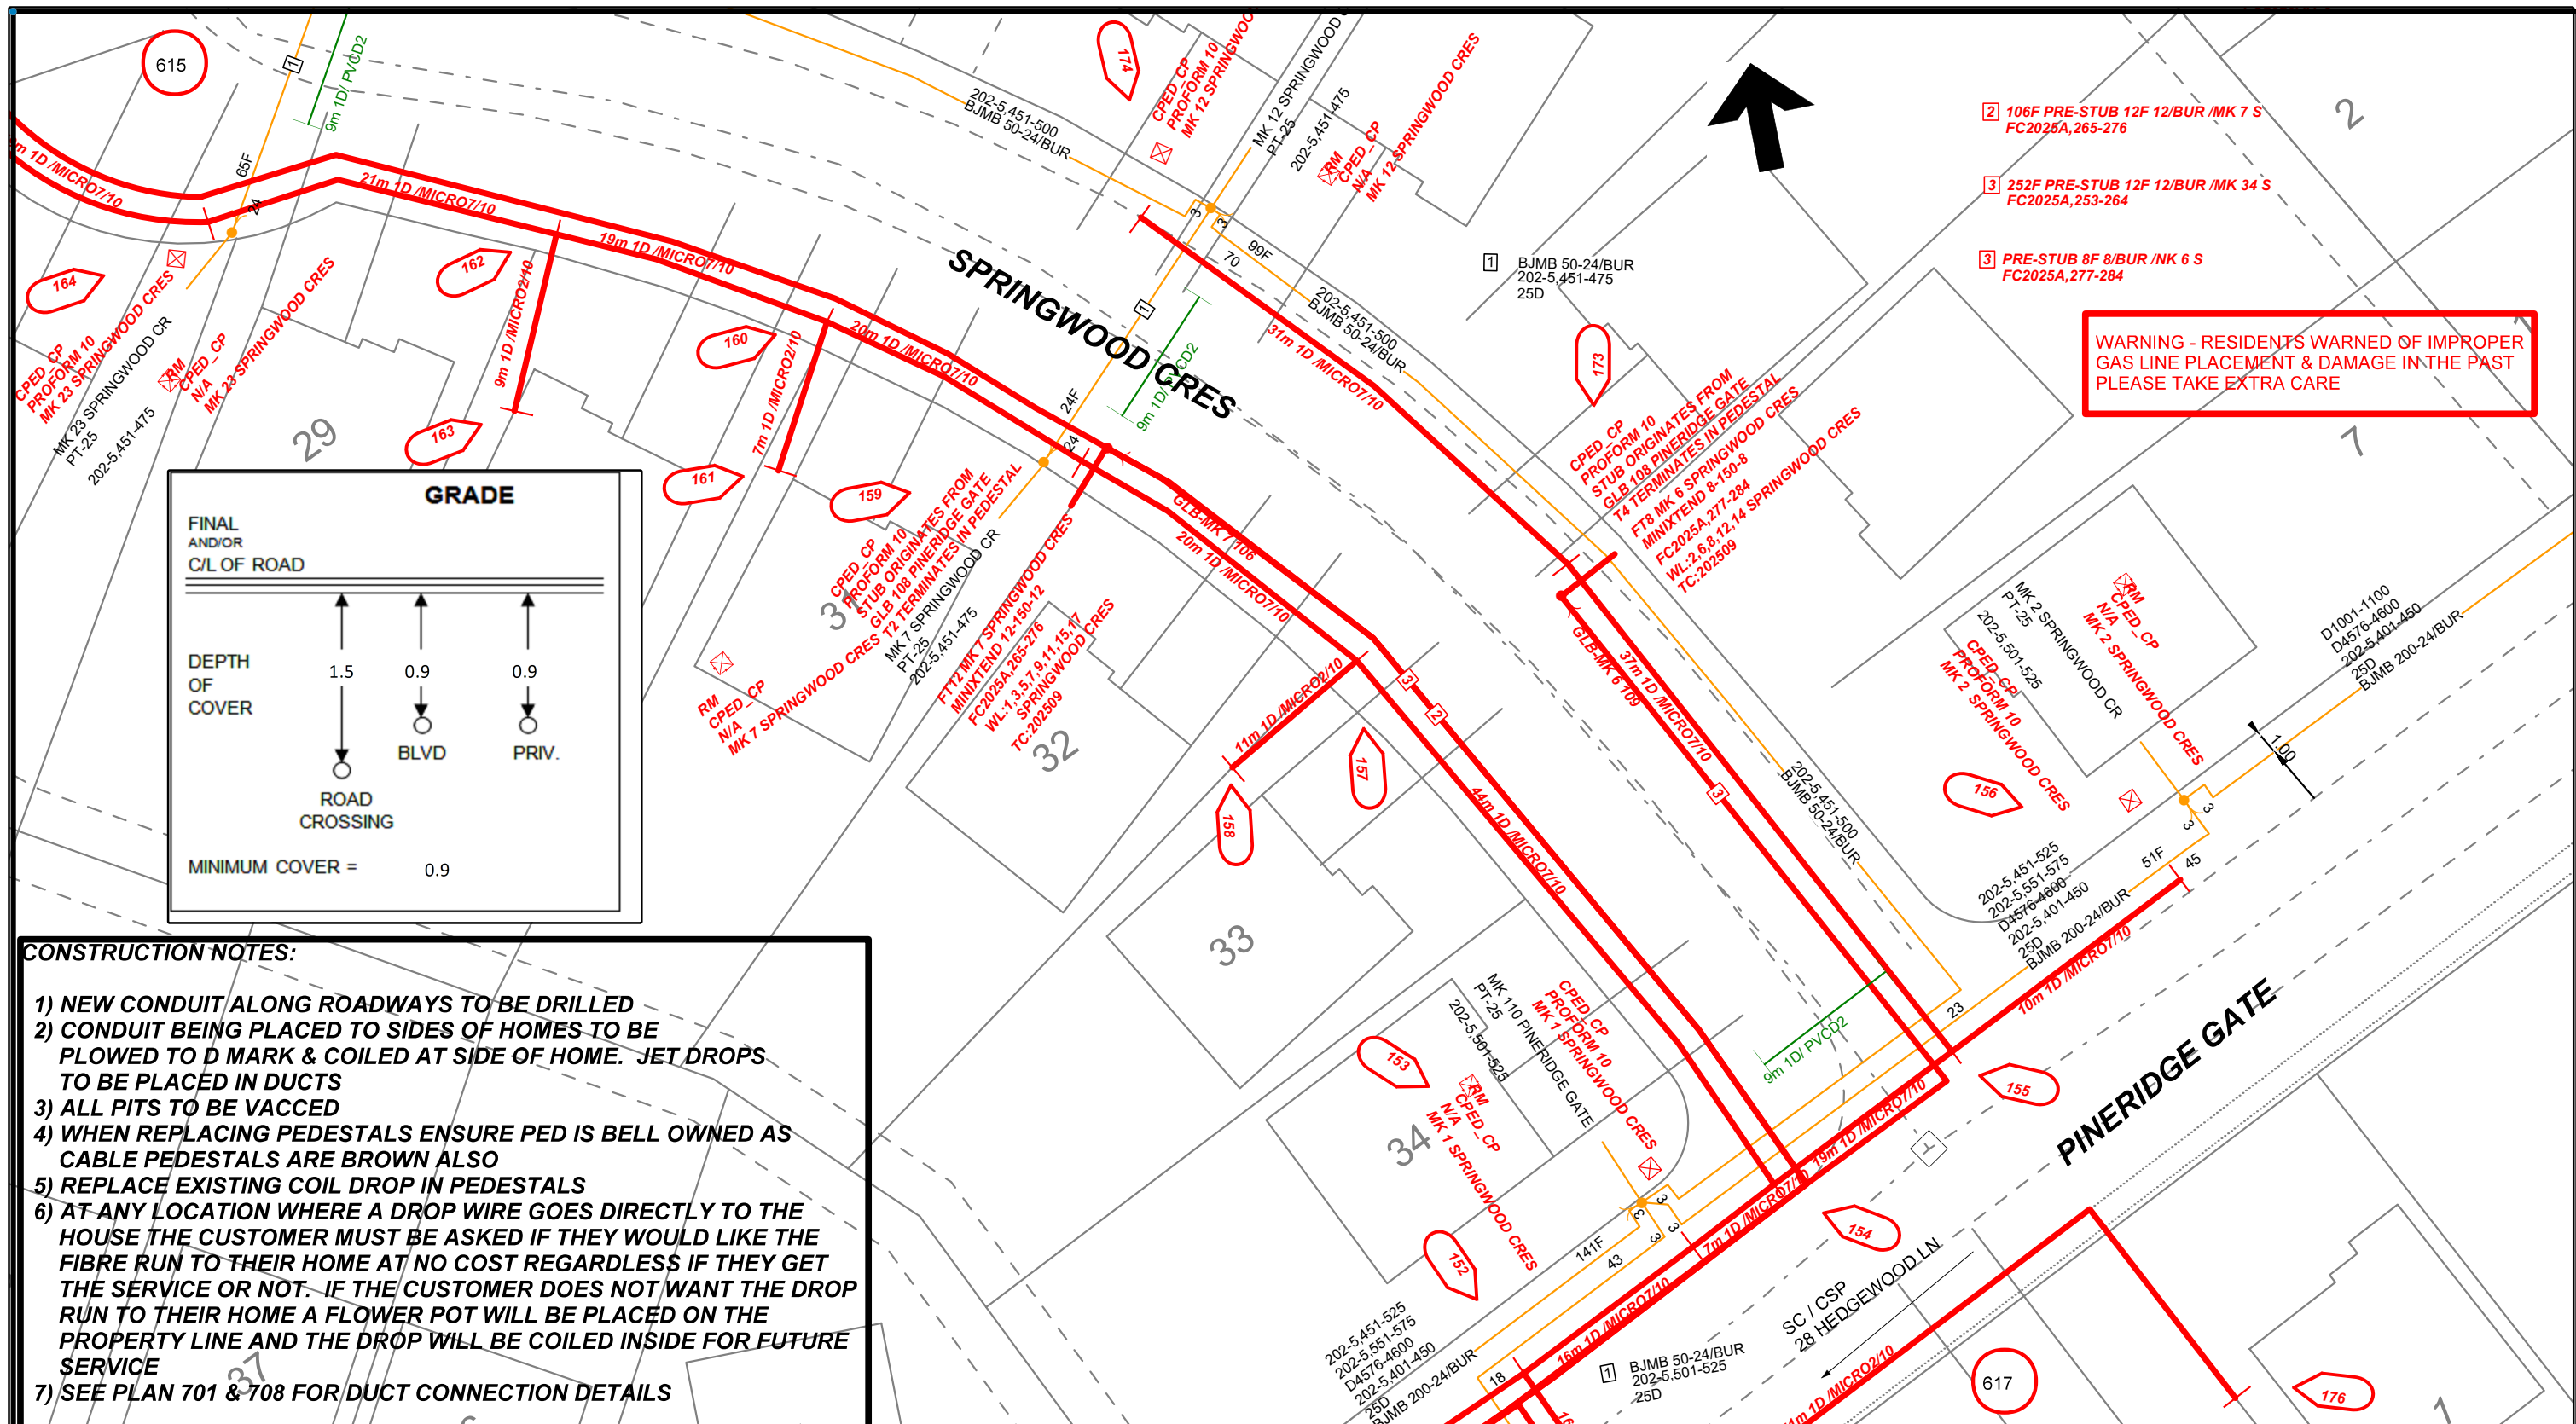


GRADE		
FINAL AND/OR C/L OF ROAD		
1.5	0.9	0.9
DEPTH OF COVER	BLVD	PRIV.
ROAD CROSSING		
MINIMUM COVER = 0.9		

- CONSTRUCTION NOTES:**
- 1) NEW CONDUIT ALONG ROADWAYS TO BE DRILLED
 - 2) CONDUIT BEING PLACED TO SIDES OF HOMES TO BE PLOWED TO D MARK & COILED AT SIDE OF HOME. JET DROPS TO BE PLACED IN DUCTS
 - 3) ALL PITS TO BE VACCED
 - 4) WHEN REPLACING PEDESTALS ENSURE PED IS BELL OWNED AS CABLE PEDESTALS ARE BROWN ALSO
 - 5) REPLACE EXISTING COIL DROP IN PEDESTALS
 - 6) AT ANY LOCATION WHERE A DROP WIRE GOES DIRECTLY TO THE HOUSE THE CUSTOMER MUST BE ASKED IF THEY WOULD LIKE THE FIBRE RUN TO THEIR HOME AT NO COST REGARDLESS IF THEY GET THE SERVICE OR NOT. IF THE CUSTOMER DOES NOT WANT THE DROP RUN TO THEIR HOME A FLOWER POT WILL BE PLACED ON THE PROPERTY LINE AND THE DROP WILL BE COILED INSIDE FOR FUTURE SERVICE
 - 7) SEE PLAN 701 & 708 FOR DUCT CONNECTION DETAILS


730

ISSUE DATE	REISSUE DATE	ASSOCIATE / PHONE CAG/MATT KNIGHT / 705-624-2396	SIGNATURE
ENGINEERING: This plan represents a Letter of Instruction. The work will be completed according to cost/requirements established in BCH-Vendor contracts and conform to schedules determined by the individual BCH Companies.		R/W N/A	ORIGINATOR / PHONE IM/CHUCK COOPER / 705-788-4320
CLLI GRVNON31		SC GRAVENHURST	NETWORK# S47411
			PLAN 616

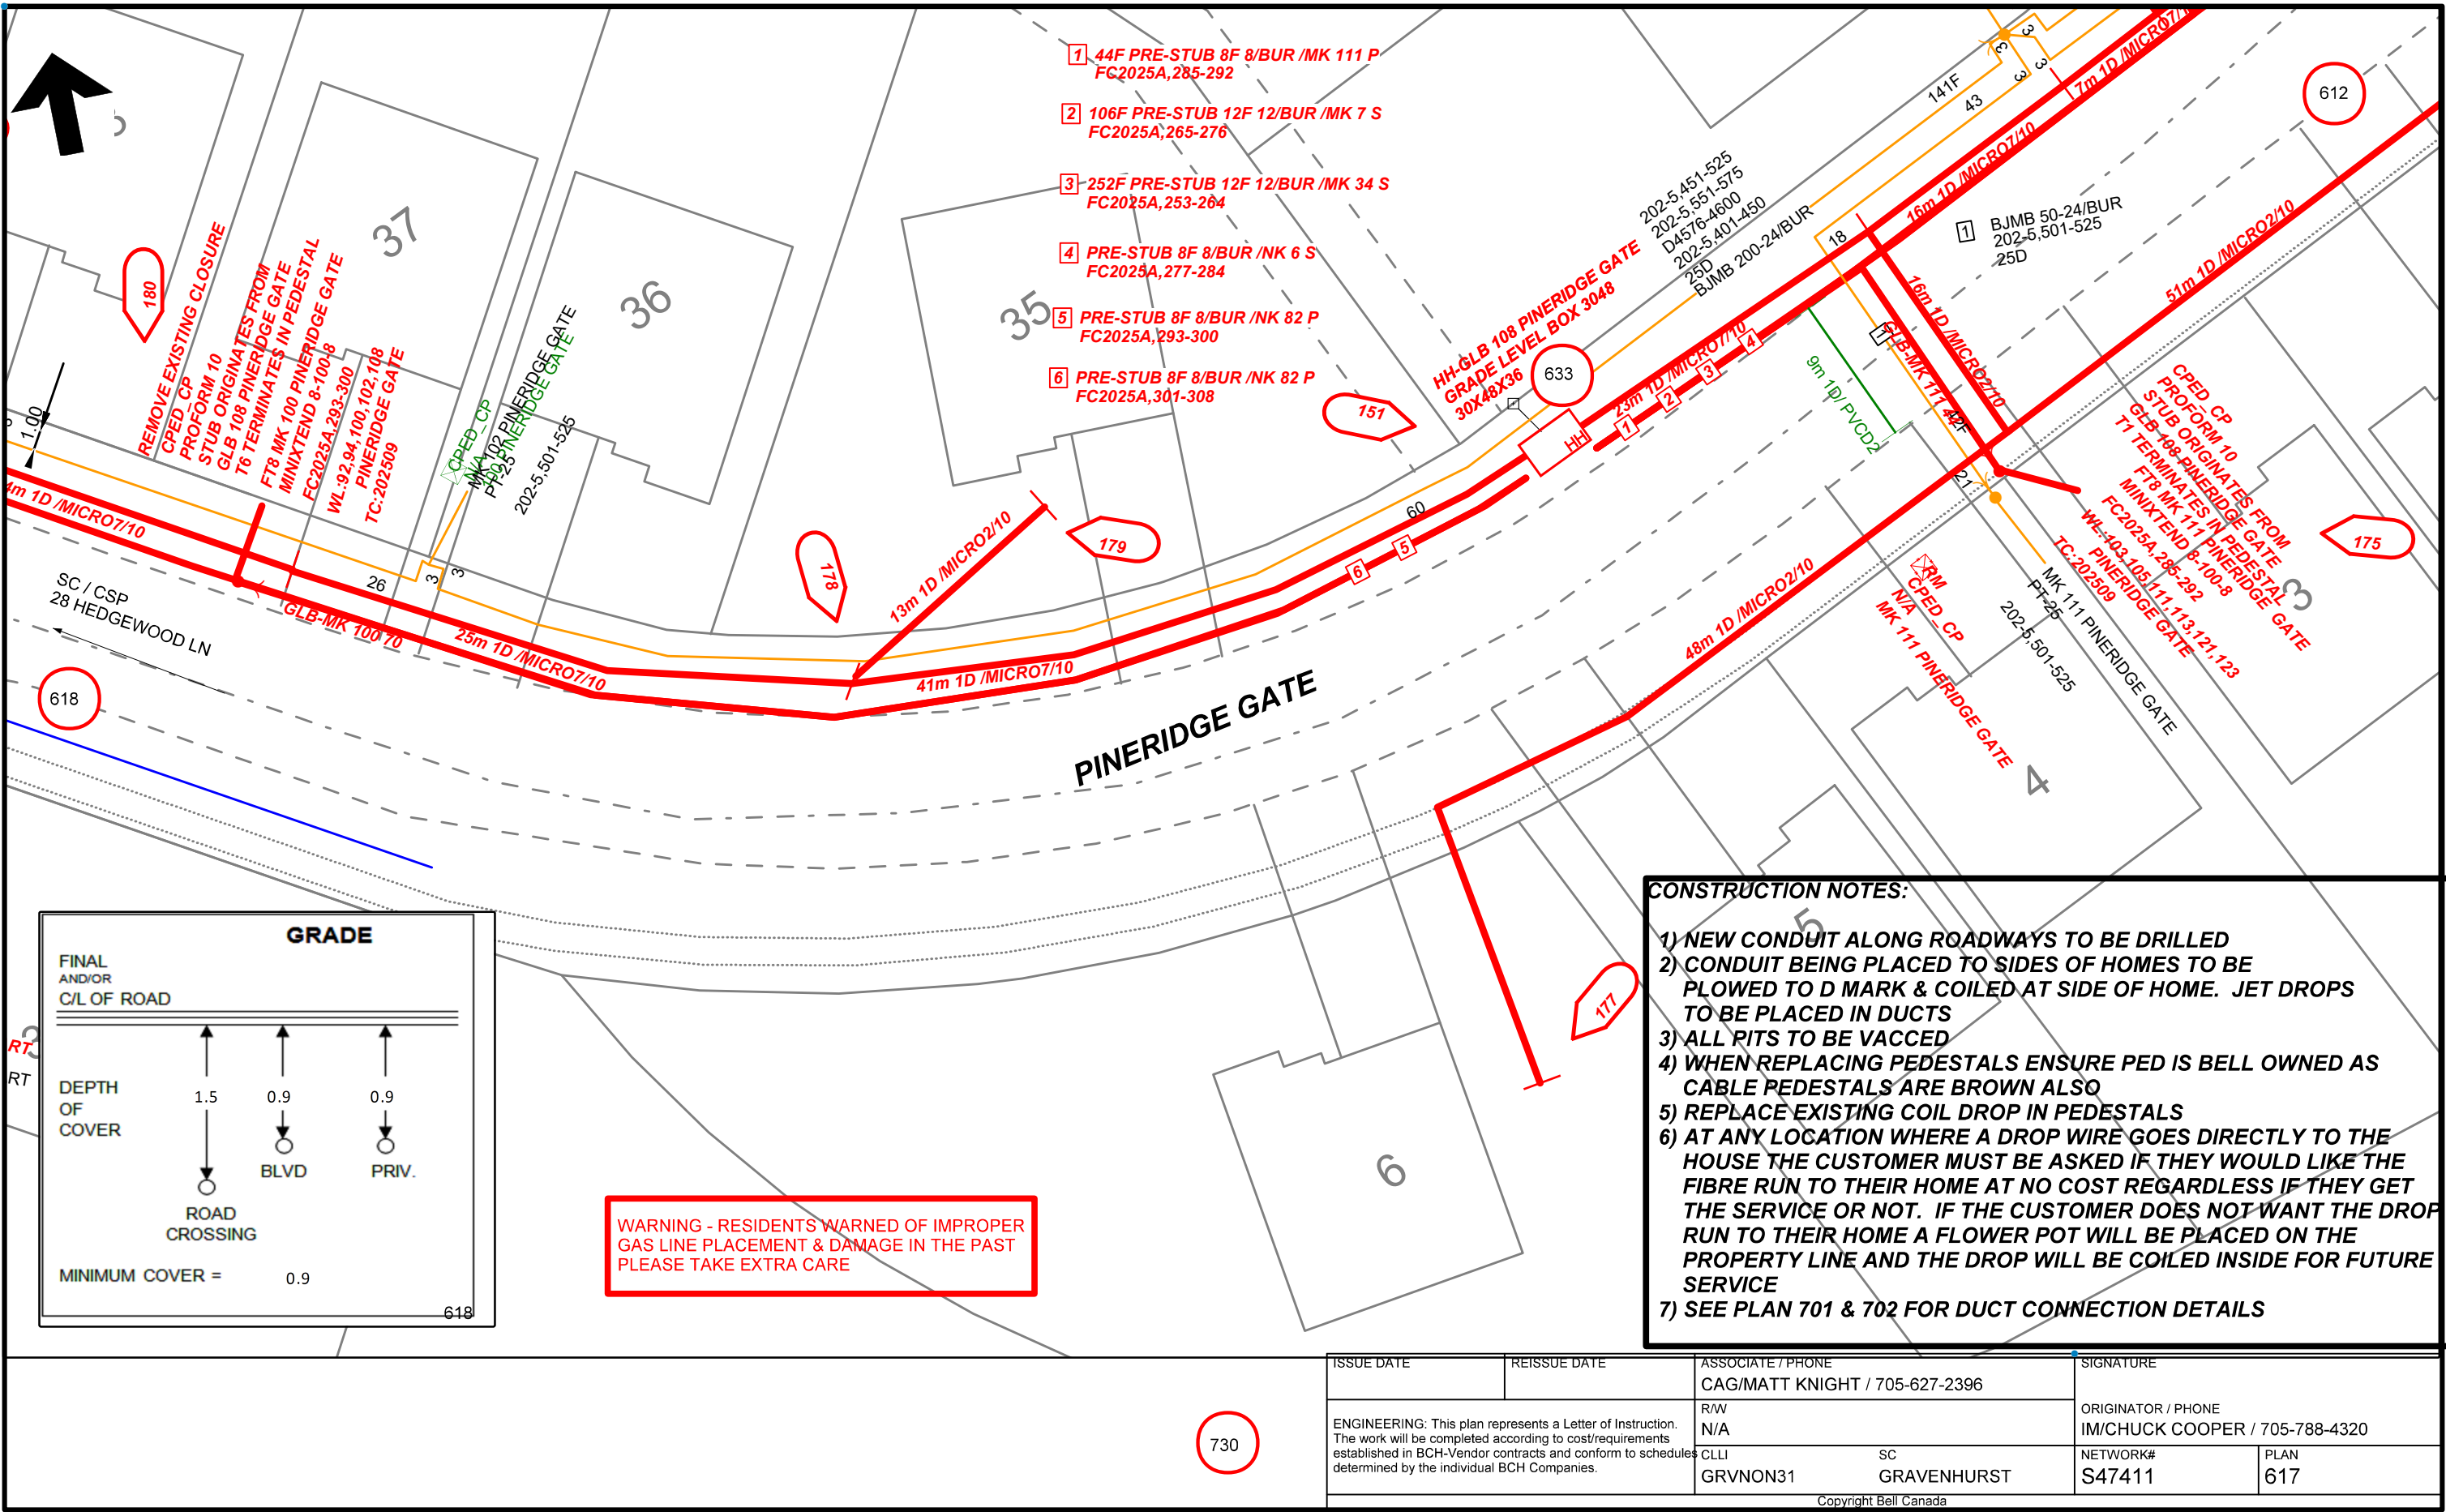

GRADE

FINAL
AND/OR
C/L OF ROAD

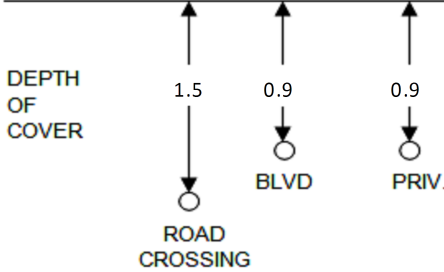


MINIMUM COVER = 0.9

WARNING - RESIDENTS WARNED OF IMPROPER
GAS LINE PLACEMENT & DAMAGE IN THE PAST
PLEASE TAKE EXTRA CARE


CONSTRUCTION NOTES:

- 1) NEW CONDUIT ALONG ROADWAYS TO BE DRILLED
- 2) CONDUIT BEING PLACED TO SIDES OF HOMES TO BE PLOWED TO D MARK & COILED AT SIDE OF HOME. JET DROPS TO BE PLACED IN DUCTS
- 3) ALL PITS TO BE VACCED
- 4) WHEN REPLACING PEDESTALS ENSURE PED IS BELL OWNED AS CABLE PEDESTALS ARE BROWN ALSO
- 5) REPLACE EXISTING COIL DROP IN PEDESTALS
- 6) AT ANY LOCATION WHERE A DROP WIRE GOES DIRECTLY TO THE HOUSE THE CUSTOMER MUST BE ASKED IF THEY WOULD LIKE THE FIBRE RUN TO THEIR HOME AT NO COST REGARDLESS IF THEY GET THE SERVICE OR NOT. IF THE CUSTOMER DOES NOT WANT THE DROP RUN TO THEIR HOME A FLOWER POT WILL BE PLACED ON THE PROPERTY LINE AND THE DROP WILL BE COILED INSIDE FOR FUTURE SERVICE
- 7) SEE PLAN 701 & 702 FOR DUCT CONNECTION DETAILS

ISSUE DATE	REISSUE DATE	ASSOCIATE / PHONE CAG/MATT KNIGHT / 705-627-2396	SIGNATURE
ENGINEERING: This plan represents a Letter of Instruction. The work will be completed according to cost/requirements established in BCH-Vendor contracts and conform to schedules determined by the individual BCH Companies.		R/W N/A	ORIGINATOR / PHONE IM/CHUCK COOPER / 705-788-4320
CLLI GRVNON31	SC GRAVENHURST	NETWORK# S47411	PLAN 617

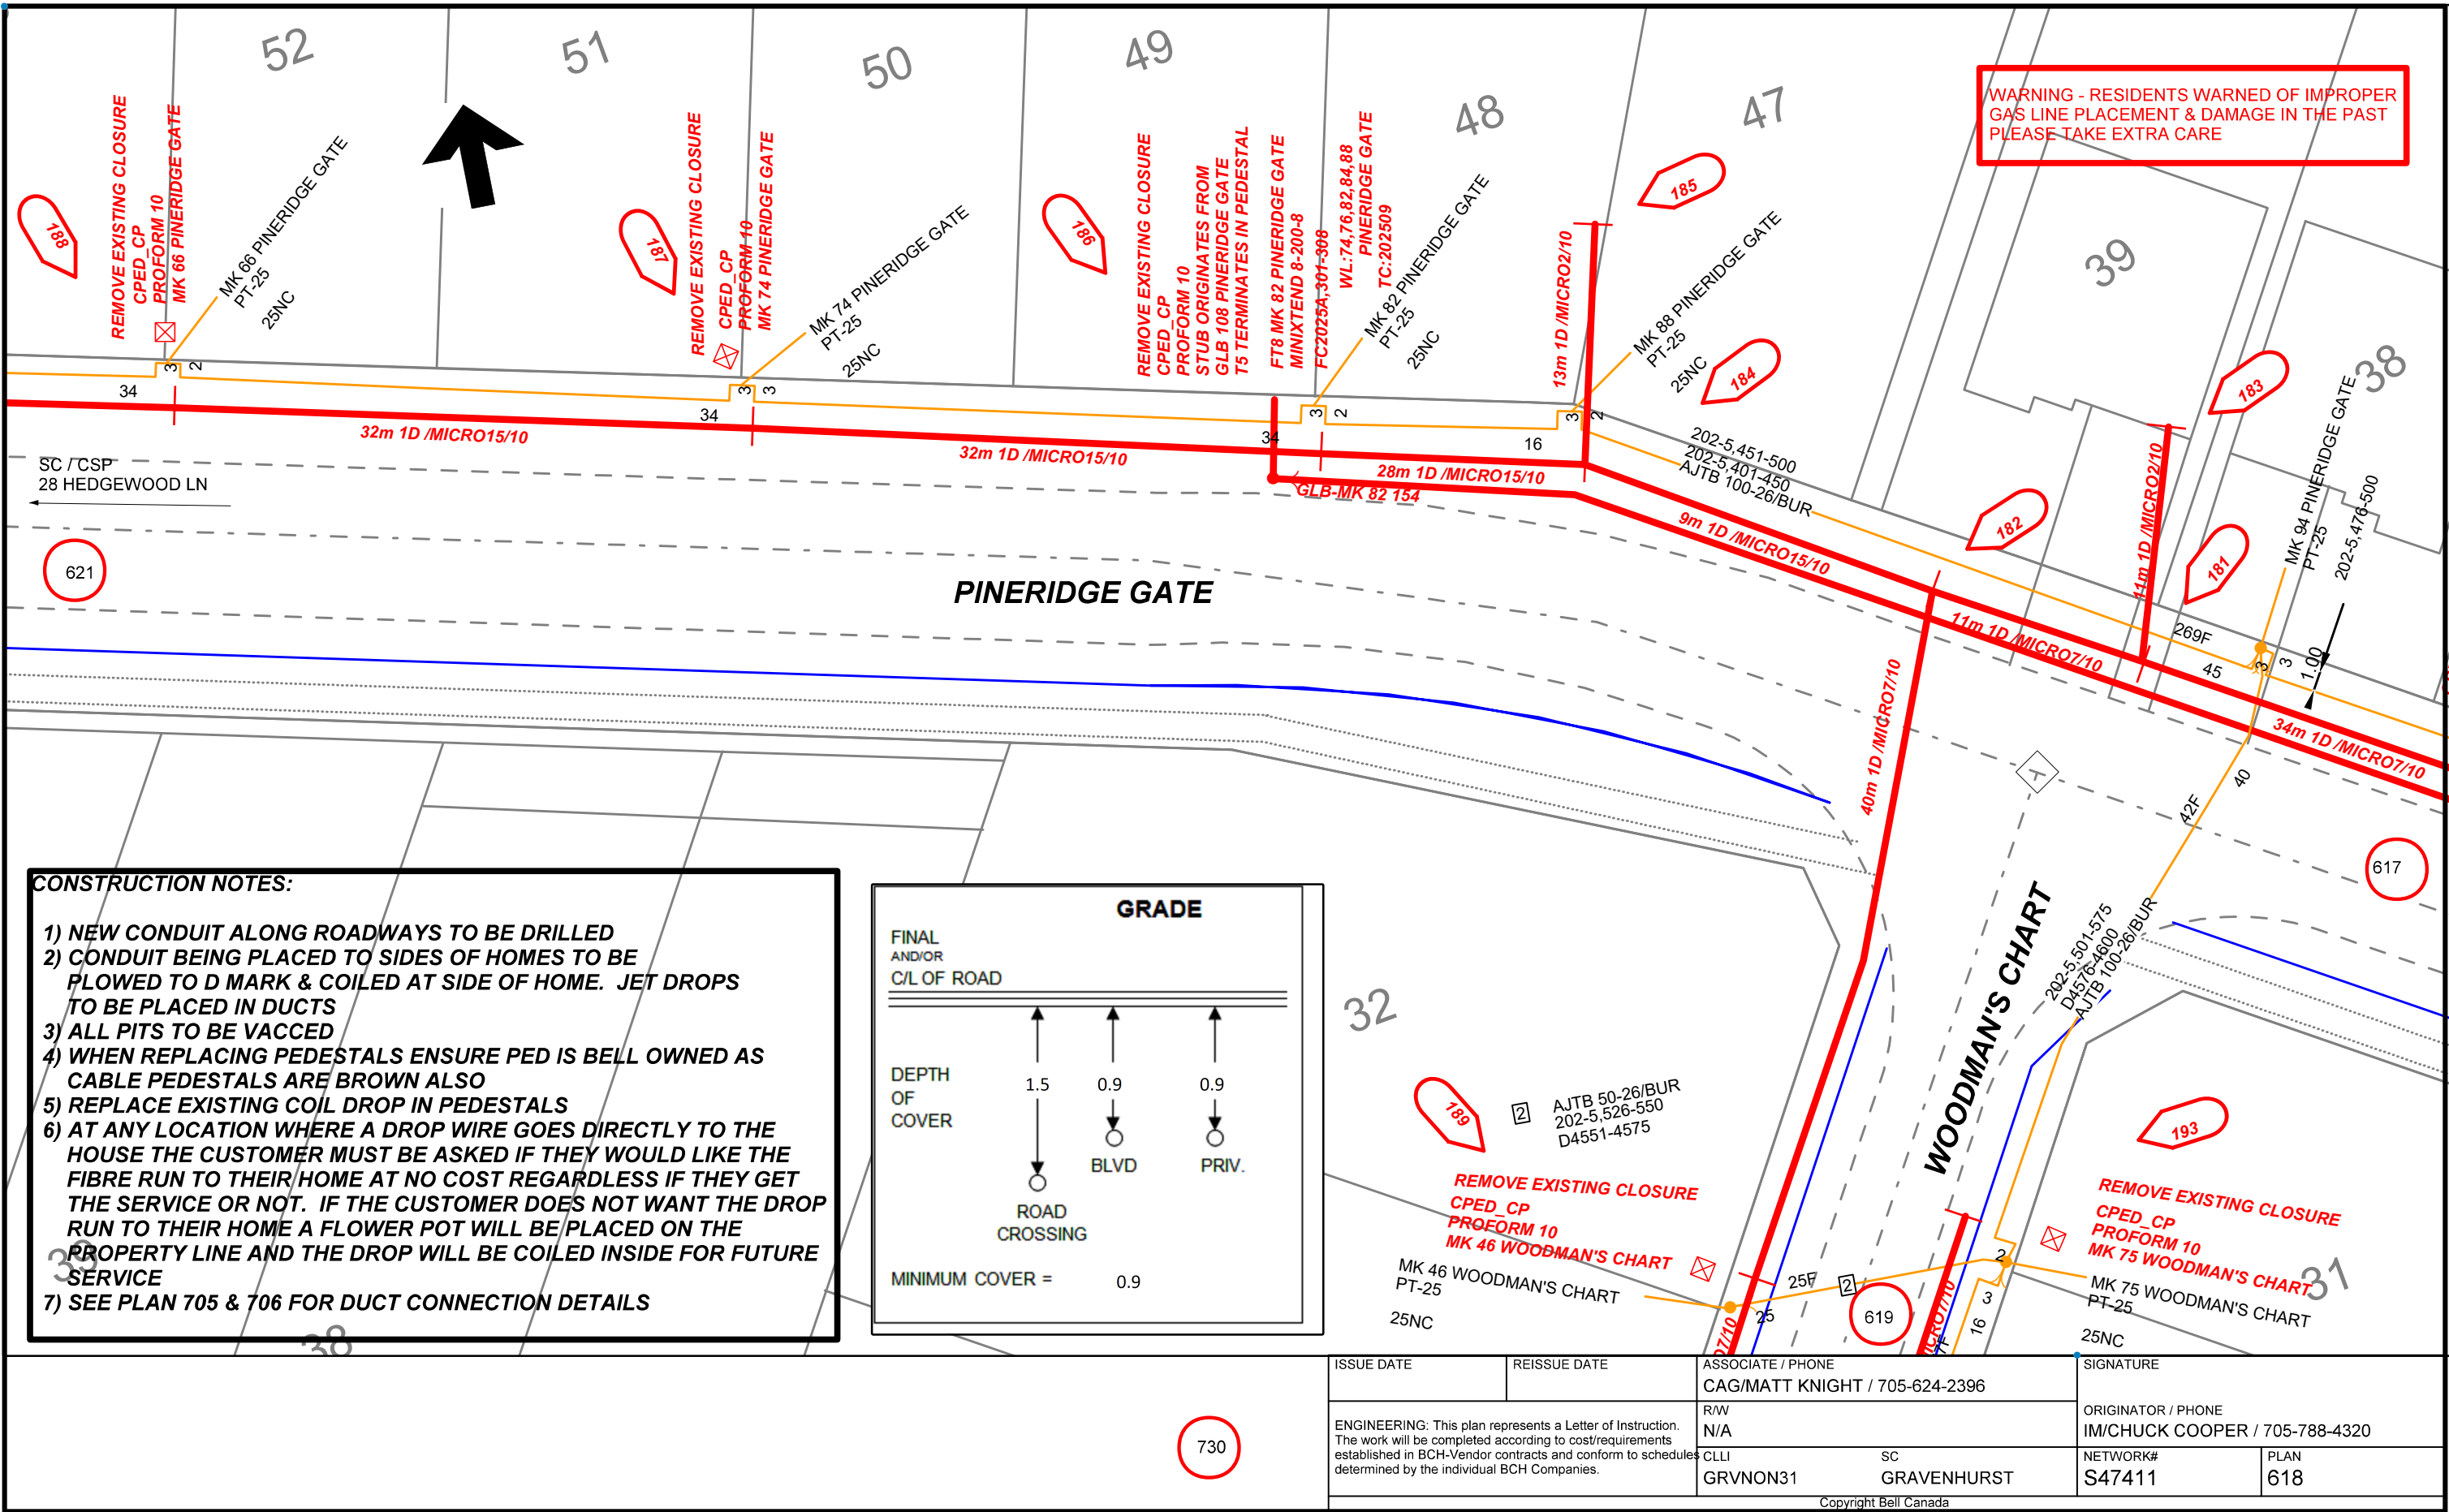


- CONSTRUCTION NOTES:**
- 1) NEW CONDUIT ALONG ROADWAYS TO BE DRILLED
 - 2) CONDUIT BEING PLACED TO SIDES OF HOMES TO BE PLOWED TO D MARK & COILED AT SIDE OF HOME. JET DROPS TO BE PLACED IN DUCTS
 - 3) ALL PITS TO BE VACCD
 - 4) WHEN REPLACING PEDESTALS ENSURE PED IS BELL OWNED AS CABLE PEDESTALS ARE BROWN ALSO
 - 5) REPLACE EXISTING COIL DROP IN PEDESTALS
 - 6) AT ANY LOCATION WHERE A DROP WIRE GOES DIRECTLY TO THE HOUSE THE CUSTOMER MUST BE ASKED IF THEY WOULD LIKE THE FIBRE RUN TO THEIR HOME AT NO COST REGARDLESS IF THEY GET THE SERVICE OR NOT. IF THE CUSTOMER DOES NOT WANT THE DROP RUN TO THEIR HOME A FLOWER POT WILL BE PLACED ON THE PROPERTY LINE AND THE DROP WILL BE COILED INSIDE FOR FUTURE SERVICE
 - 7) SEE PLAN 705 & 706 FOR DUCT CONNECTION DETAILS

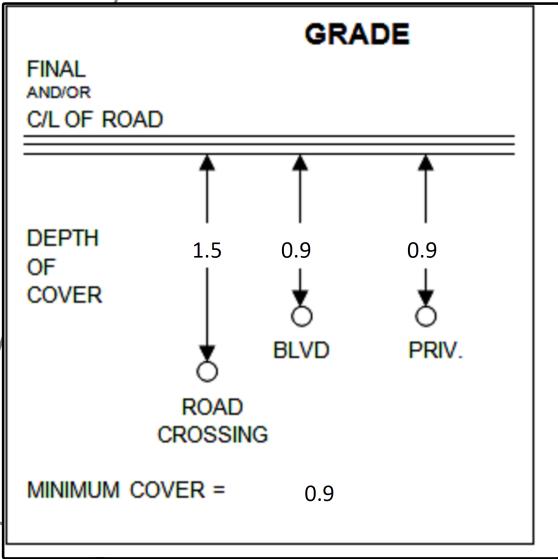

ISSUE DATE	REISSUE DATE	ASSOCIATE / PHONE CAG/MATT KNIGHT / 705-624-2396	SIGNATURE
ENGINEERING: This plan represents a Letter of Instruction. The work will be completed according to cost/requirements established in BCH-Vendor contracts and conform to schedules determined by the individual BCH Companies.		R/W N/A	ORIGINATOR / PHONE IM/CHUCK COOPER / 705-788-4320
CLLI GRVNON31	SC GRAVENHURST	NETWORK# S47411	PLAN 618

**WARNING - RESIDENTS WARNED OF IMPROPER
GAS LINE PLACEMENT & DAMAGE IN THE PAST
PLEASE TAKE EXTRA CARE**

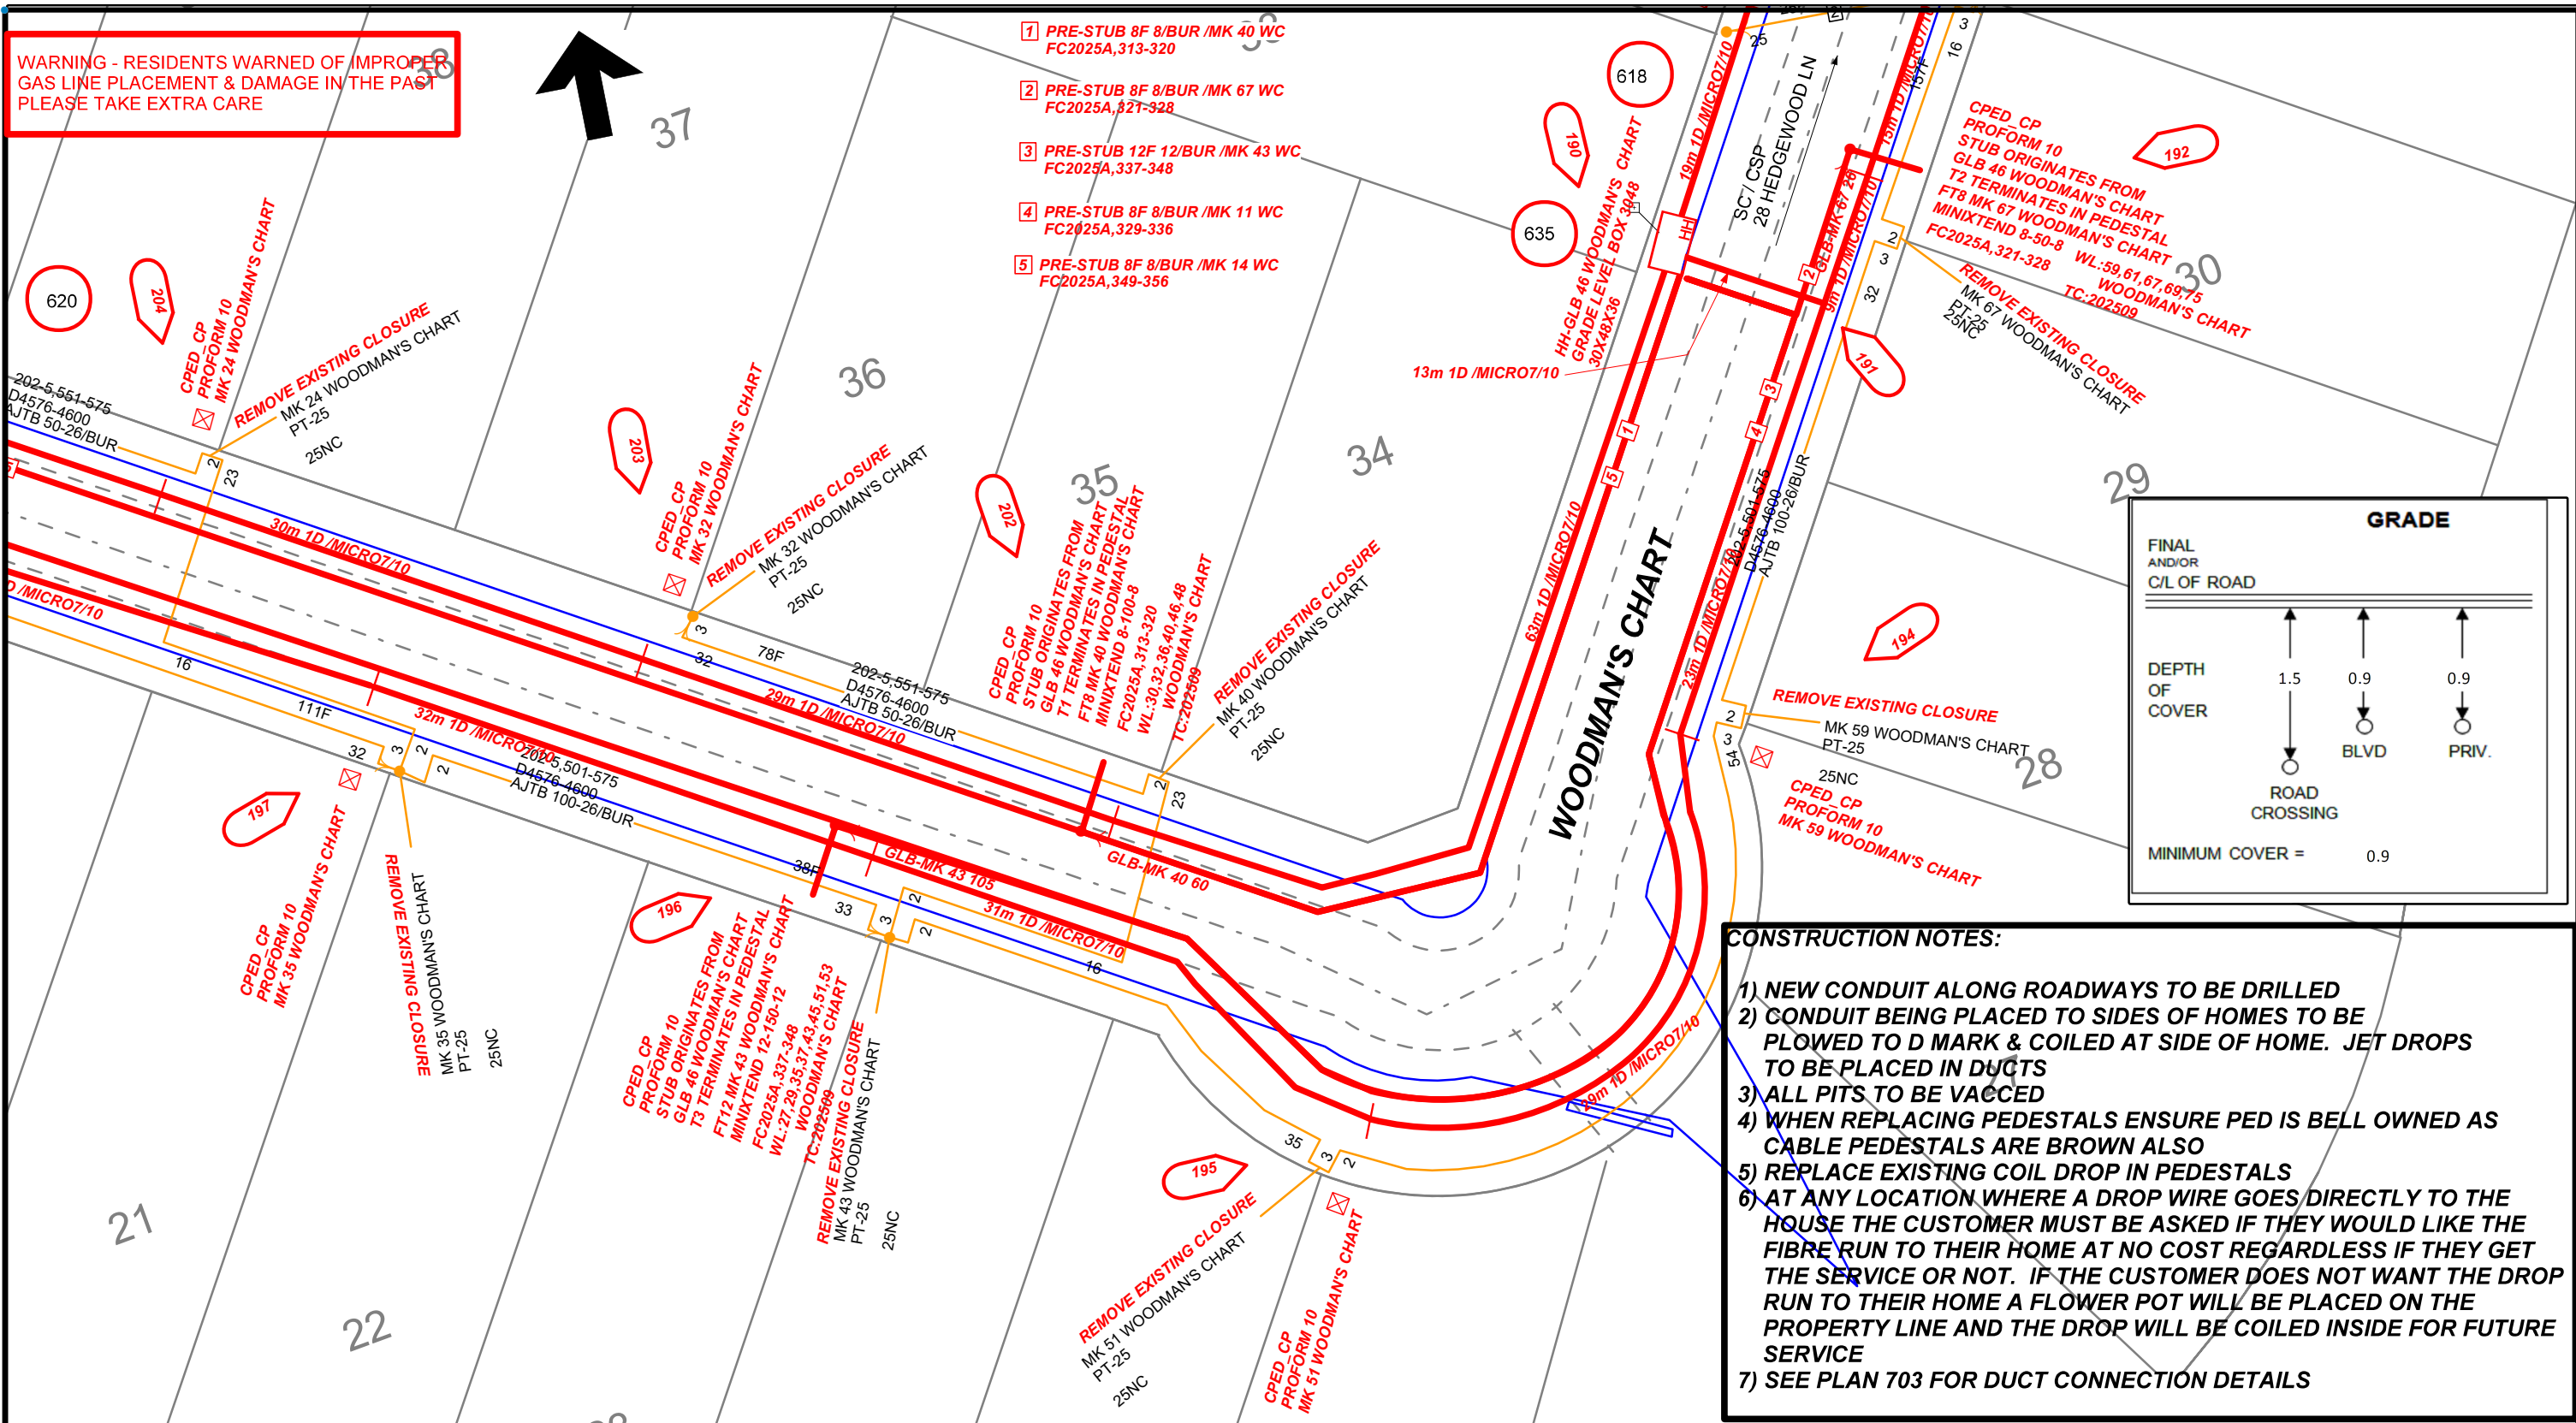


ISSUE DATE	REISSUE DATE	ASSOCIATE / PHONE CAG/MATT KNIGHT / 705-624-2396		SIGNATURE	
ENGINEERING: This plan represents a Letter of Instruction. The work will be completed according to cost/requirements established in BCH-Vendor contracts and conform to schedules determined by the individual BCH Companies.		R/W N/A		ORIGINATOR / PHONE IM/CHUCK COOPER / 705-788-4320	
		CLLI GRVNON31	SC GRAVENHURST	NETWORK# S47411	PLAN 619
Copyright Bell Canada					






- 730

Copyright Bell Canada

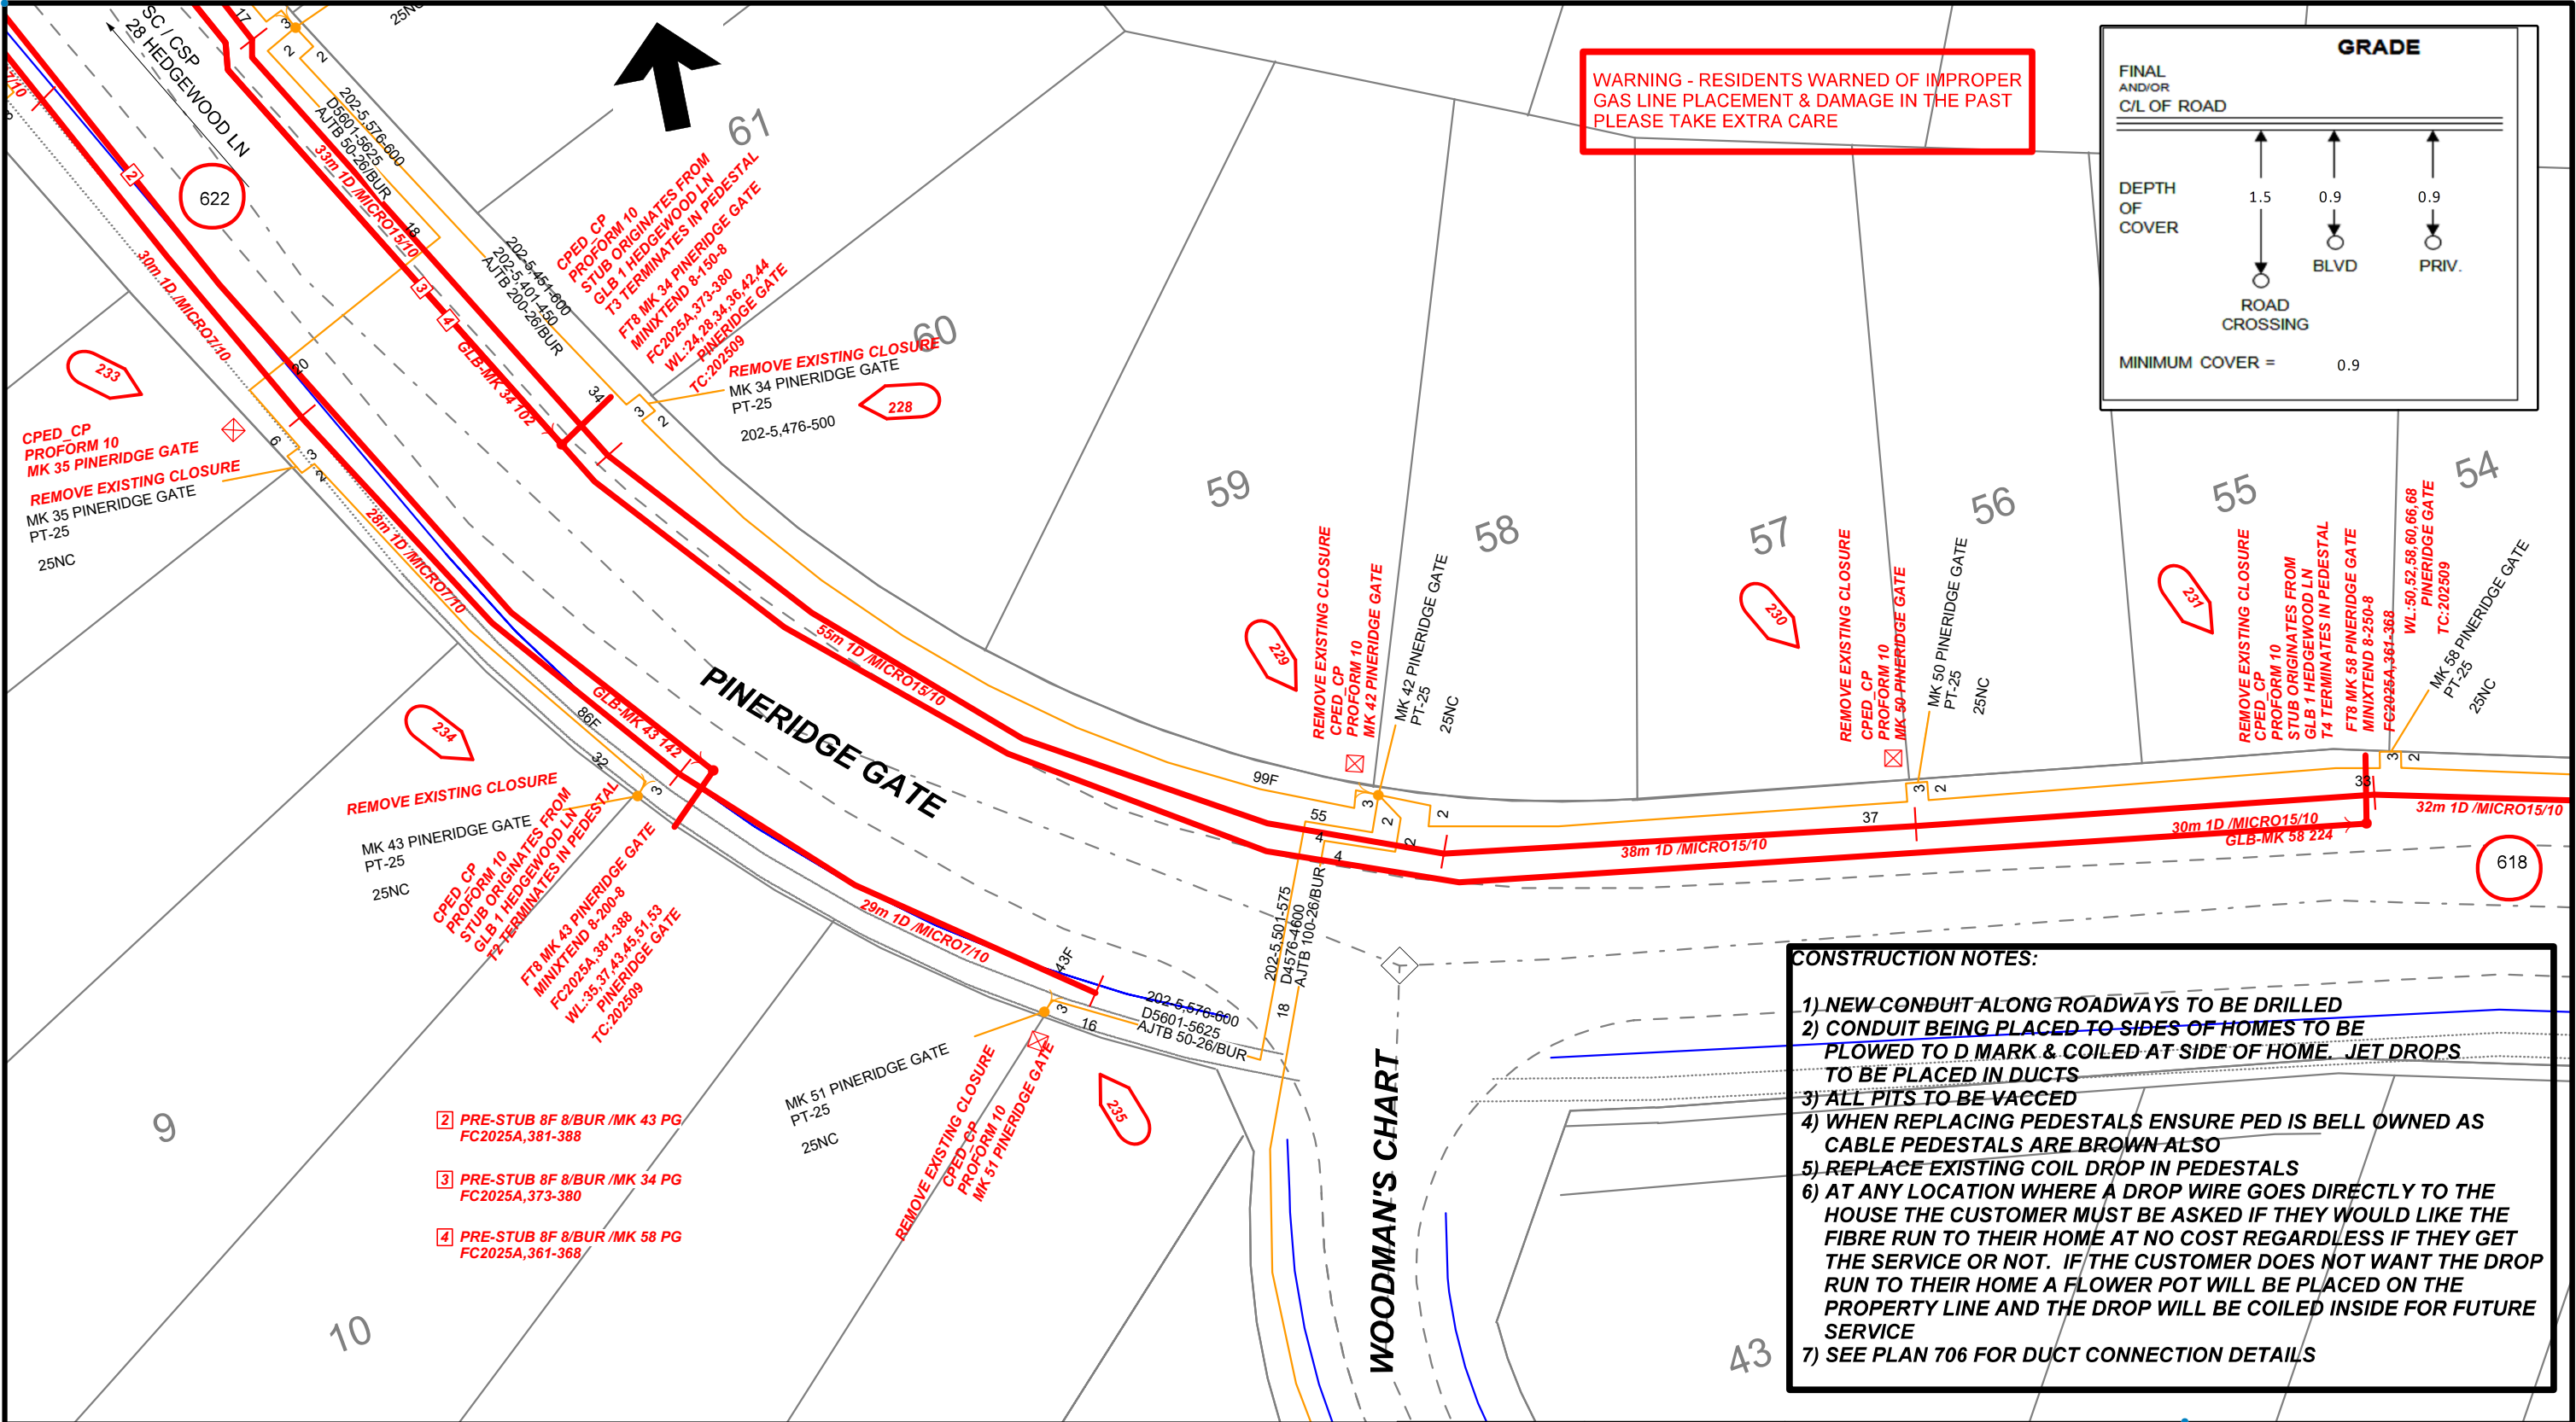

730		ISSUE DATE	REISSUE DATE	ASSOCIATE / PHONE CAG/MATT KNIGHT / 705-624-2396	SIGNATURE
		ENGINEERING: This plan represents a Letter of Instruction. The work will be completed according to cost/requirements established in BCH-Vendor contracts and conform to schedules determined by the individual BCH Companies.		R/W N/A	ORIGINATOR / PHONE IM/CHUCK COOPER / 705-788-4320
		CLLI GRVNON31	SC GRAVENHURST	NETWORK# S47411	PLAN 621

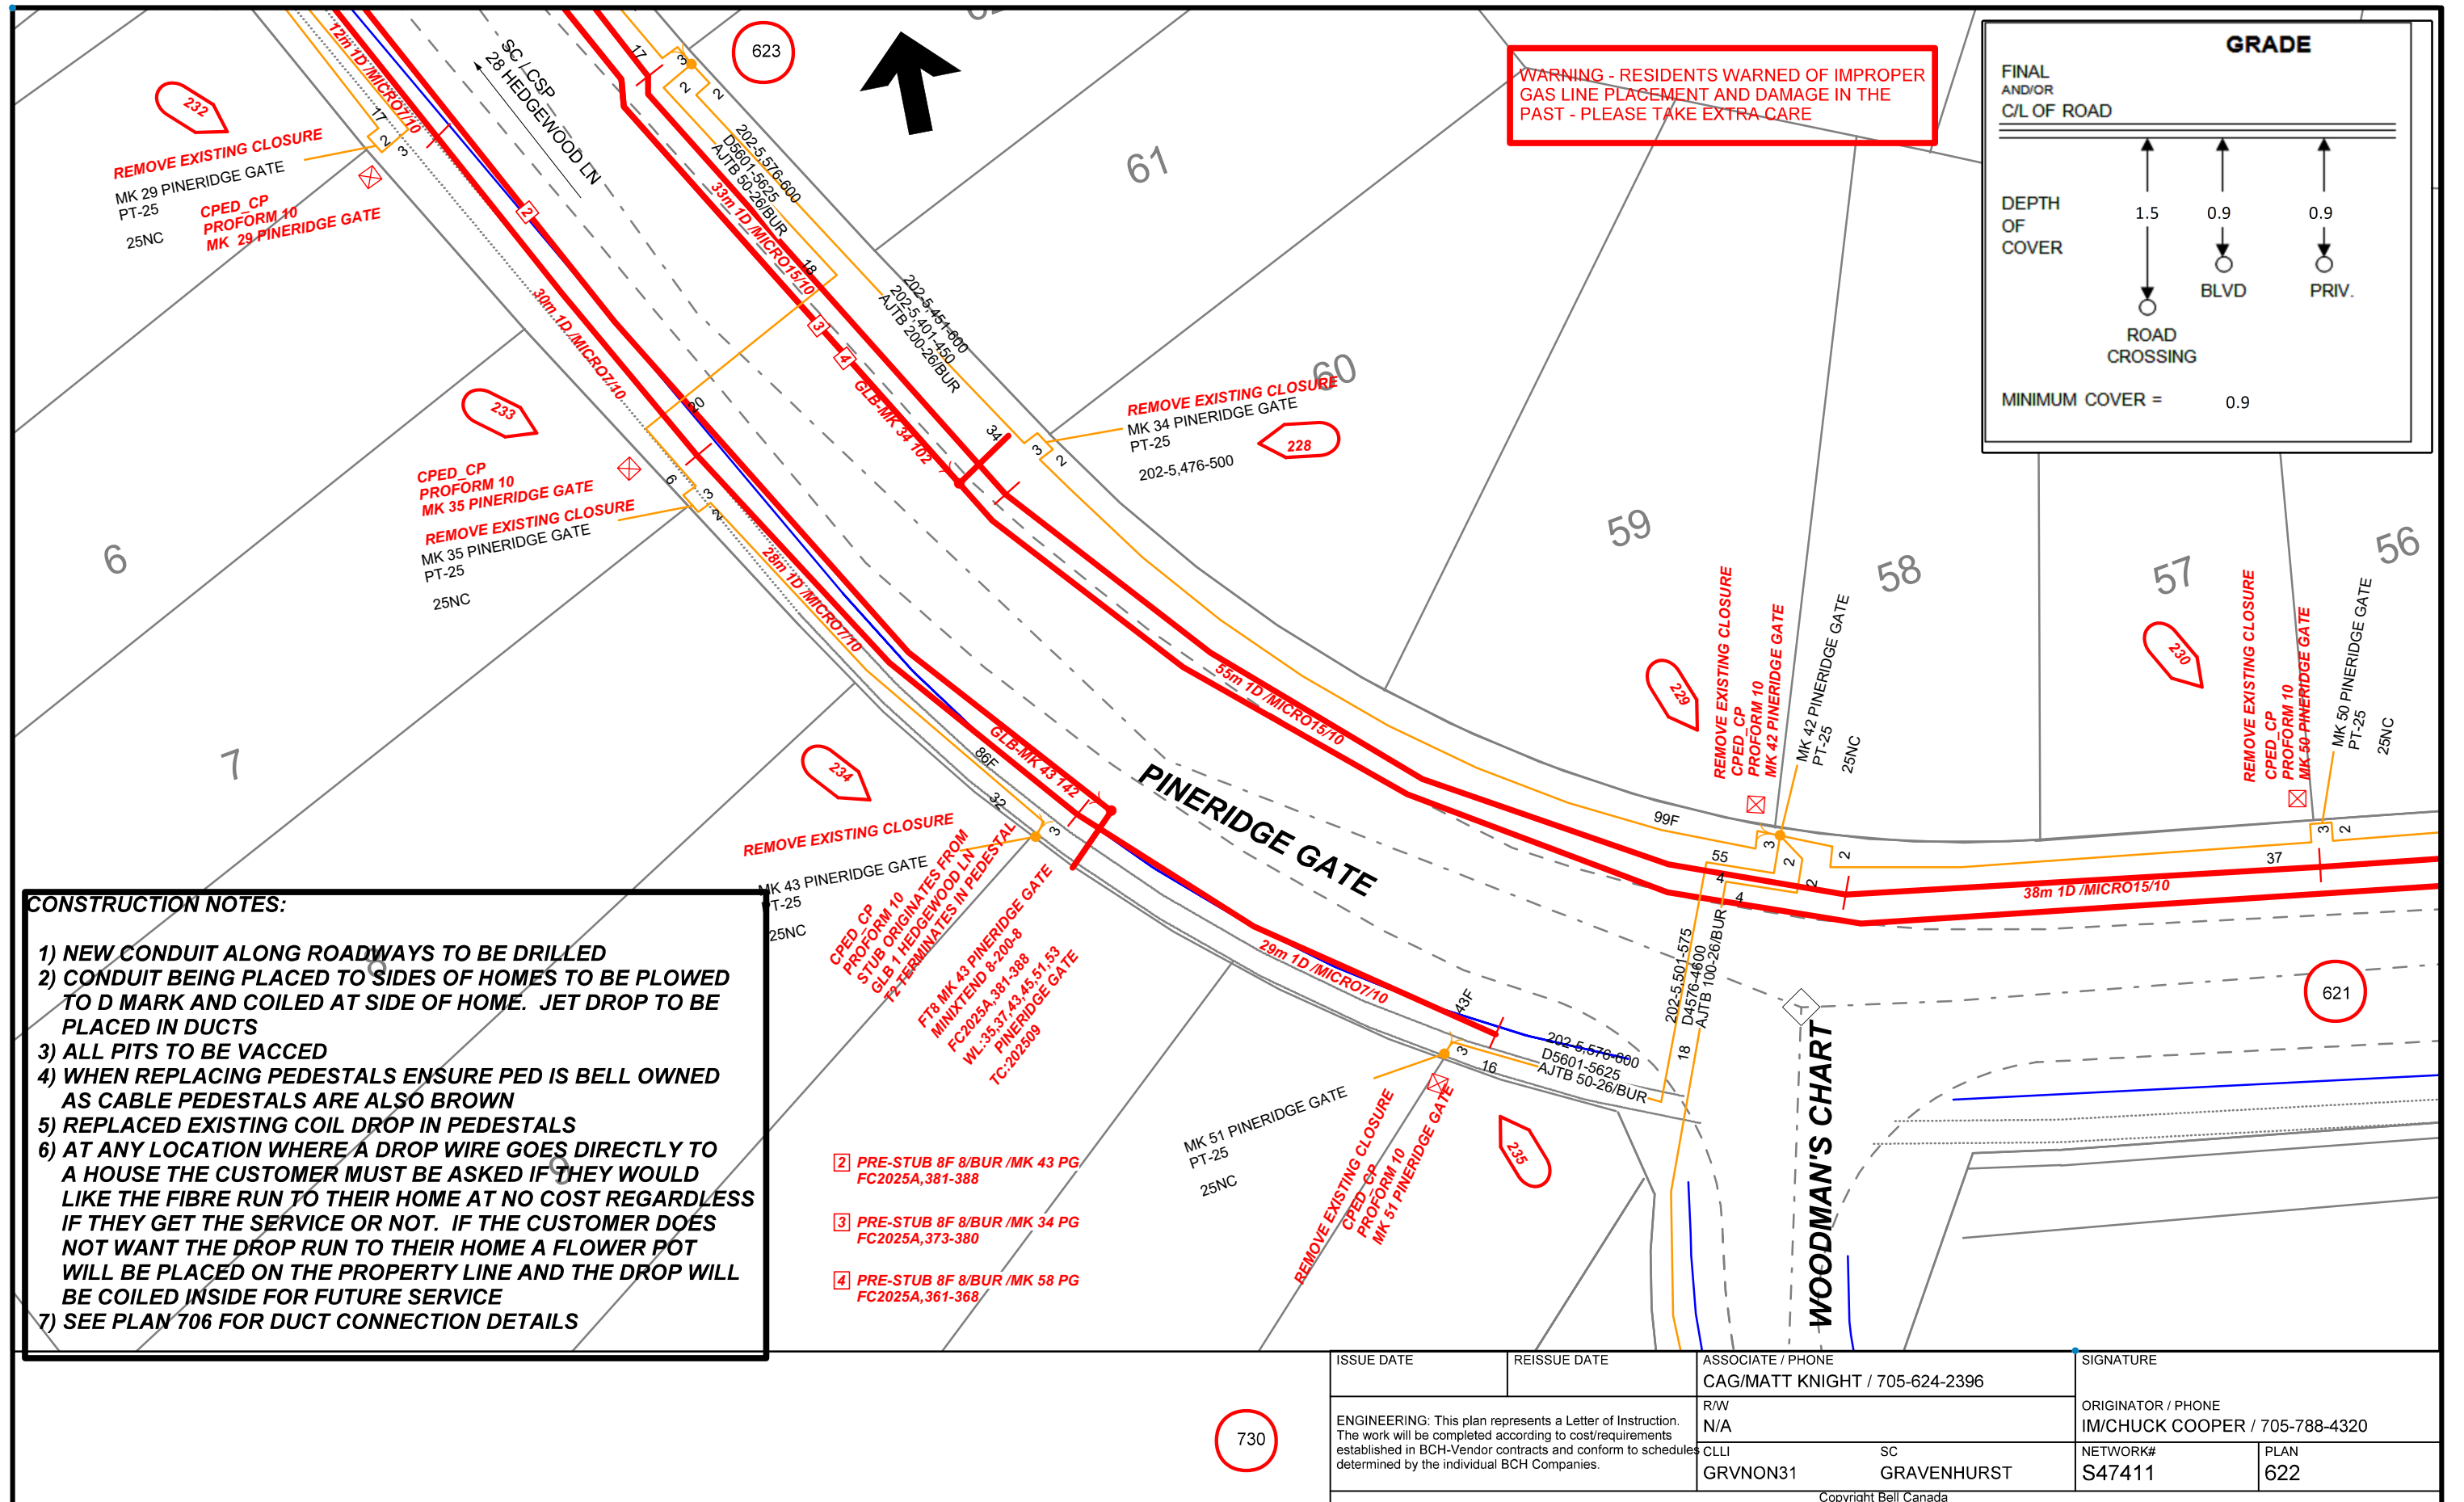

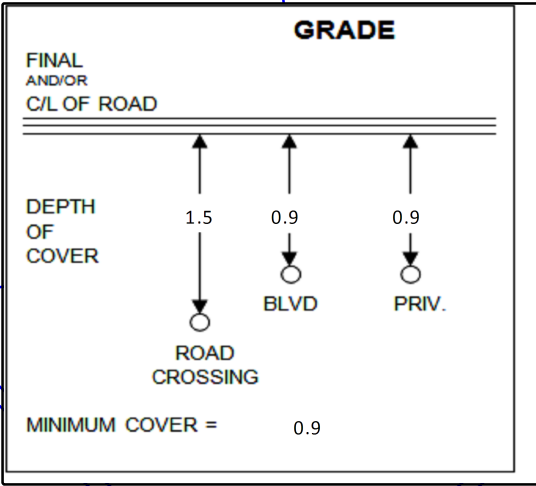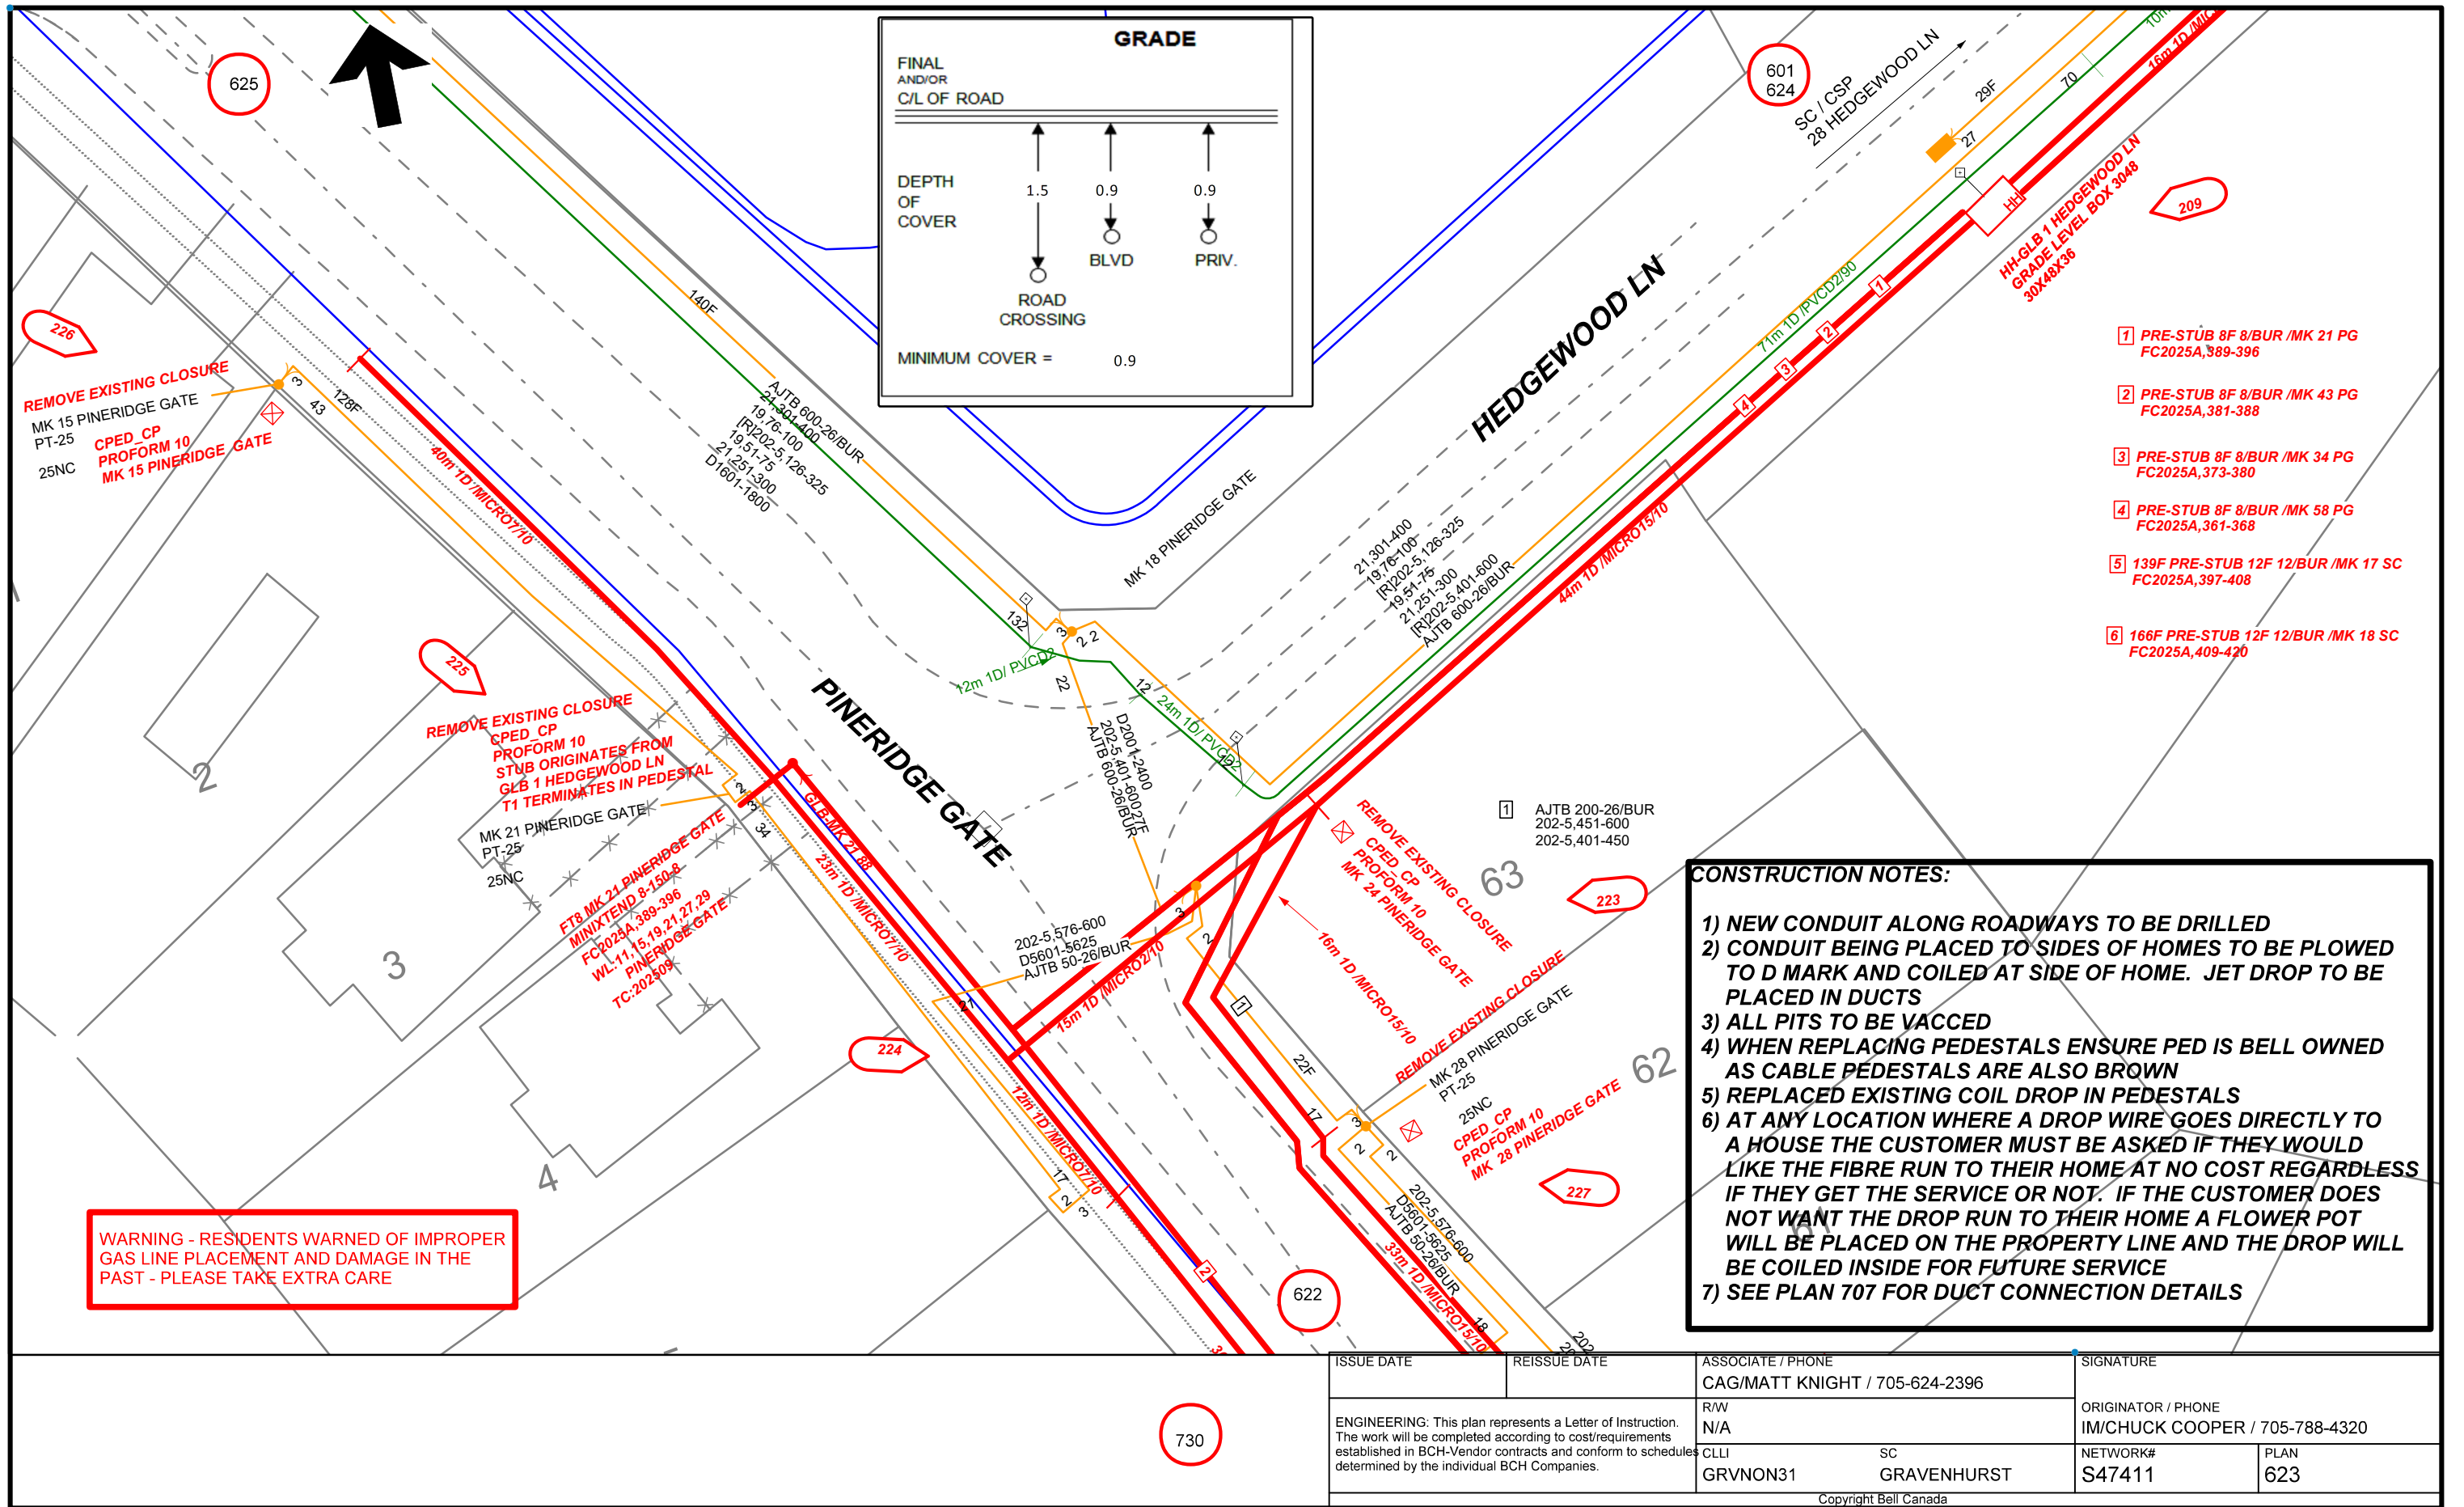


- 1 PRE-STUB 8F 8/BUR /MK 21 PG FC2025A,389-396
- 2 PRE-STUB 8F 8/BUR /MK 43 PG FC2025A,381-388
- 3 PRE-STUB 8F 8/BUR /MK 34 PG FC2025A,373-380
- 4 PRE-STUB 8F 8/BUR /MK 58 PG FC2025A,361-368
- 5 139F PRE-STUB 12F 12/BUR /MK 17 SC FC2025A,397-408
- 6 166F PRE-STUB 12F 12/BUR /MK 18 SC FC2025A,409-420

CONSTRUCTION NOTES:

- 1) NEW CONDUIT ALONG ROADWAYS TO BE DRILLED
- 2) CONDUIT BEING PLACED TO SIDES OF HOMES TO BE PLOWED TO D MARK AND COILED AT SIDE OF HOME. JET DROP TO BE PLACED IN DUCTS
- 3) ALL PITS TO BE VACCED
- 4) WHEN REPLACING PEDESTALS ENSURE PED IS BELL OWNED AS CABLE PEDESTALS ARE ALSO BROWN
- 5) REPLACED EXISTING COIL DROP IN PEDESTALS
- 6) AT ANY LOCATION WHERE A DROP WIRE GOES DIRECTLY TO A HOUSE THE CUSTOMER MUST BE ASKED IF THEY WOULD LIKE THE FIBRE RUN TO THEIR HOME AT NO COST REGARDLESS IF THEY GET THE SERVICE OR NOT. IF THE CUSTOMER DOES NOT WANT THE DROP RUN TO THEIR HOME A FLOWER POT WILL BE PLACED ON THE PROPERTY LINE AND THE DROP WILL BE COILED INSIDE FOR FUTURE SERVICE
- 7) SEE PLAN 707 FOR DUCT CONNECTION DETAILS


WARNING - RESIDENTS WARNED OF IMPROPER GAS LINE PLACEMENT AND DAMAGE IN THE PAST - PLEASE TAKE EXTRA CARE

ISSUE DATE	REISSUE DATE	ASSOCIATE / PHONE CAG/MATT KNIGHT / 705-624-2396	SIGNATURE
ENGINEERING: This plan represents a Letter of Instruction. The work will be completed according to cost/requirements established in BCH-Vendor contracts and conform to schedules determined by the individual BCH Companies.		R/W N/A	ORIGINATOR / PHONE IM/CHUCK COOPER / 705-788-4320
CLLI GRVNON31		SC GRAVENHURST	NETWORK# S47411
			PLAN 623

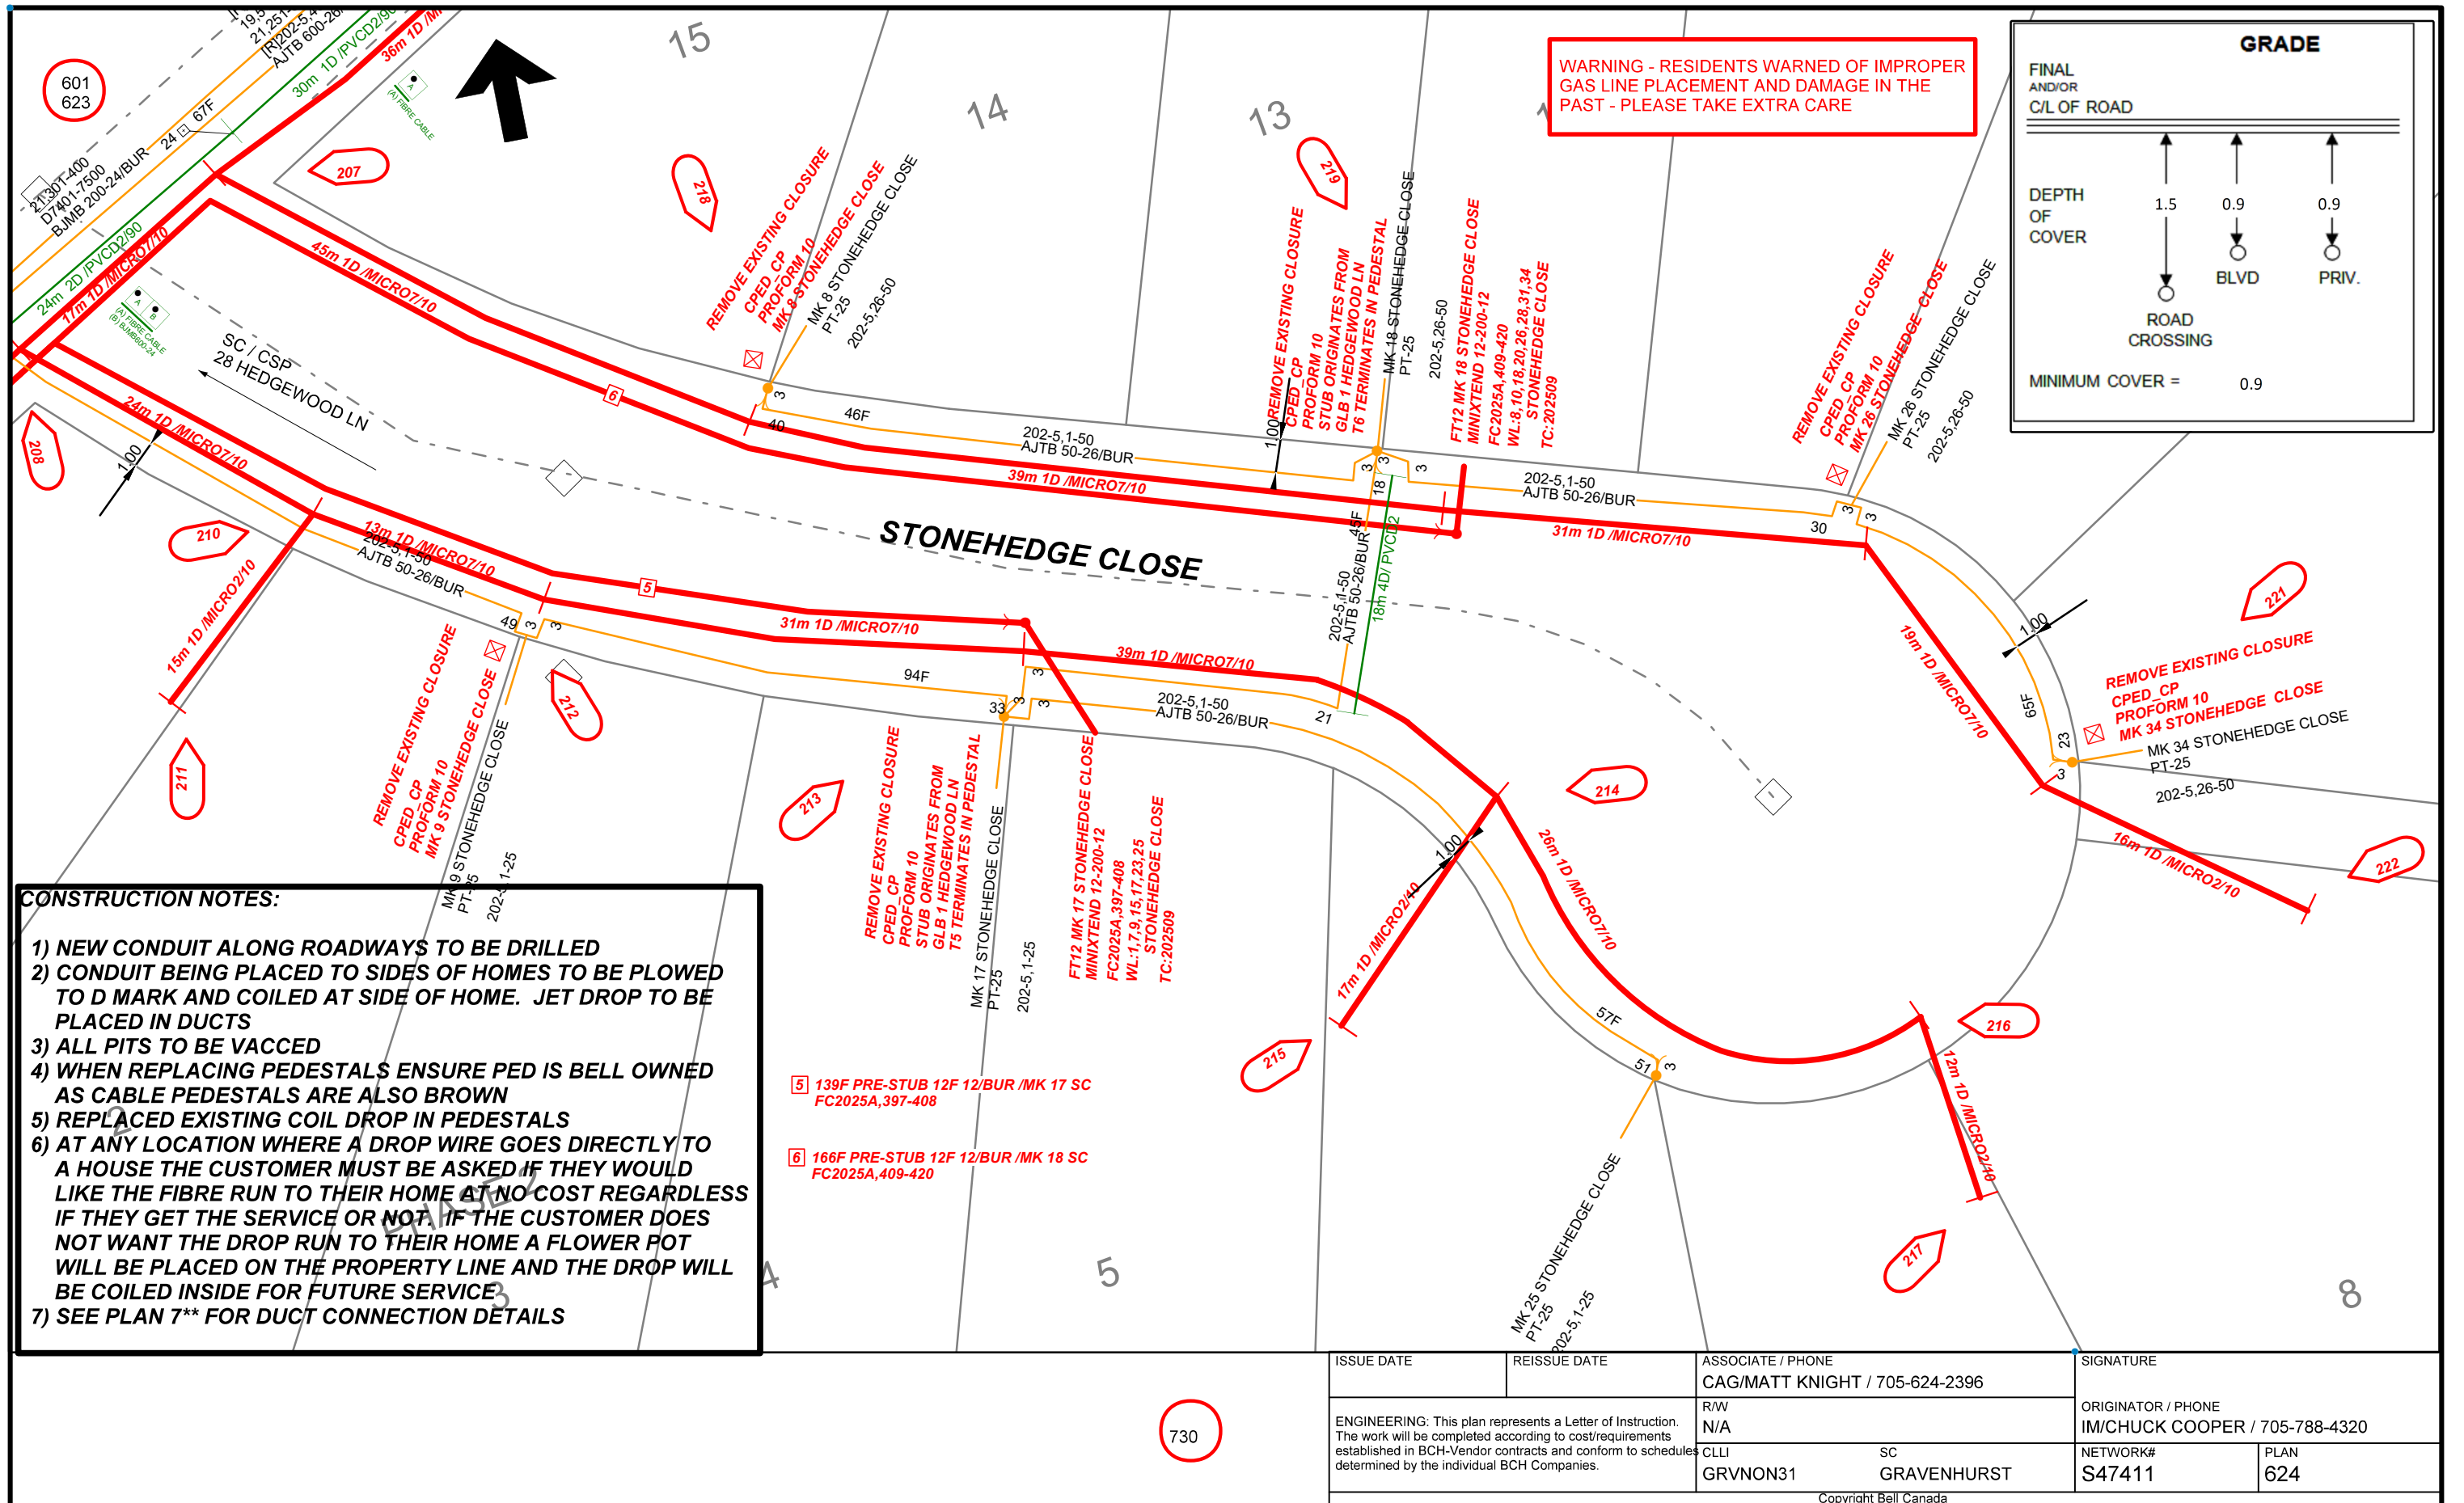



CONSTRUCTION NOTES:
1) PULL NEW FIBRE CABLE THROUGH EXISTING CONDUIT FROM P 275 FAIRVIEW DR TO NEW GLB 28-1 HEDGEWOOD LN
2) COIL 25m AT BASE OF POLE FOR FUTURE

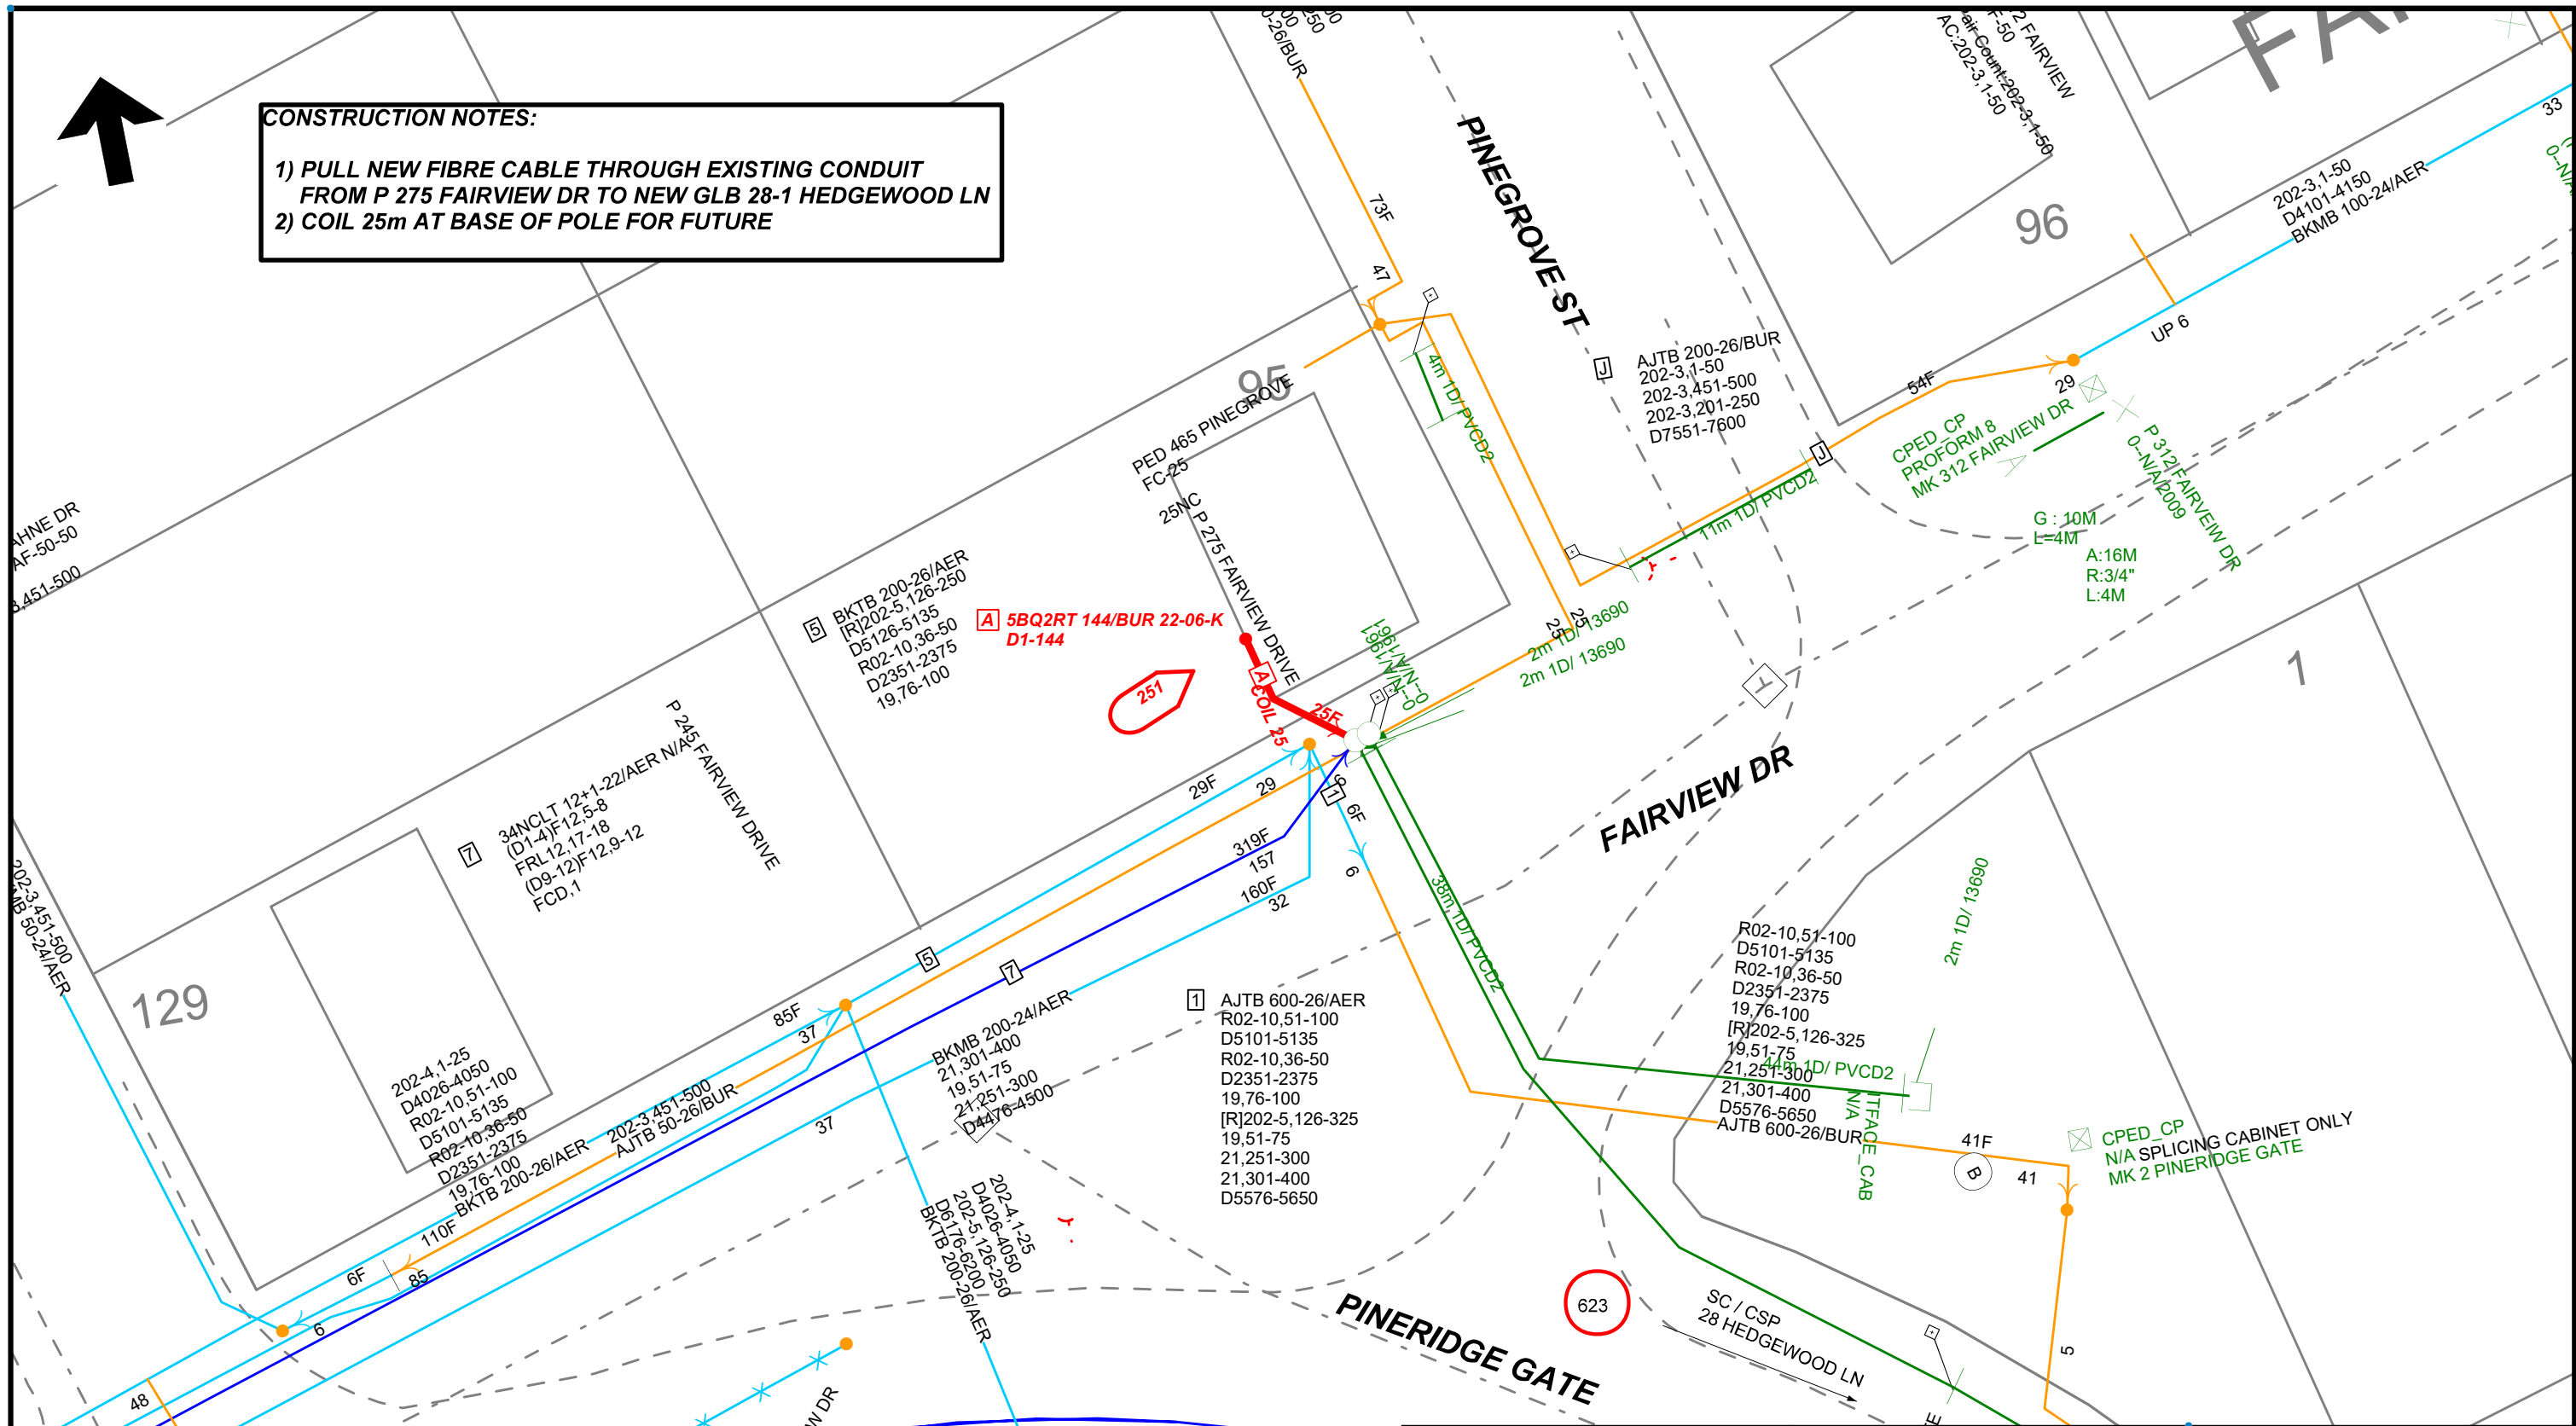

- 1) OPEN EXISTING SPLICE AT ARB 237 AND SPLICE IN NEW FIBRE CABLE
- 2) SEE PLAN 601 FOR REMOTE LOCATION


AN03,1-384
D3385-3900
AJMB 900-24/BUR

MK 28 HEDGEWOOD LN
 OPI
 202-5
 RES
 IN_BP:1-96:AN03,1-96
 IN_BP:96-100:4D
 IN_BP:101-196:AN03,97-192
 IN_BP:197-200:4D
 IN_BP:201-296:AN03,193-288
 IN_BP:297-300:4D
 IN_BP:301-396:AN03,289-384
 IN_BP:397-400:4D
 IN_BP:401-500:21,301-400
 IN_BP:501-525:19,51-75
 IN_BP:526-575:21,251-300
 IN_BP:576-675:100VAC
 IN_BP:676-700:19,76-100
 OUT_BP:1-100:202-5,1-100
 OUT_BP:101-125:25VAC
 OUT_BP:126-325:202-5,126-325
 OUT_BP:326-350:25SP
 OUT_BP:351-400:50SP
 OUT_BP:401-600:202-5,401-600
 OUT_BP:601-1200:202-5,601-1200
 OUT_BP:1201-1300:100VAC
 IN_BP:1301-1400:100VAC

- ☒ Splicing
- ☐ Pulling over existing fibre
- ☐ Digging near existing fibre
- ☐ Break Duct containing fibre

Call to Close ticket when complete

Refer to Simplified MOP (SMOP) and CRSF included with work plans for additional details

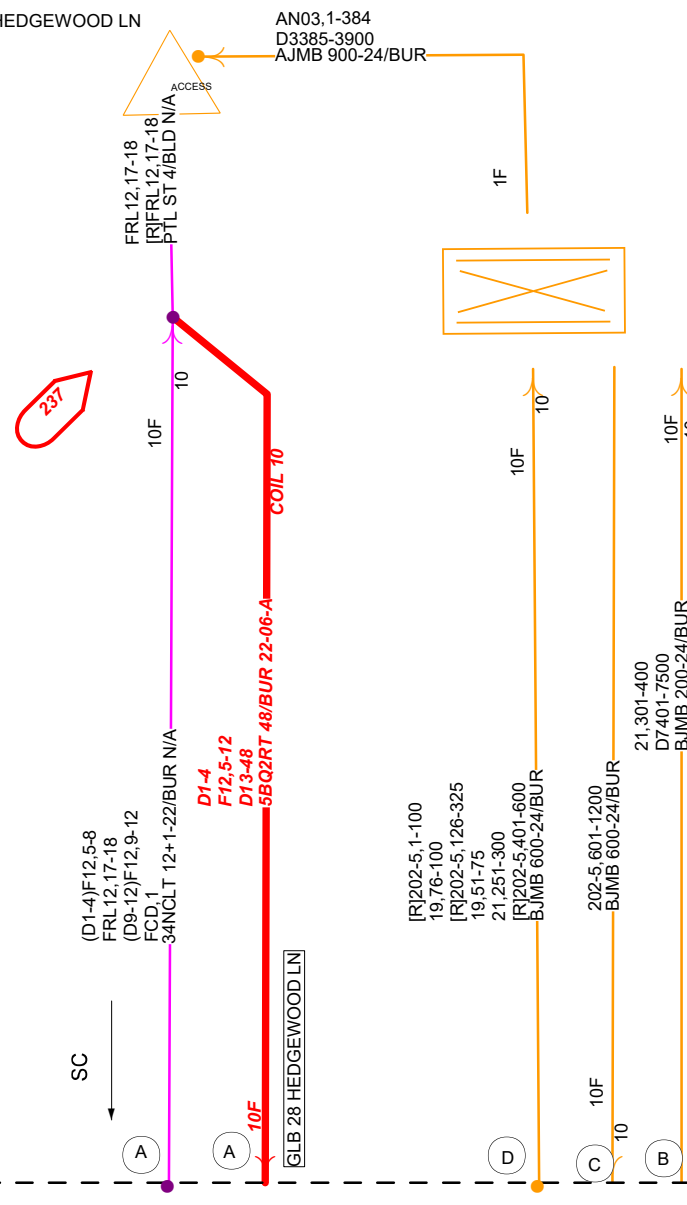


TYPE: OTHER
NAME: PINERIDGE
NUMBER:
MAIN+STREET:

— REMOTE_EQUIP
N/A


625

730

ISSUE DATE	REISSUE DATE	ASSOCIATE / PHONE CAG/MATT KNIGHT / 705-624-2396	SIGNATURE		
ENGINEERING: This plan represents a Letter of Instruction. The work will be completed according to cost/requirements established in BCH-Vendor contracts and conform to schedules determined by the individual BCH Companies.		R/W N/A	ORIGINATOR / PHONE IM/CHUCK COOPER / 705-788-4320		
		CLLI GRVNON31	SC GRAVENHURST	NETWORK# S47411	PLAN 626
		Copyright Bell Canada			

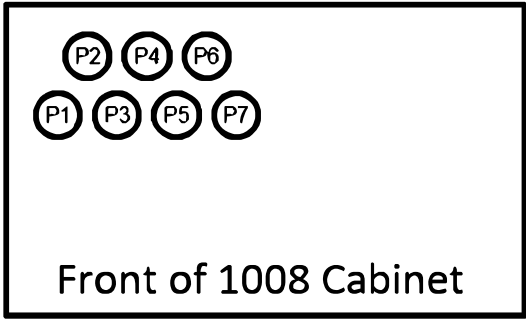

CSP 28 WEDGEWOOD LN
1008M2
2025A
RES
GRVNONJ3004
202509
087614NM
MOD 1-18:PORT 1-432:FC2025A,1-432
MOD 19-40:PORT 433-960:528VAC
MOD 41:PORT 961-984:24RES
MOD 42:PORT 985-988:D1-4
MOD 42:PORT 989-996:F12,5-12
MOD 42:PORT 997-1008:D13-24

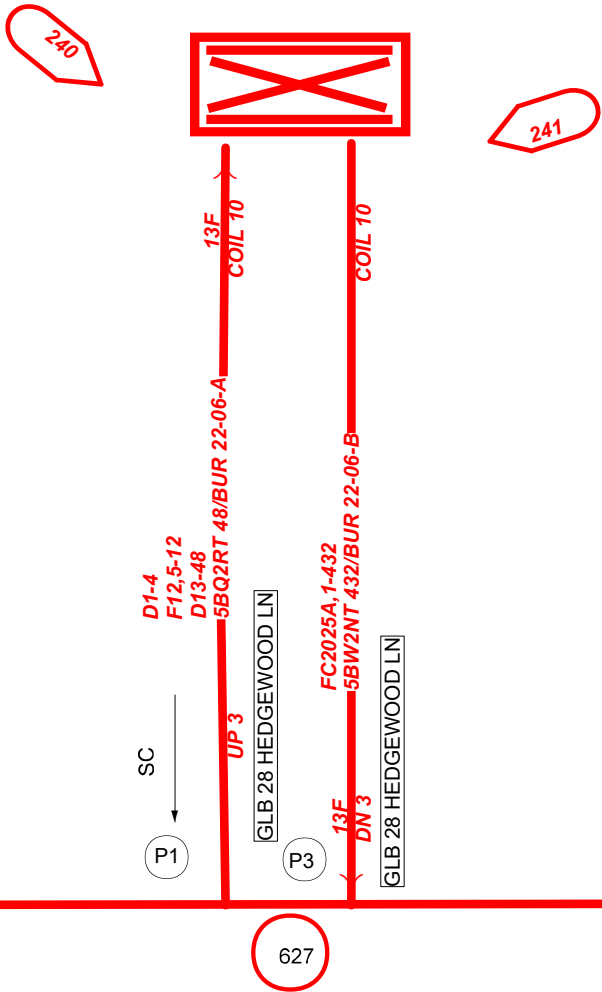

Threat Ticket Change
is required on this workplan for the following work:

- ☒ Splicing
- ☐ Pulling over existing fibre
- ☐ Digging near existing fibre
- ☐ Break Duct containing fibre

Prior to starting work - Call
TNOC 800-588-6870
Call to Close ticket when complete

Refer to Simplified MOP (SMOP) and CRSF included with work plans for additional details

- CONSTRUCTION NOTES:**
- 1) PLACE CSP-M2 PAD (S/C 087614NM)
 - 2) PLACE 2-MOD CSP M2 24 SM SCA RIBBONS (S/C 059120NM)
 - 3) PLACE 5 x 32 PORT CSP-M2 SPLITTERS (S/C 027339NM)
 - 4) PLACE 18-MOD M2 24 SM SCA RIBBONS (059120NM)
 - 5) PULL NEW CABLES THROUGH NEWLY PLACED DUCT
 - 6) SEE PLAN 601 FOR CSP LOCATION

ITFACE_CAB
CSP GLB
CSP 28 HEDGEWOOD LN

FINAL LENGTH 5BQ2RT-48 = 40m BUR

730

ISSUE DATE	REISSUE DATE	ASSOCIATE / PHONE CAG/MATT KNIGHT / 705-624-2396	SIGNATURE
ENGINEERING: This plan represents a Letter of Instruction. The work will be completed according to cost/requirements established in BCH-Vendor contracts and conform to schedules determined by the individual BCH Companies.		R/W N/A	ORIGINATOR / PHONE IM/CHUCK COOPER / 705-788-4320
CLLI GRVNON31		SC GRAVENHURST	NETWORK# S47411
			PLAN 628

is required on this workplan for the following work:

- Prior to starting work - Call
TNOC 800-588-6870
 Call to Close ticket when complete

Copyright Bell Canada

- 1

20F PRE-STUB 8F 8/BUR /MK 160 HL
FC2025A,89-96
- 2

20F PRE-STUB 12F 12/BUR /MK 187 PG
FC2025A,109-120
- 3

20F PRE-STUB 6F 6/BUR /MK 4 RM
FC2025A,121-126
- 4

20F PRE-STUB 8F 8/BUR /MK 3 RM
FC2025A,81-88
- 5

20F PRE-STUB 12F 12/BUR /MK 13 RM
FC2025A,97-108
- 6

20F PRE-STUB 8F 8/BUR /MK 173 PG
FC2025A,73-80

CONSTRUCTION NOTES:

1) PULL NEW CABLES & MPT'S THROUGH NEW DUCTS
2) CREATE NEW 919R SPLICE AT ARB 246 AND SPLICE NEW CABLES
3) SEE PLAN 607 FOR GLB LOCATION

Threat Ticket Change
is required on this workplan for the following work:

☒ Splicing
☐ Pulling over existing fibre
☐ Digging near existing fibre
☐ Break Duct containing fibre

Prior to starting work - Call
TNOC 800-588-6870
Call to Close ticket when complete

Refer to Simplified MOP (SMOP) and CRSF included with work plans for additional details

FINAL LENGTH 5BDXLT-144 = 328m BUR
FINAL LENGTH 5BDXLT-72 = 689m BUR

ISSUE DATE	REISSUE DATE	ASSOCIATE / PHONE CAG/MATT KNIGHT / 705-624-2396	SIGNATURE
ENGINEERING: This plan represents a Letter of Instruction. The work will be completed according to cost/requirements established in BCH-Vendor contracts and conform to schedules determined by the individual BCH Companies.		R/W N/A	ORIGINATOR / PHONE IM/CHUCK COOPER / 705-788-4320
CLLI GRVNON31	SC GRAVENHURST	NETWORK# S47411	PLAN 631

Copyright Bell Canada

Threat Ticket Change

is required on this workplan for the following work:

- ☒ Splicing
- ☐ Pulling over existing fibre
- ☐ Digging near existing fibre
- ☐ Break Duct containing fibre


Prior to starting work - Call
TNOC 800-588-6870
Call to Close ticket when complete

Refer to Simplified MOP (SMOP) and CRSF included with work plans for additional details

CONSTRUCTION NOTES:

1) PULL NEW CABLES & MPT'S THROUGH NEW DUCTS
2) CREATE NEW 919R SPLICE AT ARB 247 AND SPLICE NEW CABLES
3) SEE PLAN 612 FOR GLB LOCATION

HH-GLB 140 PINERIDGE GATE
GRADE LEVEL BOX 3048
30X48X36

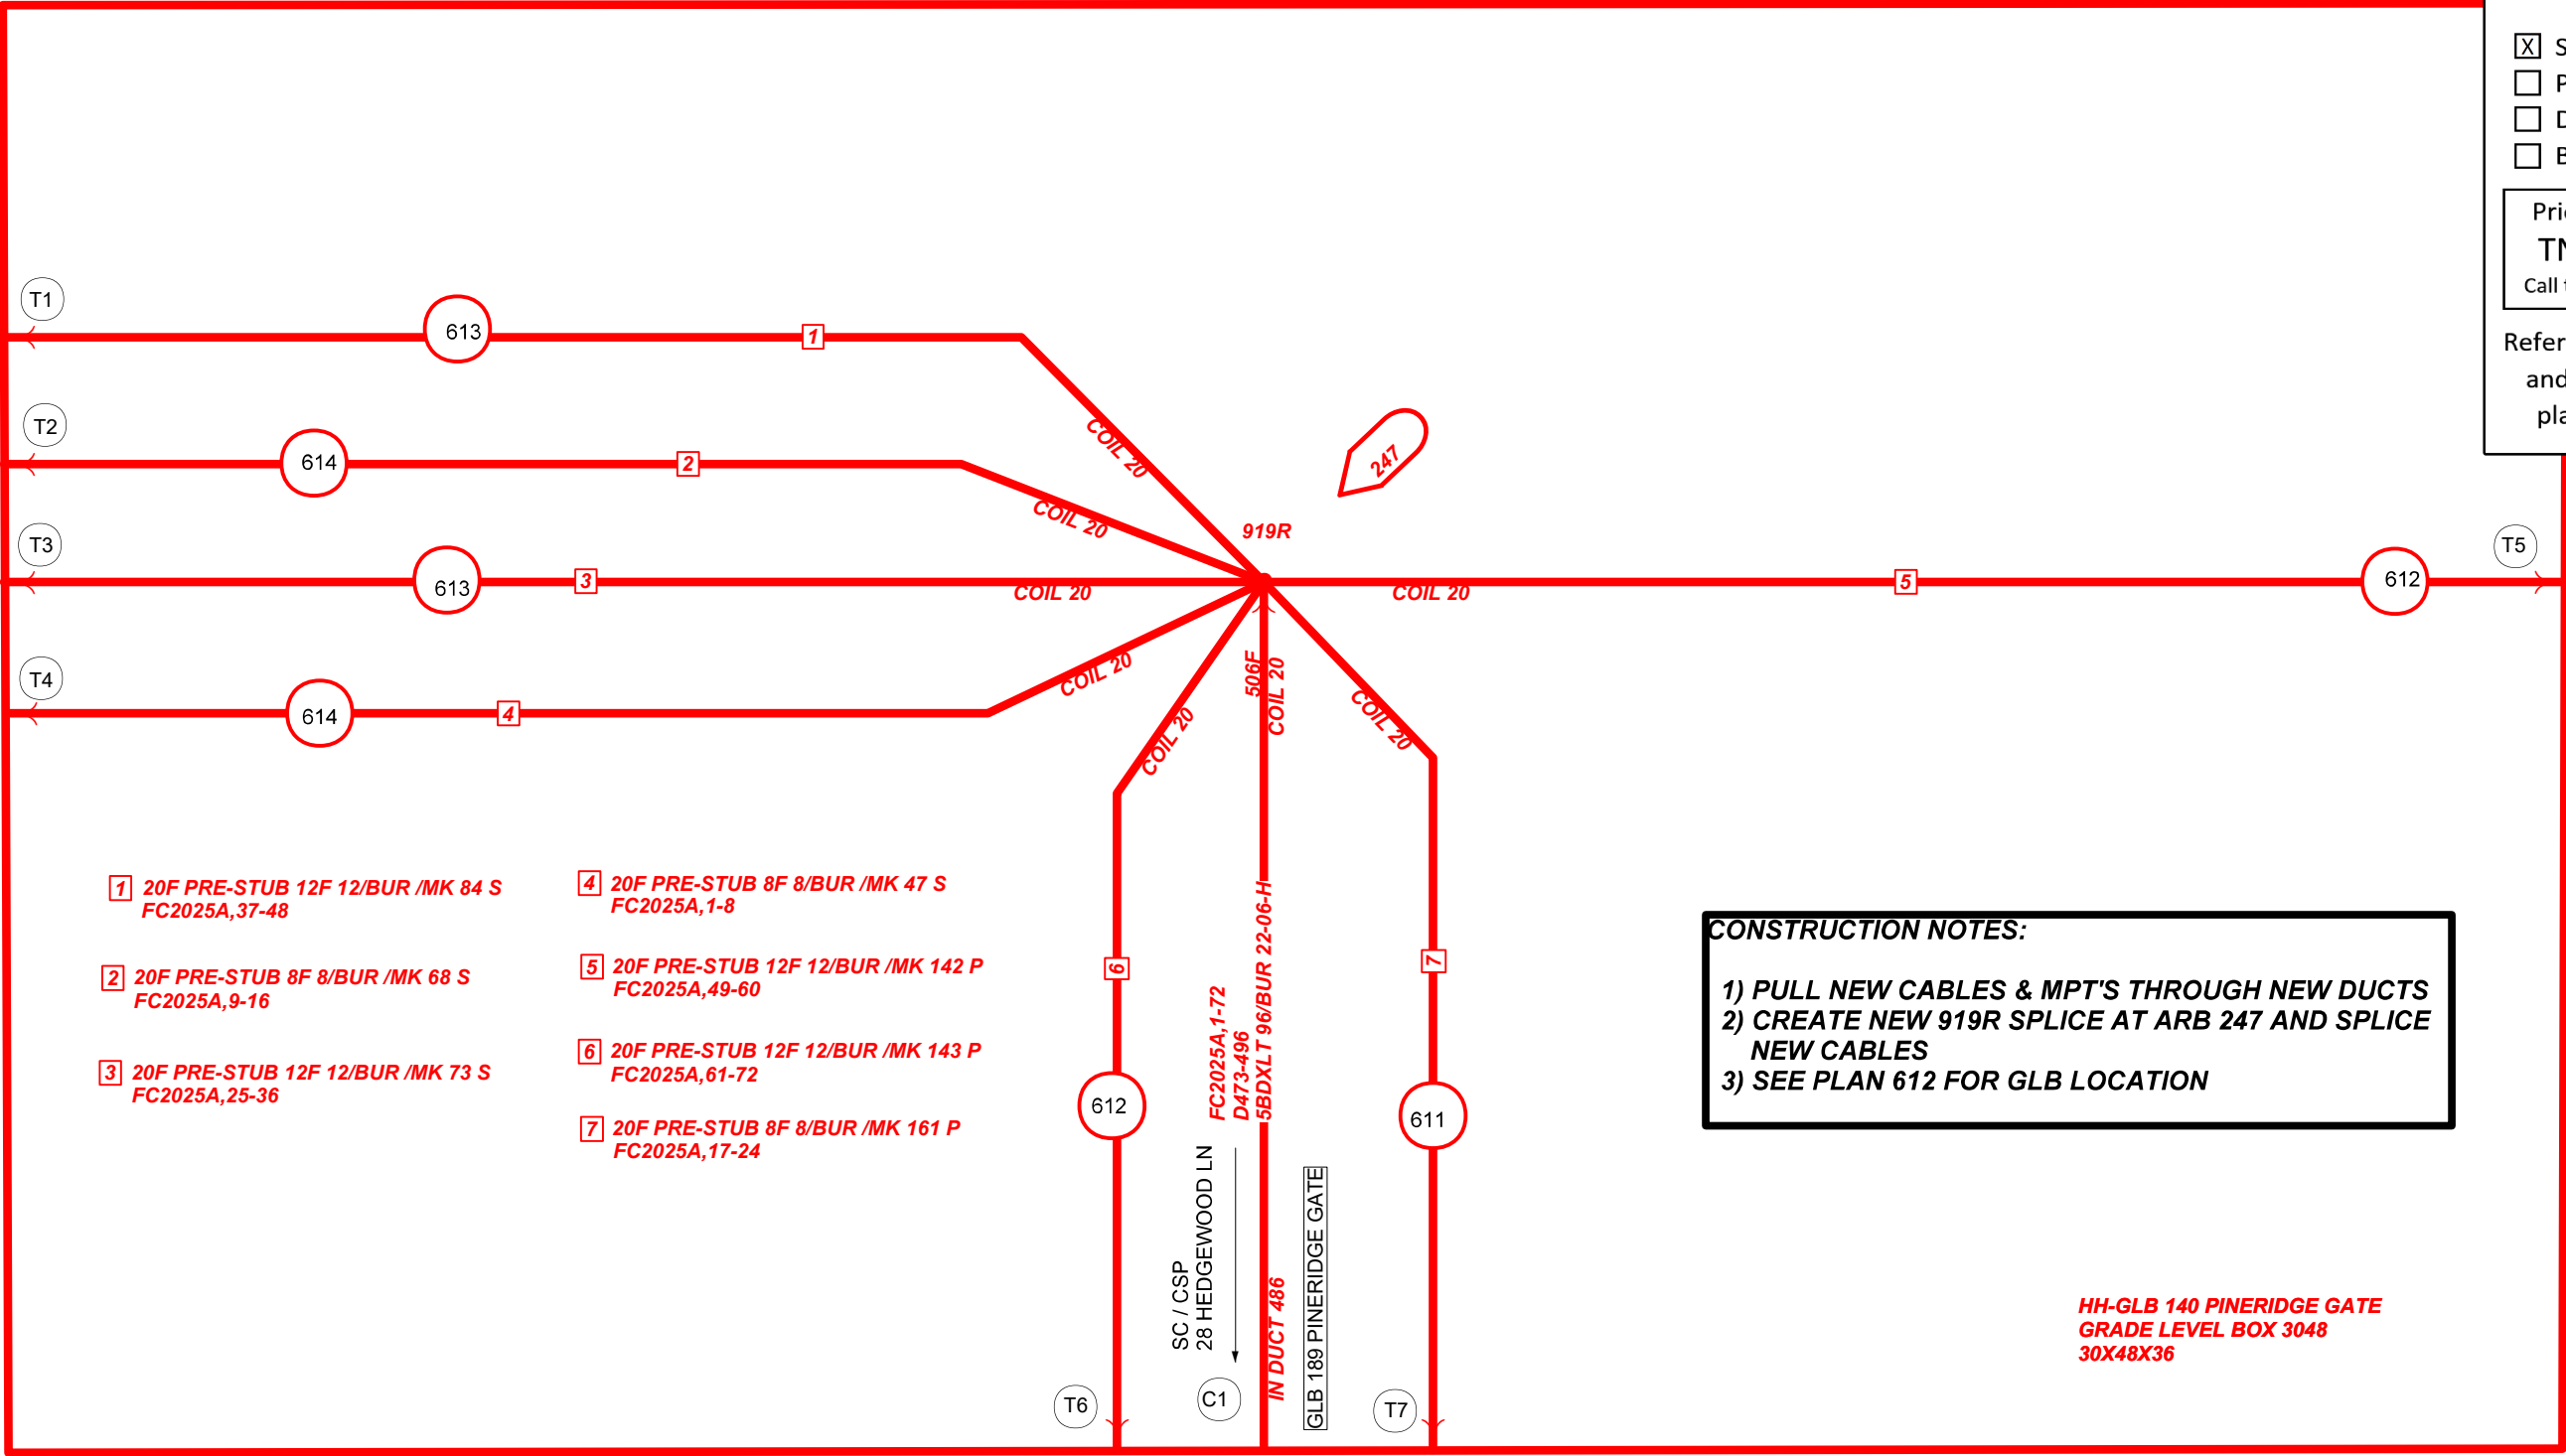

FINAL LENGTH 5BDXLT-96 = 526m BUR

730

ISSUE DATE	REISSUE DATE	ASSOCIATE / PHONE CAG/MATT KNIGHT / 705-624-2396	SIGNATURE
ENGINEERING: This plan represents a Letter of Instruction. The work will be completed according to cost/requirements established in BCH-Vendor contracts and conform to schedules determined by the individual BCH Companies.		R/W N/A	ORIGINATOR / PHONE IM/CHUCK COOPER / 705-788-4320
CLLI GRVNON31		SC GRAVENHURST	NETWORK# S47411
			PLAN 632

Threat Ticket Change

is required on this workplan for the following work:


- ☒ Splicing
- ☐ Pulling over existing fibre
- ☐ Digging near existing fibre
- ☐ Break Duct containing fibre

Prior to starting work - Call
TNOC 800-588-6870
Call to Close ticket when complete

Refer to Simplified MOP (SMOP)
and CRSF included with work
plans for additional details

CONSTRUCTION NOTES:

- 1) PULL NEW CABLES & MPT'S THROUGH NEW DUCTS
- 2) CREATE NEW 919R SPLICE AT ARB 247 AND SPLICE NEW CABLES
- 3) SEE PLAN 617 FOR GLB LOCATION

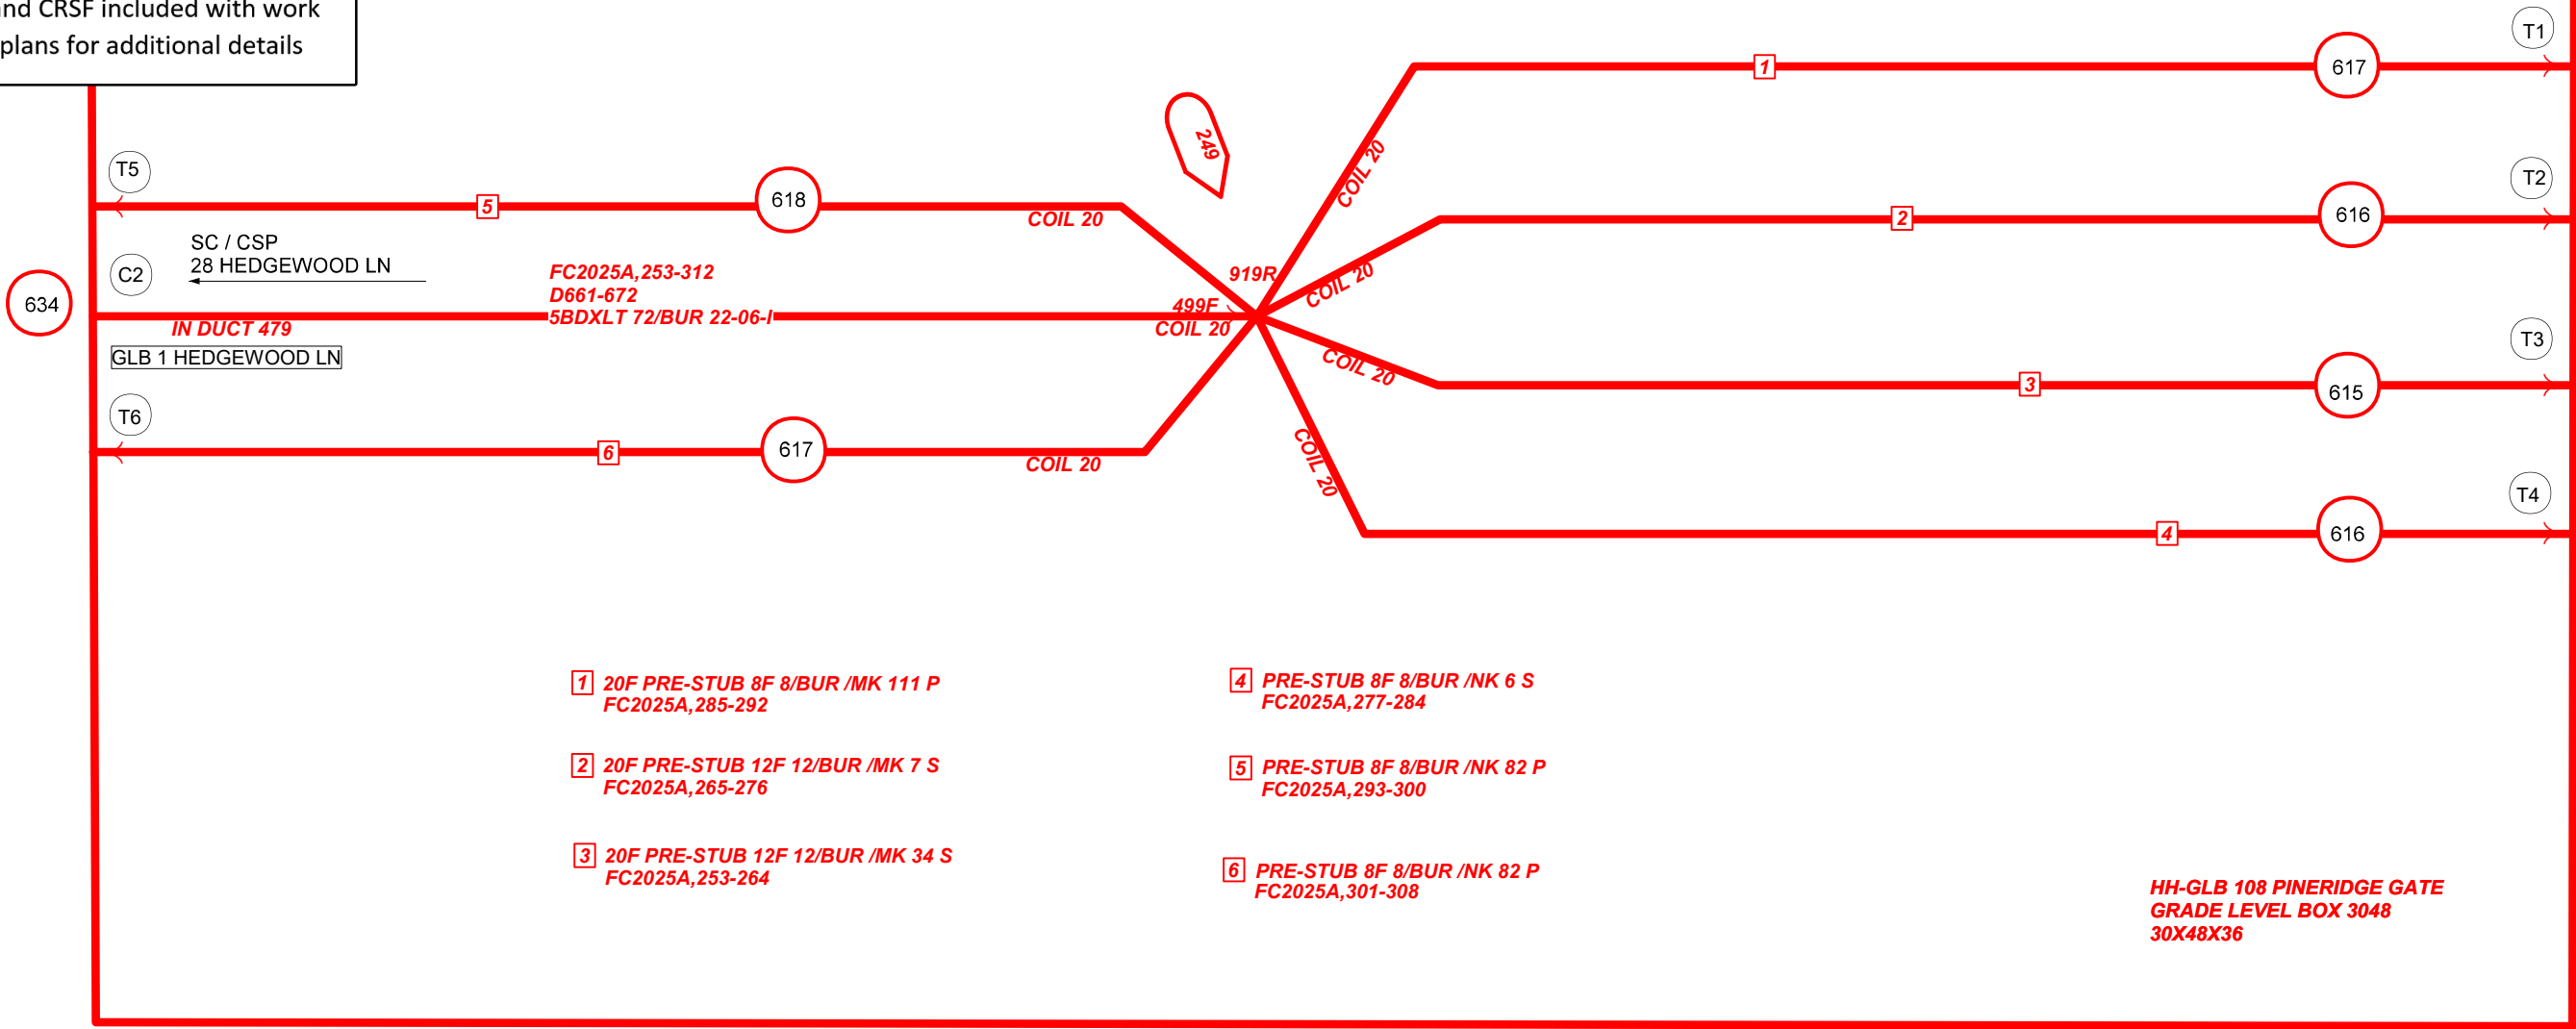

FINAL LENGTH 5BDXLT-72 = 519m BUR

730

ISSUE DATE	REISSUE DATE	ASSOCIATE / PHONE CAG/MATT KNIGHT / 705-624-2396	SIGNATURE
ENGINEERING: This plan represents a Letter of Instruction. The work will be completed according to cost/requirements established in BCH-Vendor contracts and conform to schedules determined by the individual BCH Companies.		R/W N/A	ORIGINATOR / PHONE IM/CHUCK COOPER / 705-788-4320
CLLI GRVNON31		SC GRAVENHURST	NETWORK# S47411
			PLAN 633


Threat Ticket Change

is required on this workplan for the following work:

- ☒ Splicing
- ☐ Pulling over existing fibre
- ☐ Digging near existing fibre
- ☐ Break Duct containing fibre

Prior to starting work - Call
TNOC 800-588-6870
Call to Close ticket when complete

Refer to Simplified MOP (SMOP) and CRSF included with work plans for additional details

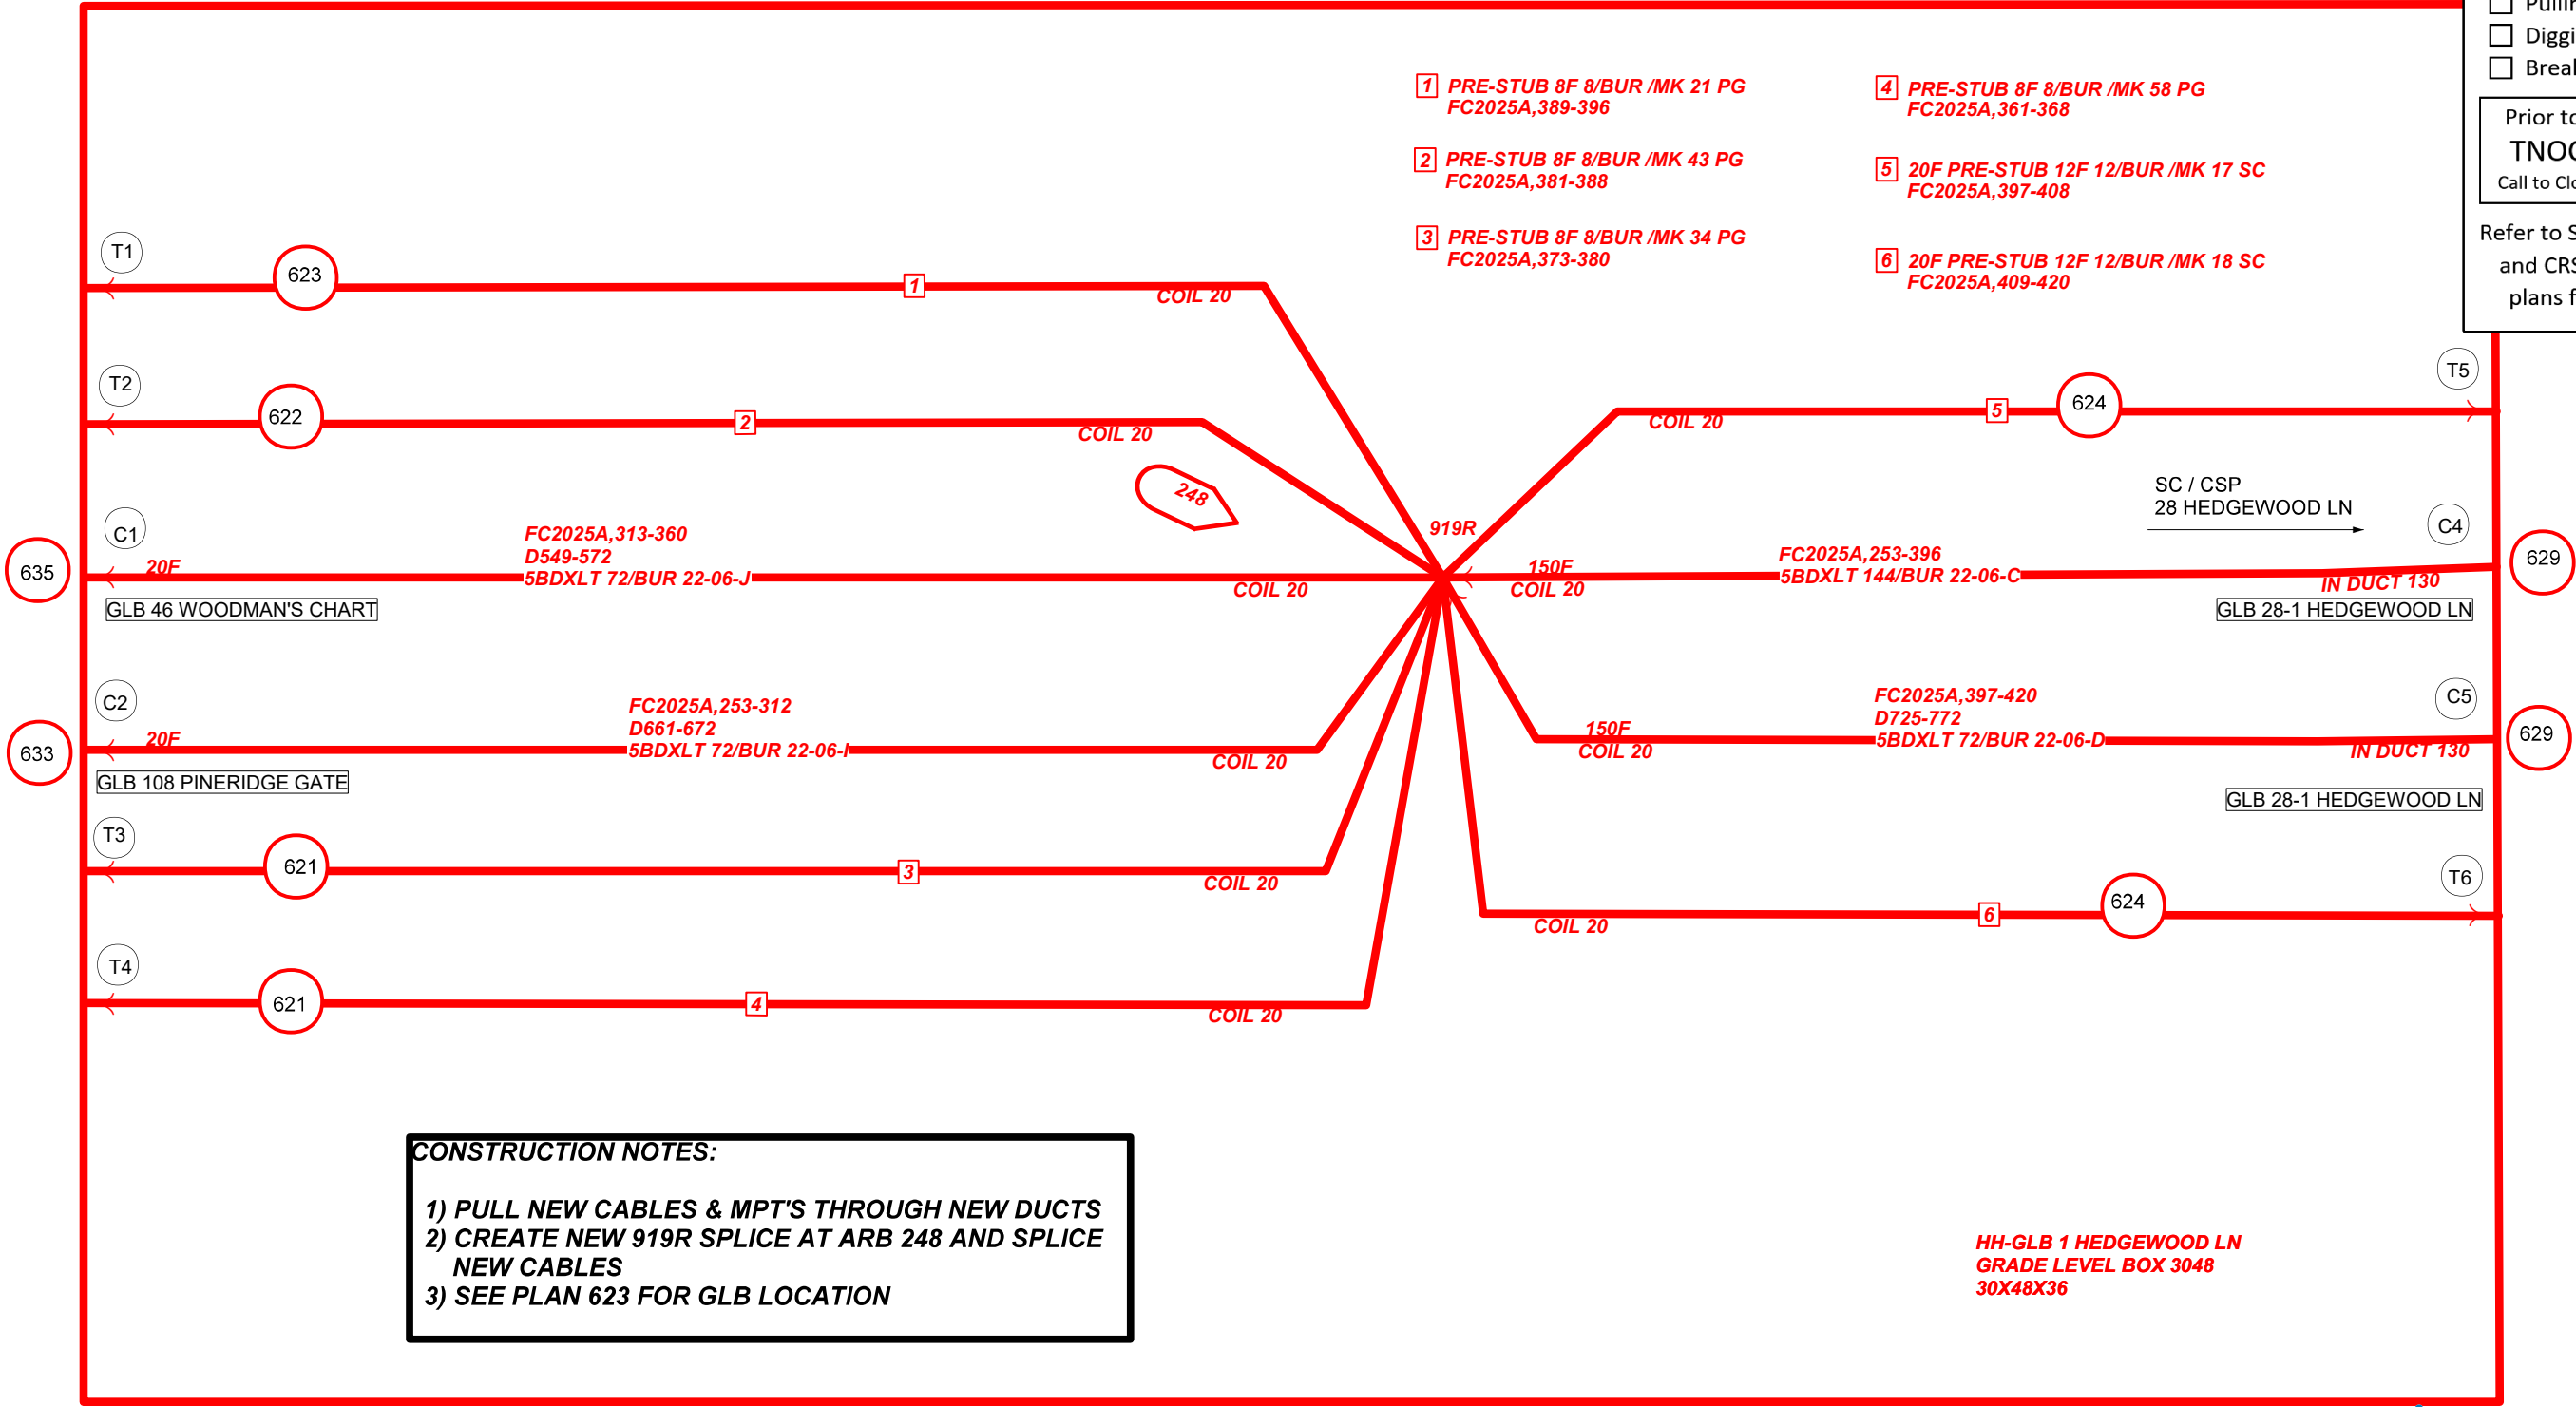

CONSTRUCTION NOTES:
1) PULL NEW CABLES & MPT'S THROUGH NEW DUCTS
2) CREATE NEW 919R SPLICE AT ARB 248 AND SPLICE NEW CABLES
3) SEE PLAN 623 FOR GLB LOCATION

FINAL LENGTH 5BDXLT-144 = 170m BUR

730

ISSUE DATE	REISSUE DATE	ASSOCIATE / PHONE CAG/MATT KNIGHT / 705-624-2396	SIGNATURE
ENGINEERING: This plan represents a Letter of Instruction. The work will be completed according to cost/requirements established in BCH-Vendor contracts and conform to schedules determined by the individual BCH Companies.		R/W N/A	ORIGINATOR / PHONE IM/CHUCK COOPER / 705-788-4320
CLLI GRVNON31		SC GRAVENHURST	NETWORK# S47411
			PLAN 634

Threat Ticket Change


is required on this workplan for the following work:

- ☒ Splicing
- ☐ Pulling over existing fibre
- ☐ Digging near existing fibre
- ☐ Break Duct containing fibre

Prior to starting work - Call
TNOC 800-588-6870

Call to Close ticket when complete

Refer to Simplified MOP (SMOP)
and CRSF included with work
plans for additional details

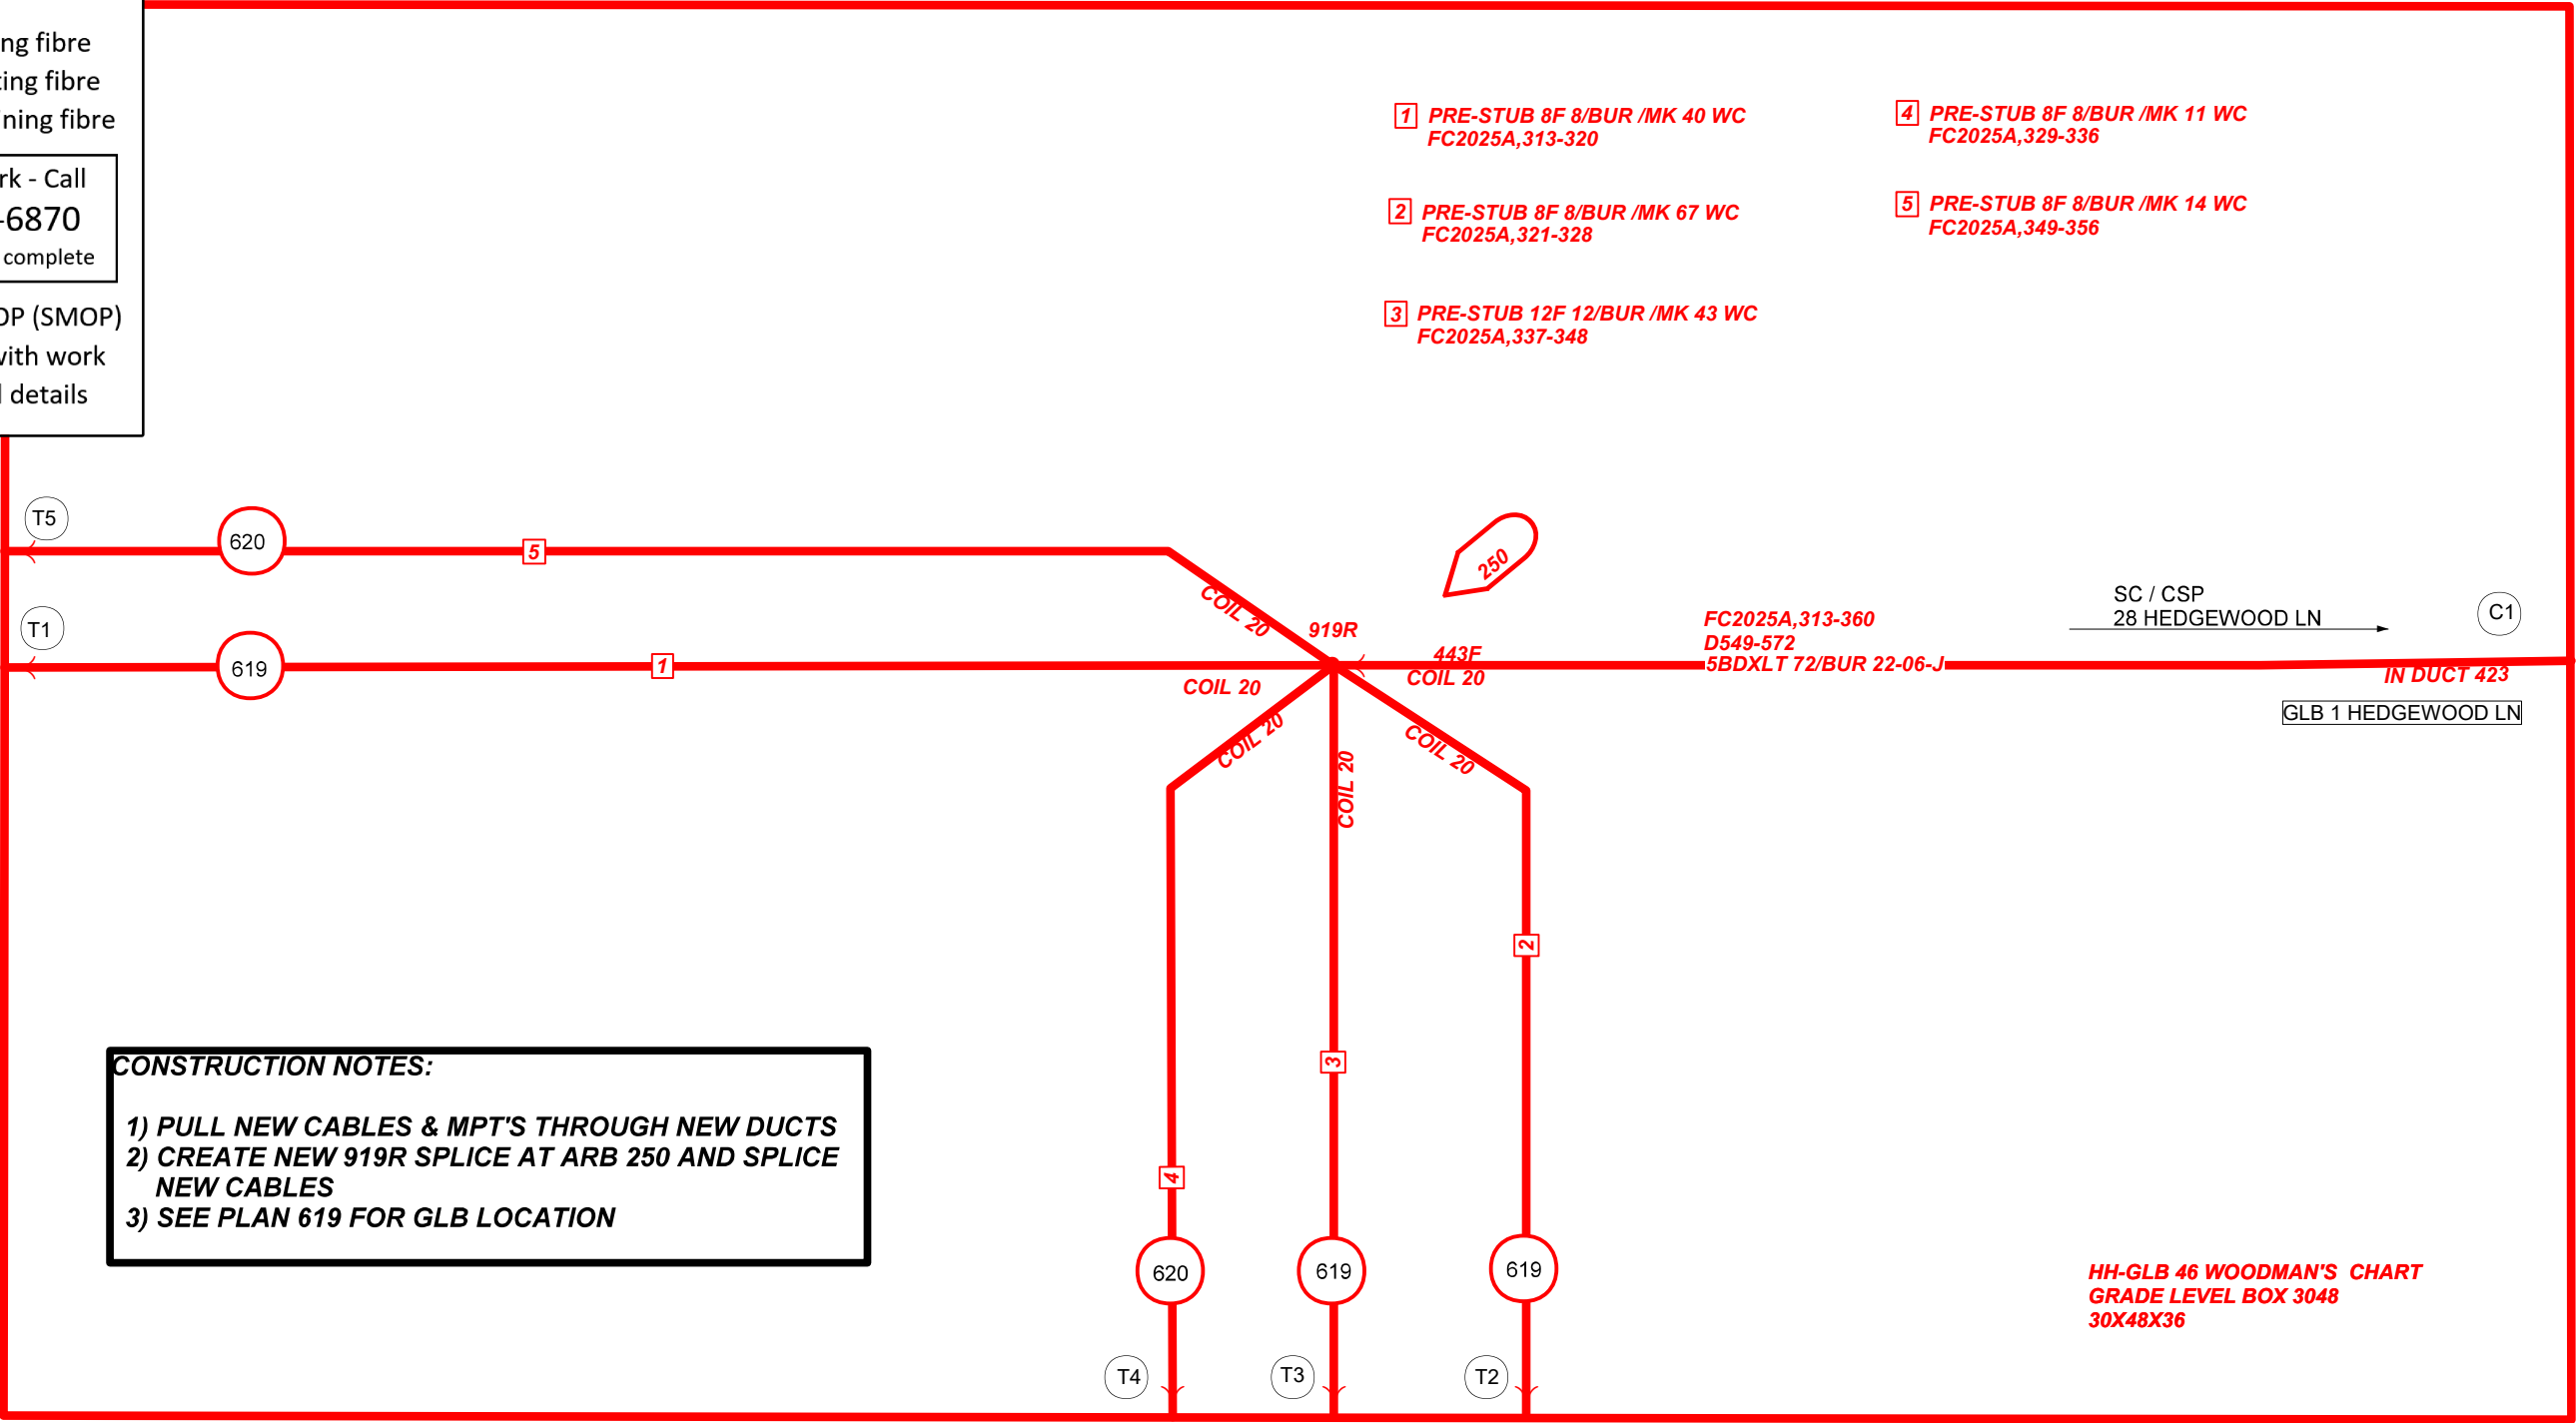

FINAL LENGTH 5BDXLT-72 = 463m BUR

730

ISSUE DATE	REISSUE DATE	ASSOCIATE / PHONE CAG/MATT KNIGHT / 705-624-2396	SIGNATURE
ENGINEERING: This plan represents a Letter of Instruction. The work will be completed according to cost/requirements established in BCH-Vendor contracts and conform to schedules determined by the individual BCH Companies.		R/W N/A	ORIGINATOR / PHONE IM/CHUCK COOPER / 705-788-4320
CLLI GRVNON31		SC GRAVENHURST	NETWORK# S47411
			PLAN 635

